


WINDOW SCHEDULE							
NUMBER	SIZE		STYLE	HEAD HEIGHT	SHCG	U-FACTOR	NOTES
	WIDTH	HEIGHT					
1	5'-0"	4'-0"	SLIDER	6'-8"	.23	.30	
2	5'-0"	4'-0"	SLIDER	6'-8"	.23	.30	
3	3'-0"	3'-0"	SLIDER	6'-8"	.23	.30	
4	5'-0"	4'-0"	SLIDER	6'-8"	.23	.30	
5	5'-0"	4'-0"	SLIDER	6'-8"	.23	.30	
6	5'-0"	4'-0"	SLIDER	6'-8"	.23	.30	
7	5'-0"	4'-0"	SLIDER	6'-8"	.23	.30	
8	3'-0"	1'-6"	SLIDER	6'-8"	.23	.30	
9	3'-0"	1'-6"	SLIDER	6'-8"	.23	.30	
10	5'-0"	4'-0"	SLIDER	6'-8"	.23	.30	


DOOR AND FRAME SCHEDULE

NUMBER	SIZE	STYLE	FIRE RATING	NOTES
1	3'-0" x 6'-8" x 1-3/4"	SINGLE - EXTERIOR	--	--
2	3'-0" x 6'-8" x 1-3/4"	SINGLE - INTERIOR	--	--
3	3'-0" x 6'-8" x 1-3/4"	BARN	--	--
4	3'-0" x 6'-8" x 1-3/4"	SINGLE - INTERIOR	--	--
5	2'-6" x 6'-8" x 1-3/4"	POCKET	--	--
6	3'-0" x 6'-8" x 1-3/4"	SINGLE - INTERIOR	--	--
7	3'-0" x 6'-8" x 1-3/4"	POCKET	--	--
8	3'-0" x 6'-8" x 1-3/4"	SINGLE - INTERIOR	--	--
9	3'-0" x 6'-8" x 1-3/4"	SINGLE - INTERIOR	--	--
10	3'-0" x 6'-8" x 1-3/4"	SINGLE - INTERIOR	--	--
11	PR 3'-0" x 6'-8" x 1-3/4"	HORIZONTAL BYPASS	--	--
12	PR 4'-0" x 6'-8" x 1-3/4"	HORIZONTAL BYPASS	--	--


REFERENCE KEYNOTES	
DIVISION 09 - FINISHES	
FLOORING -	
LVF	- LUXURY VINYL FLOORING
DIVISION 11 - EQUIPMENT	
D	- CLOTHES DRYER
DW18	- 18" DISHWASHER
FR36	- FRIDGE, 36" WIDE
MWOC	- MICROWAVE/ OVEN CABINET
W	- CLOTHES WASHER
DIVISION 12 - FURNISHINGS	
BC24	- 24" DEEP BASE CABINET
UC12	- 12" DEEP UPPER CABINET
DIVISION 15 - MECHANICAL	
HVAC	- HEATING, VENTILATING OR AIR CONDITIONING EQUIPMENT
MSH	- MINI SPLIT HEAD
WH-E	- WATER HEATER, ELECTRIC
DIVISION 16 - ELECTRICAL	
EPP	- ELECTRICAL SUB PANEL, 120/240V 125A, W/ UFER GROUND, PROVIDE 30"x30" WORKING AREA CENTERED IN FRONT OF PANEL
DIVISION 17 - PLUMBING	
BC-S	- BATHTUB SHOWER COMBO
SC30	- 30" SINK CABINET
SK-U	- UNDERMOUNT SINK
WC	- WATER CLOSET, MINIMUM 30" CLEAR WIDTH CENTERED ON WATER CLOSET & 24" CLEAR SPACE OFF NOSE OF WATER CLOSET.

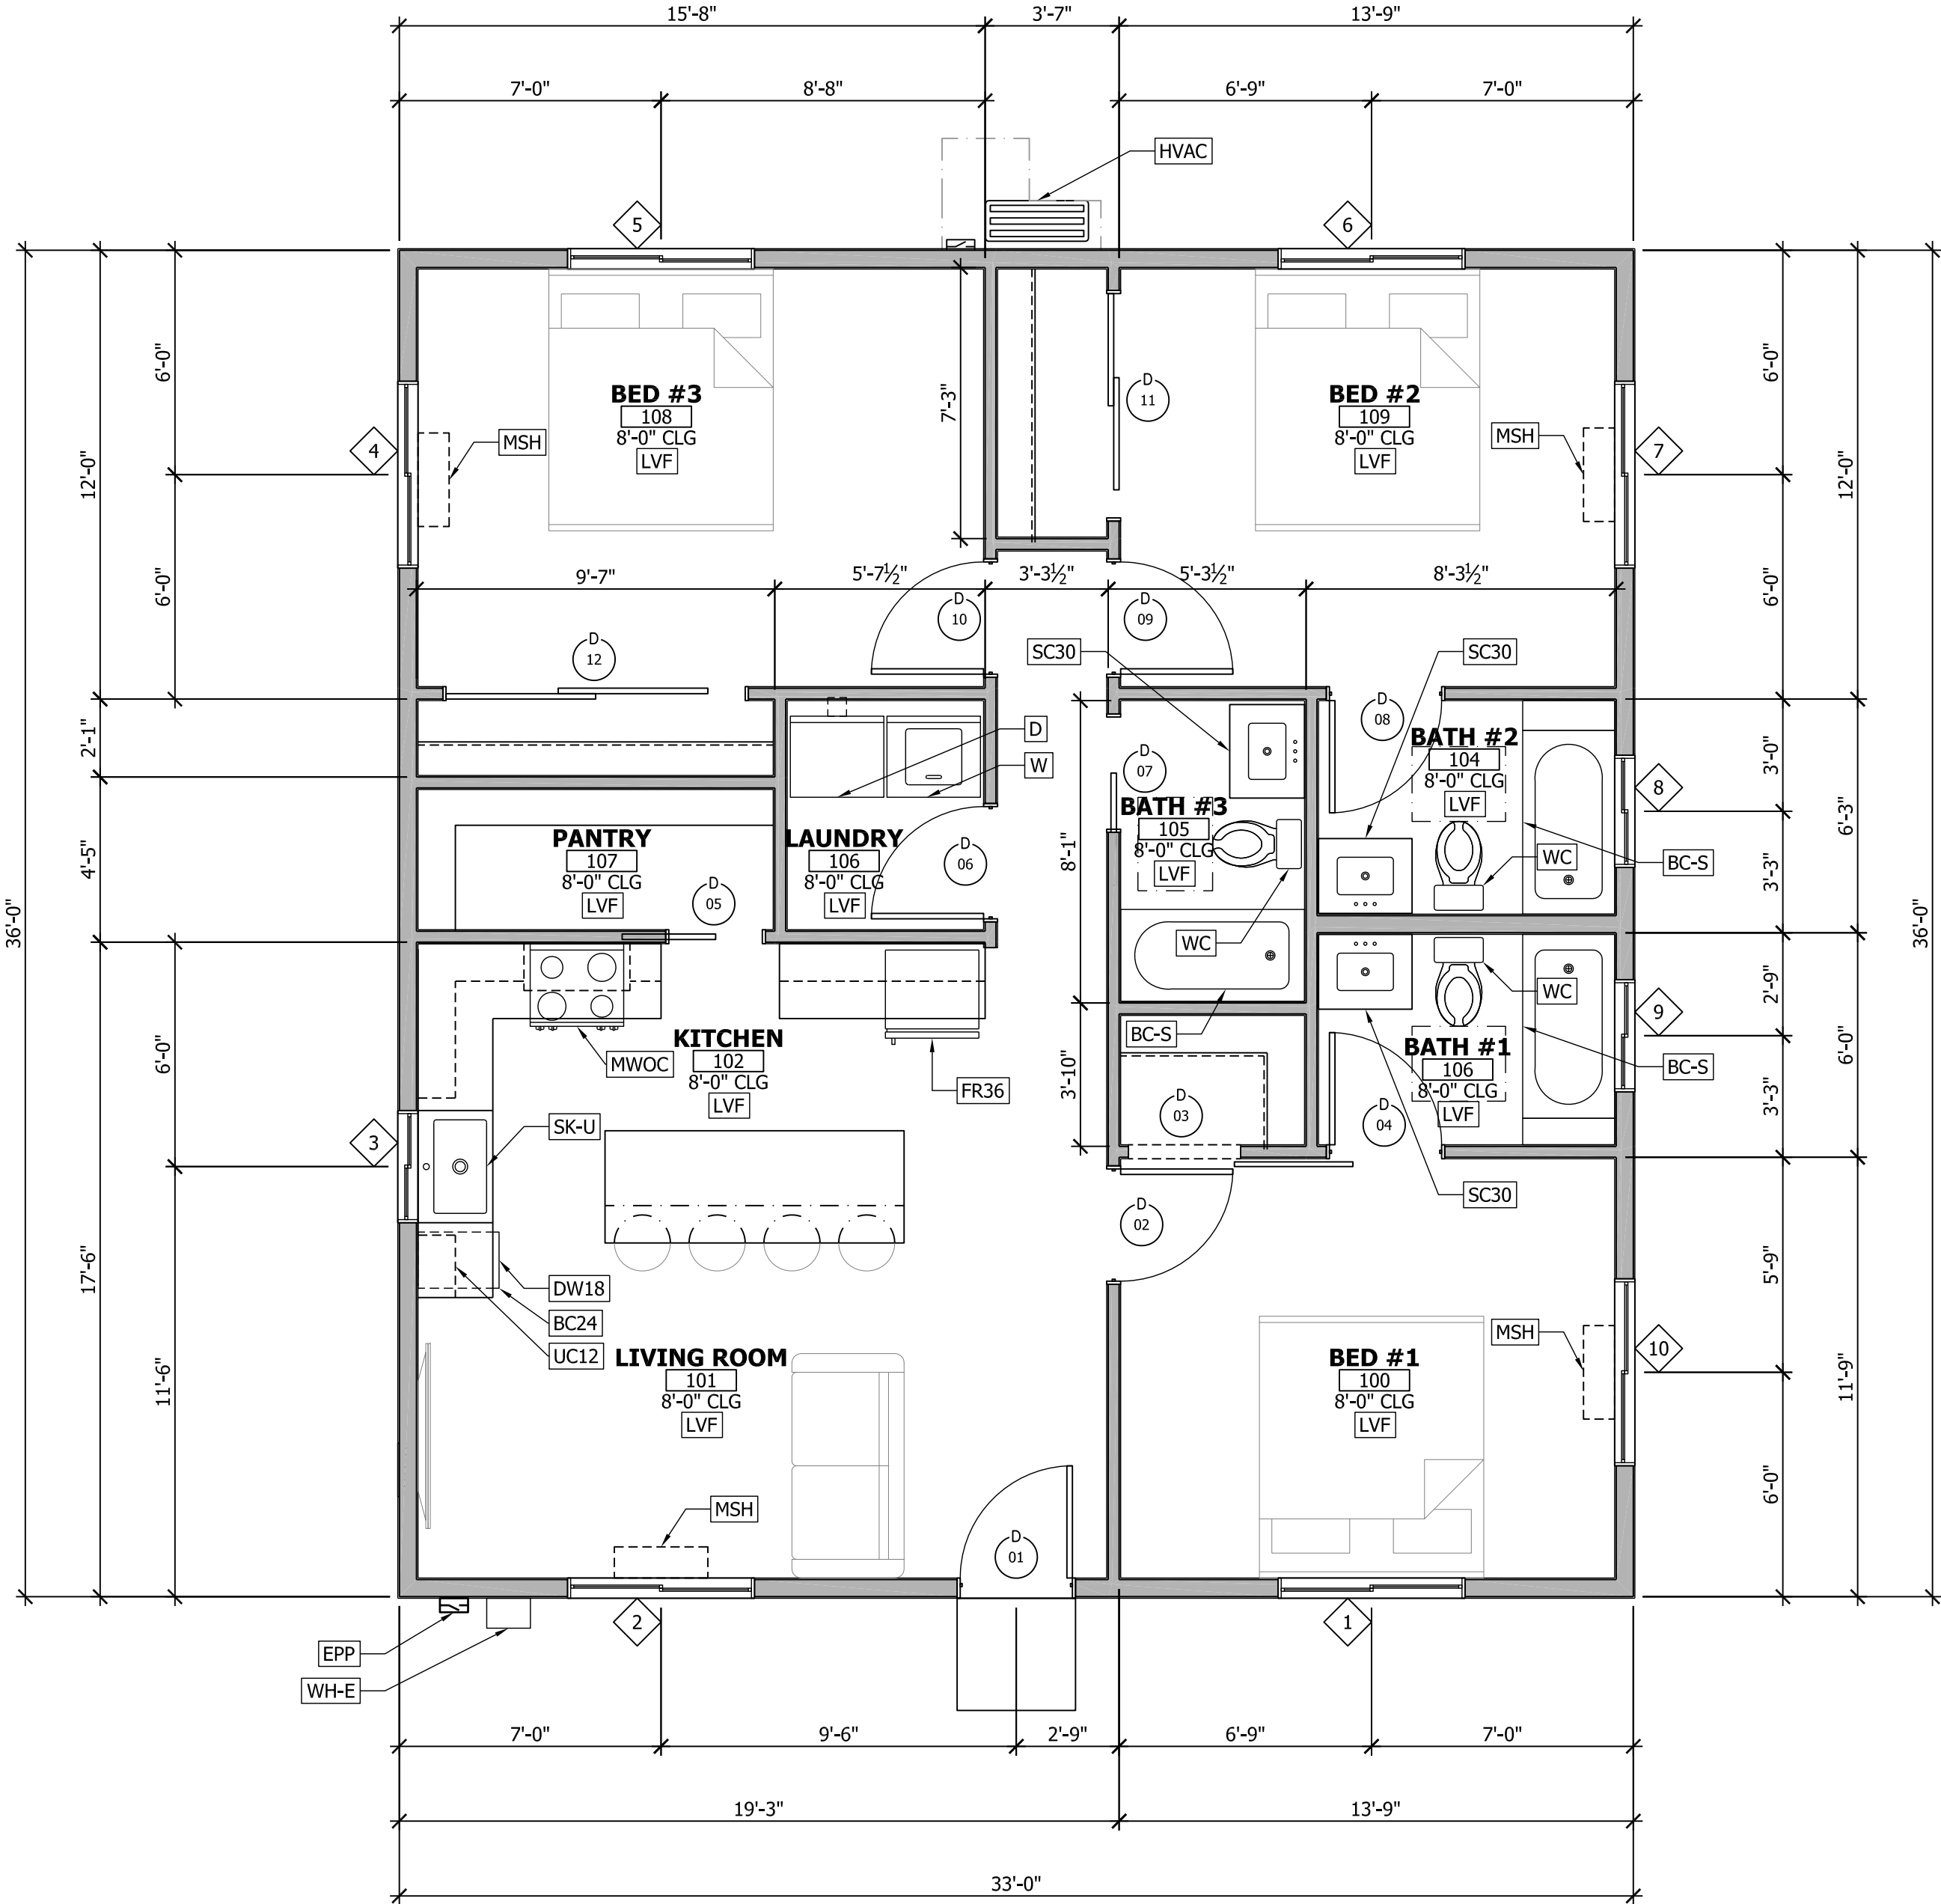


1 FLOOR PLAN

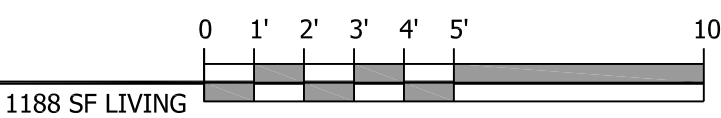


REFERENCE KEYNOTES		
DIVISION 06 - WOOD AND PLASTICS		
MISCELLANEOUS -		
WT24	-	2x4 WOOD TRIM
DIVISION 07 - THERMAL AND MOISTURE PROTECTION		
ROOFING AND SIDING -		
OHRV	-	0' HAGGIN ROOF VENT, TYP
SHG	-	CLASS 'A' LIFETIME COMPOSITION ROOF SHINGLES <i>o</i> / 15LB FELT COMPLIANT WITH TABLE R905.1(1). FASTEN ROOFING WITH CORROSION RESISTANT FASTENERS CRC R905.2.5
DIVISION 09 - FINISHES		
BBS	-	5/8" T1-11 BOARD AND BATTEN SIDING <i>o</i> / TWO LAYER GRADE 'D' PAPER OR 1 LAYER TYVEK. NAILING PER STRUCTURAL

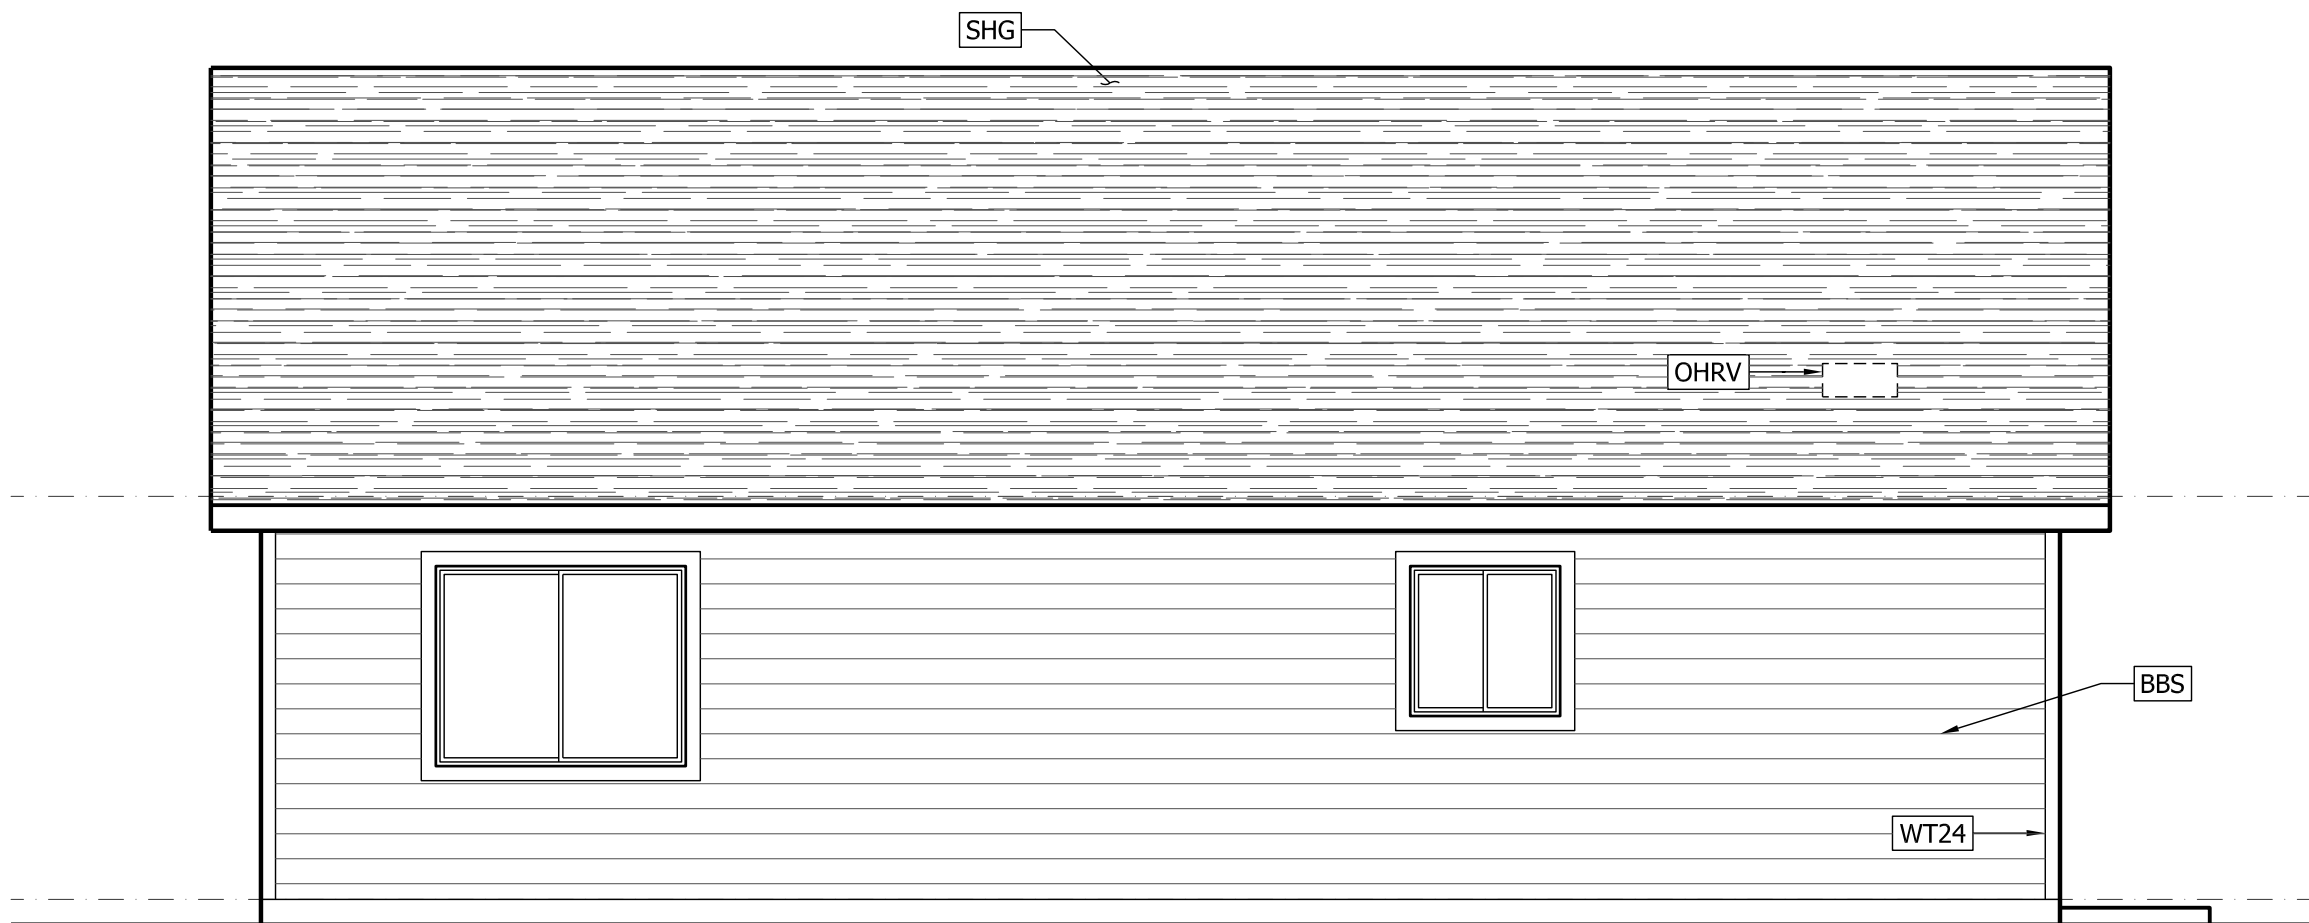


C LEFT ELEVATION
2 1/4" = 1'-0"

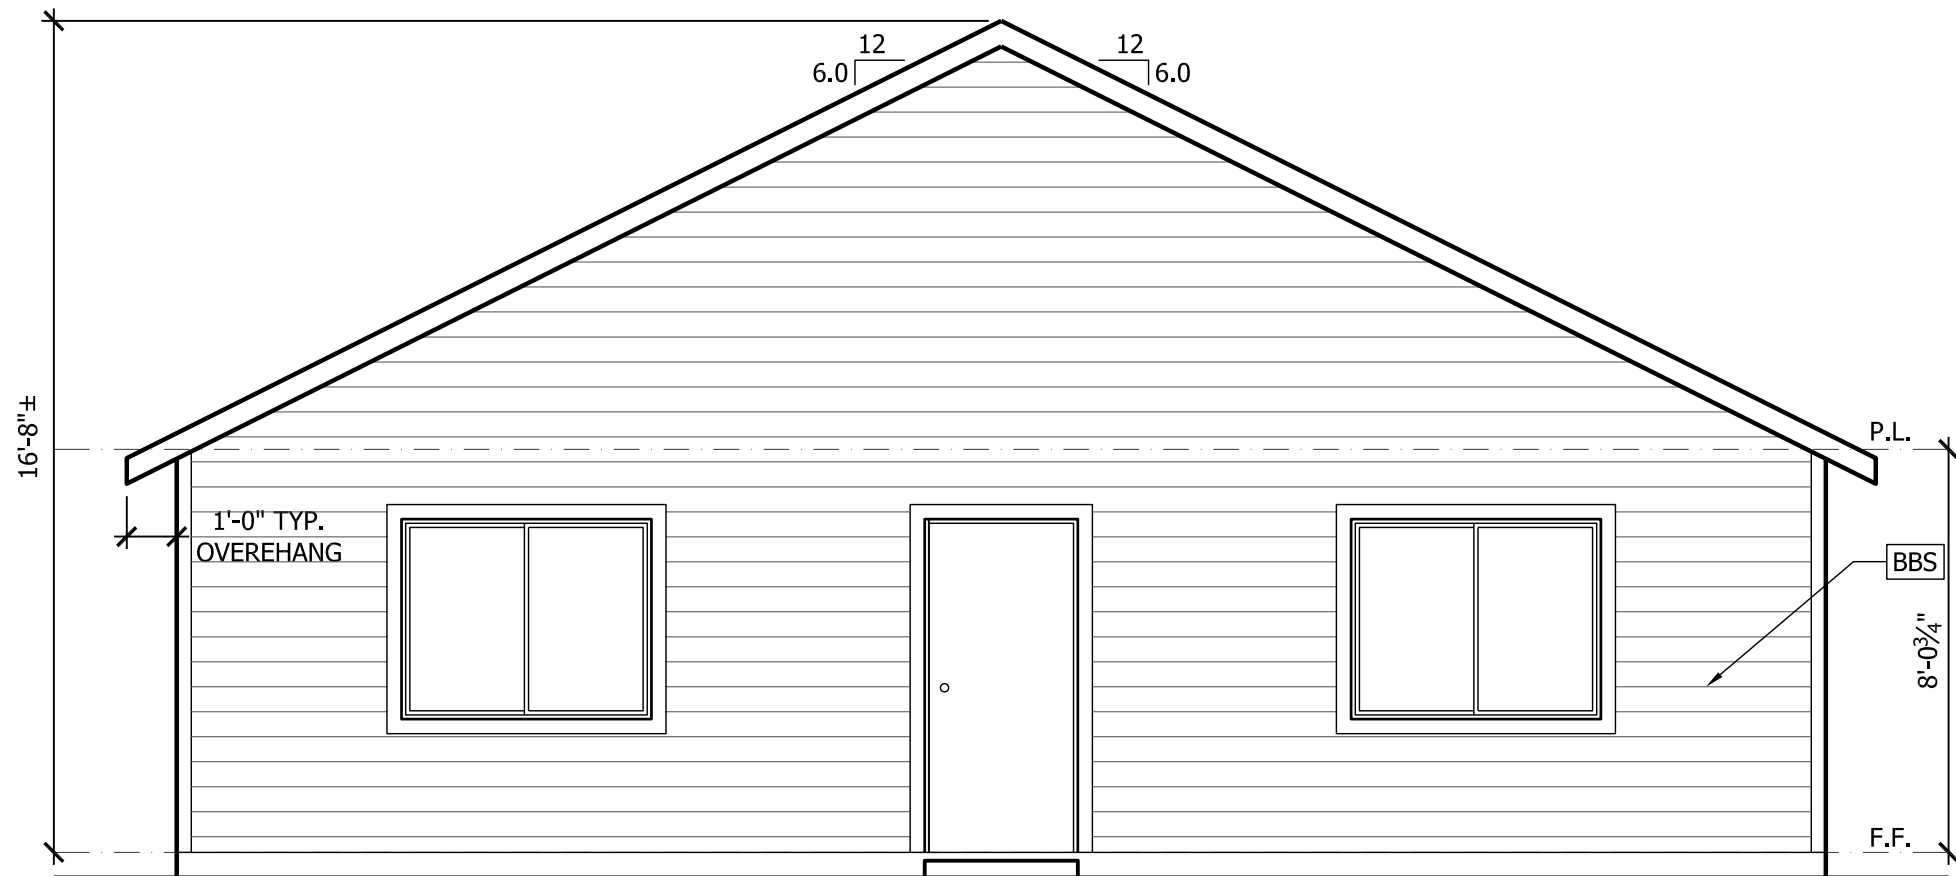

A FRONT ELEVATION
2 1/4" = 1'-0"

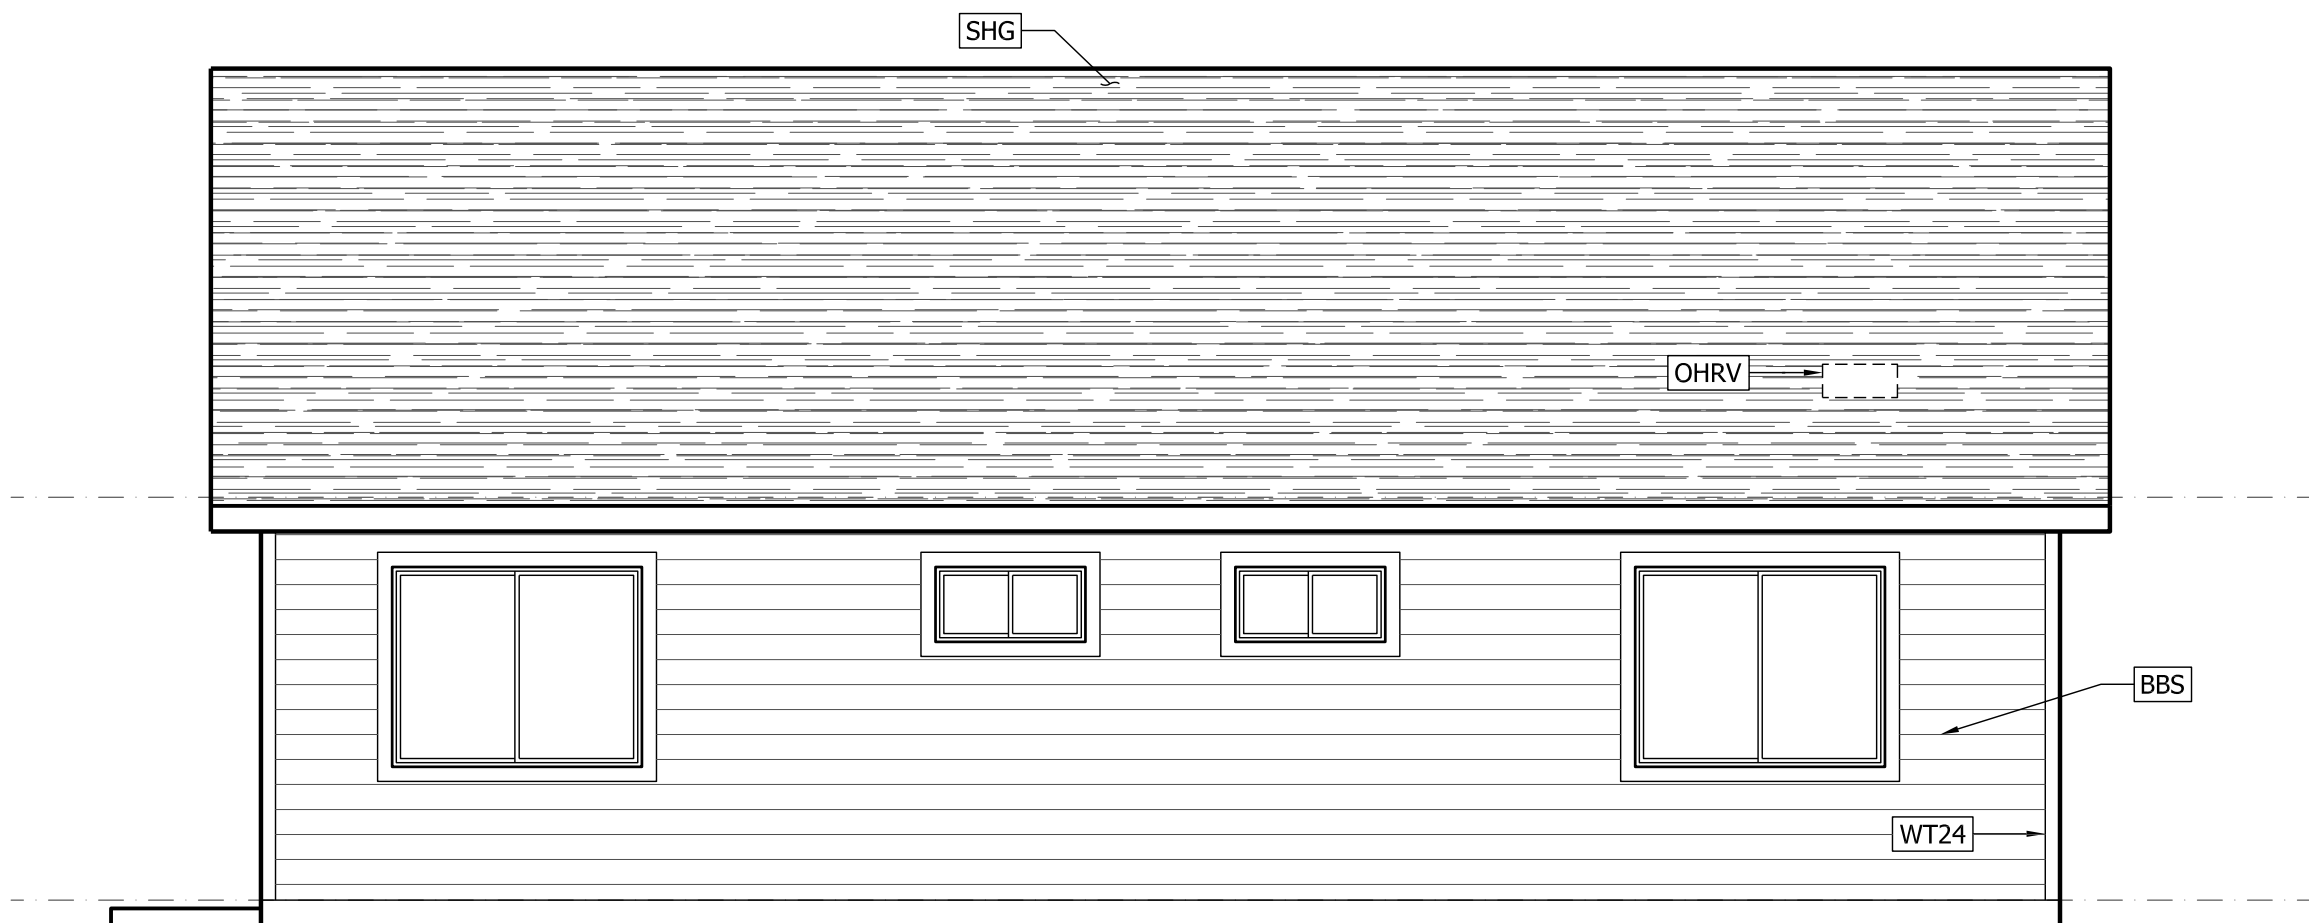

D RIGHT ELEVATION
2 1/4" = 1'-0"

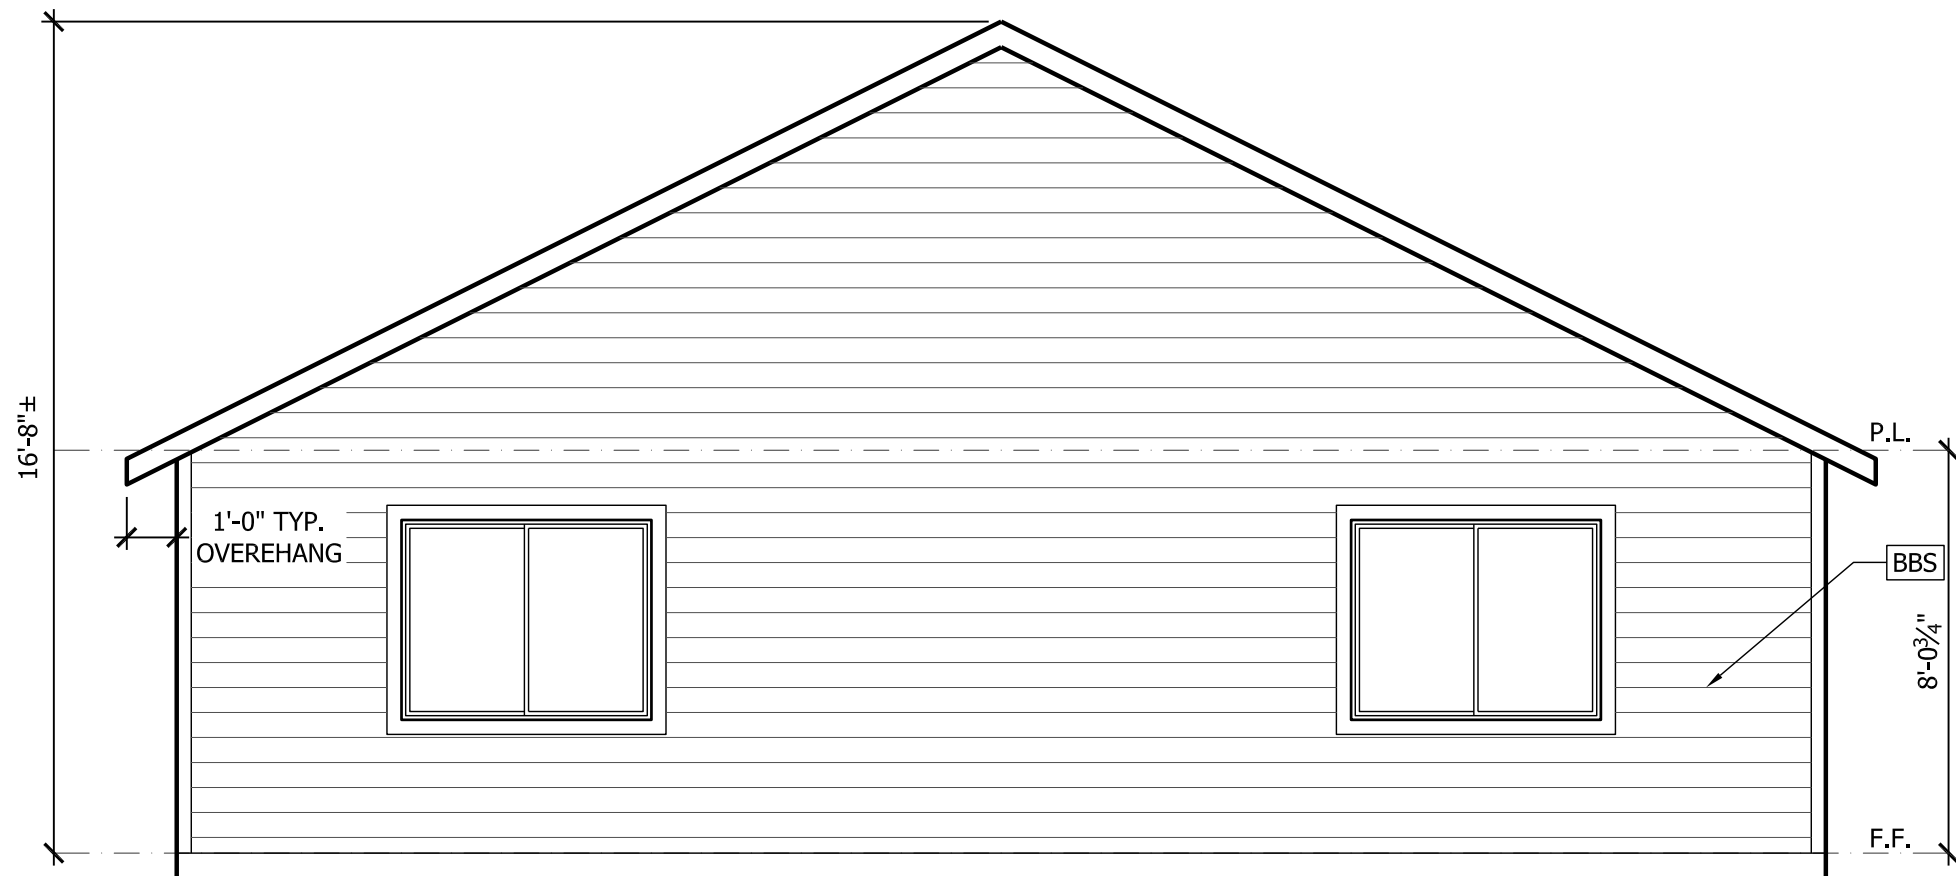

B REAR ELEVATION
2 1/4" = 1'-0"