

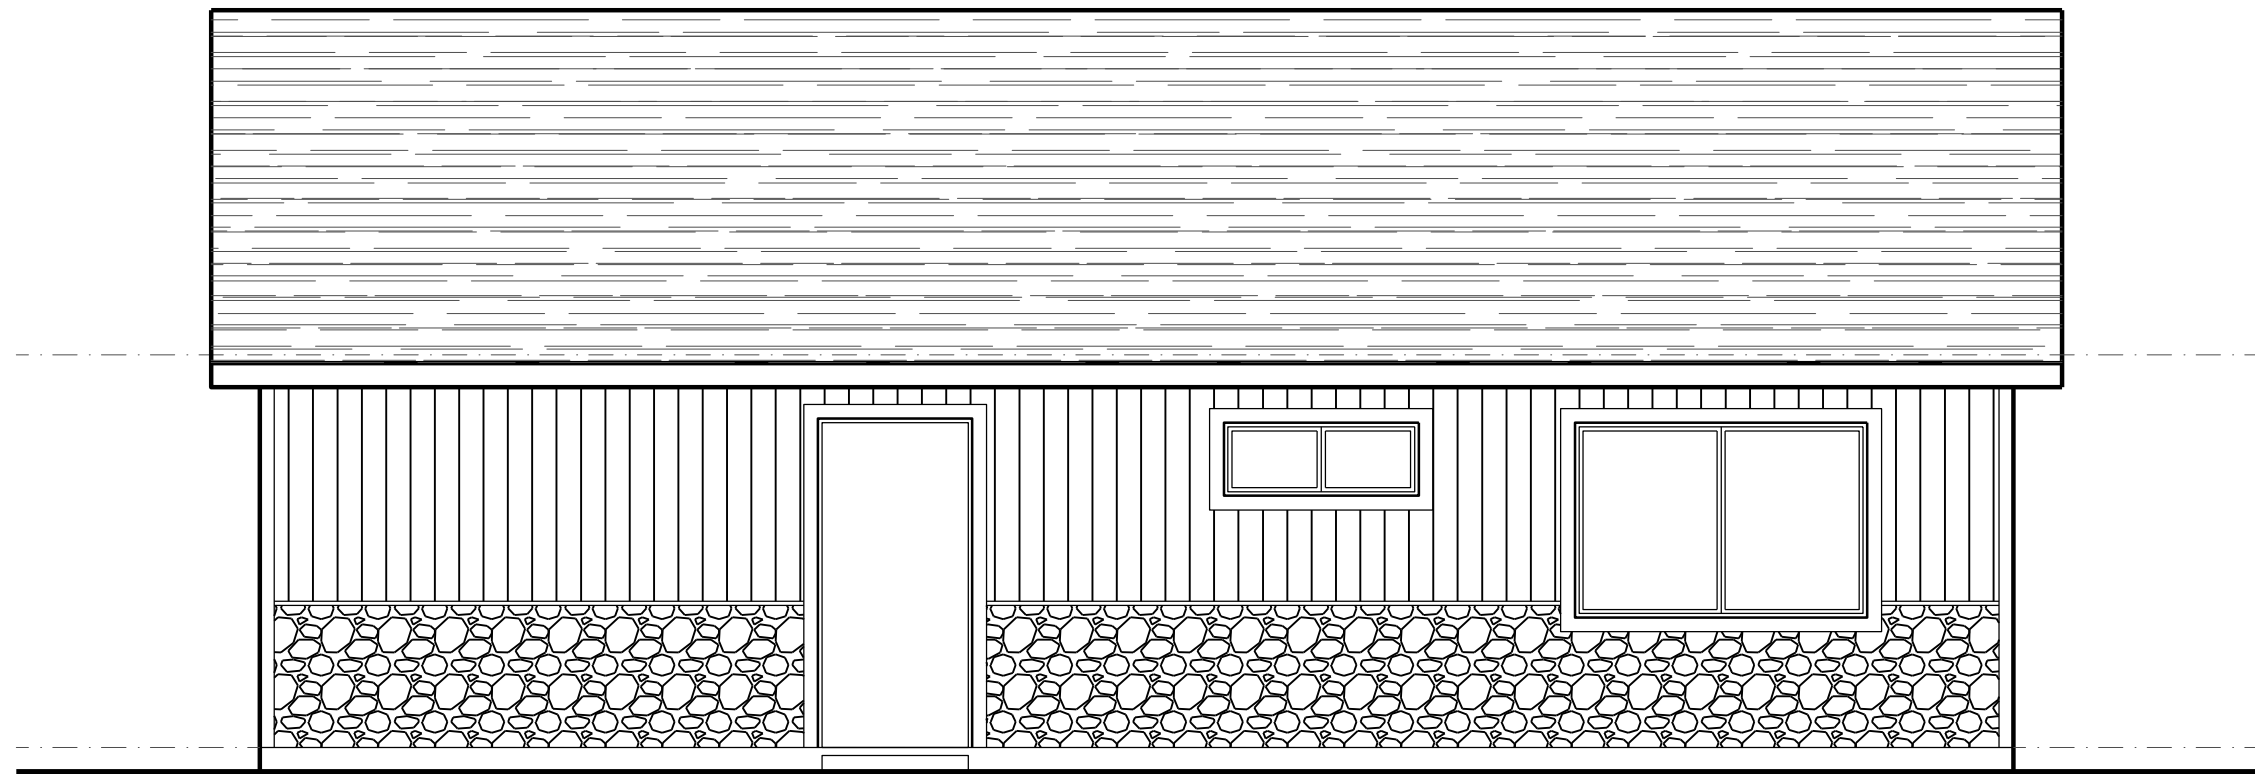
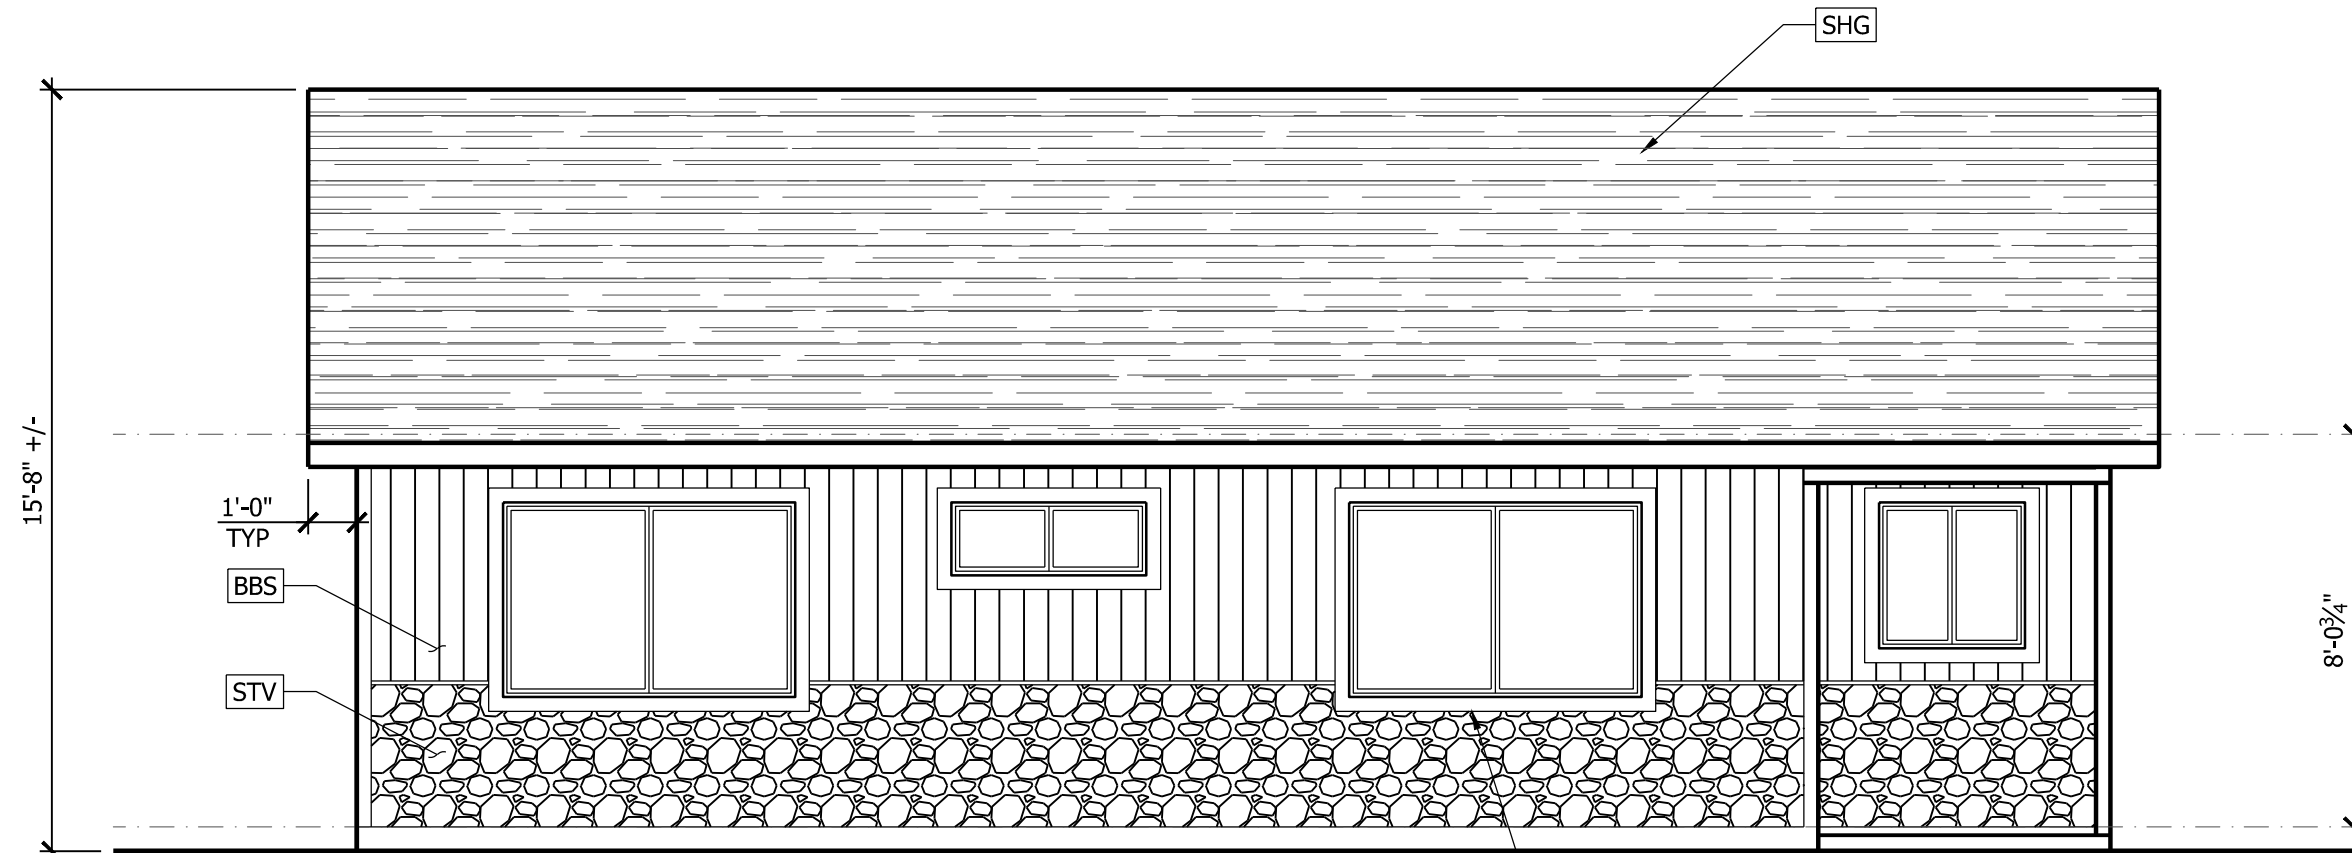
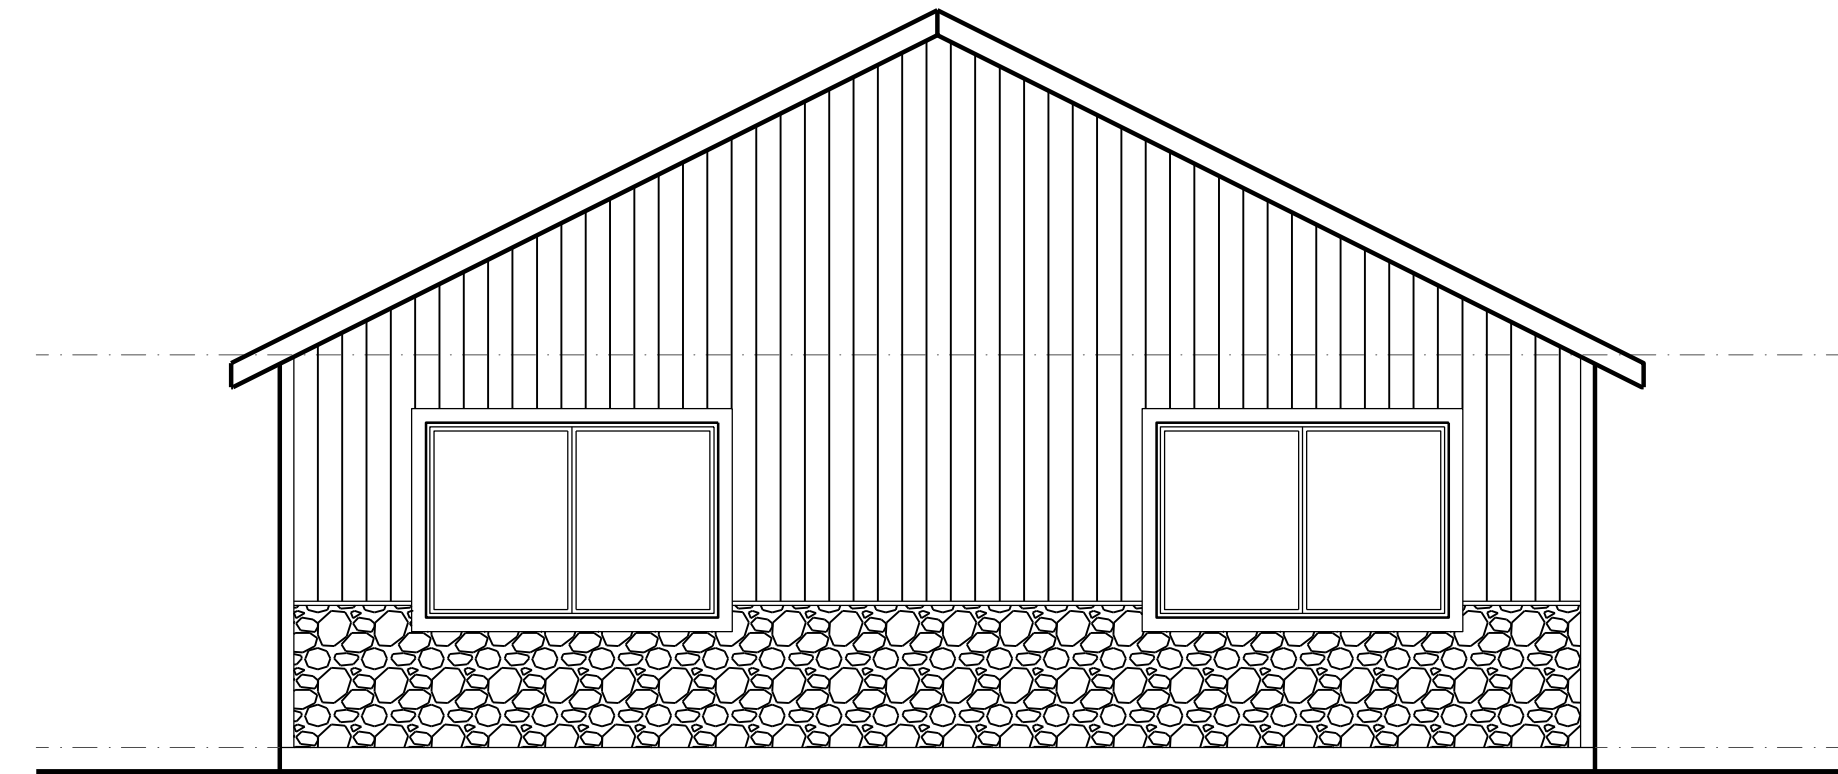


REFERENCE KEYNOTES	
DIVISION 03 - CONCRETE	
CW	- CONCRETE WALK
DIVISION 04 - MASONRY	
STV	- STONE VENEER, TYP
DIVISION 06 - WOOD AND PLASTICS	
CASEWORK -	
LIN	- FULL HEIGHT BUILT IN CABINET
MISCELLANEOUS -	
WT24	- 2x4 WOOD TRIM
DIVISION 07 - THERMAL AND MOISTURE PROTECTION	
ROOFING AND SIDING -	
SHG	- CLASS 'A' LIFETIME COMPOSITION ROOF SHINGLES o/ 15LB FELT COMPLIANT WITH TABLE R905.1(1). FASTEN ROOFING WITH CORROSION RESISTANT FASTENERS CRC R905.2.5
DIVISION 09 - FINISHES	
BBS	- 5/8" T1-11 BOARD AND BATTEN SIDING o/ TWO LAYER GRADE 'D' PAPER OR 1 LAYER TYVEK, NAILING PER STRUCTURAL
FLOORING -	
LAM	- LAMINATE FLOORING
DIVISION 11 - EQUIPMENT	
DW18	- 18" DISHWASHER
FR30	- FRIDGE, 30" WIDE
REH	- RANGE EXHAUST HOOD/ MICROWAVE, VENTED
RG30-E	- 30" RANGE - ELECTRIC
WD	- STACKED WASHER AND DRYER, PROVIDE MIN 2" STANDPIPE
DIVISION 12 - FURNISHINGS	
BC24	- 24" DEEP BASE CABINET
UC12	- 12" DEEP UPPER CABINET
UC24	- 24" DEEP UPPER CABINET
DIVISION 13 - SPECIAL CONSTRUCTION	
PS	- CLOSET POLE & SHELF
DIVISION 17 - PLUMBING	
BC-S	- BATHTUB SHOWER COMBO
KS-U	- UNDERMOUNT KITCHEN SINK
SK60	- SINK w/VANITY 60"
WC	- WATER CLOSET, MINIMUM 30" CLEAR WIDTH CENTERED ON WATER CLOSET & 24" CLEAR SPACE OFF NOSE OF WATER CLOSET.

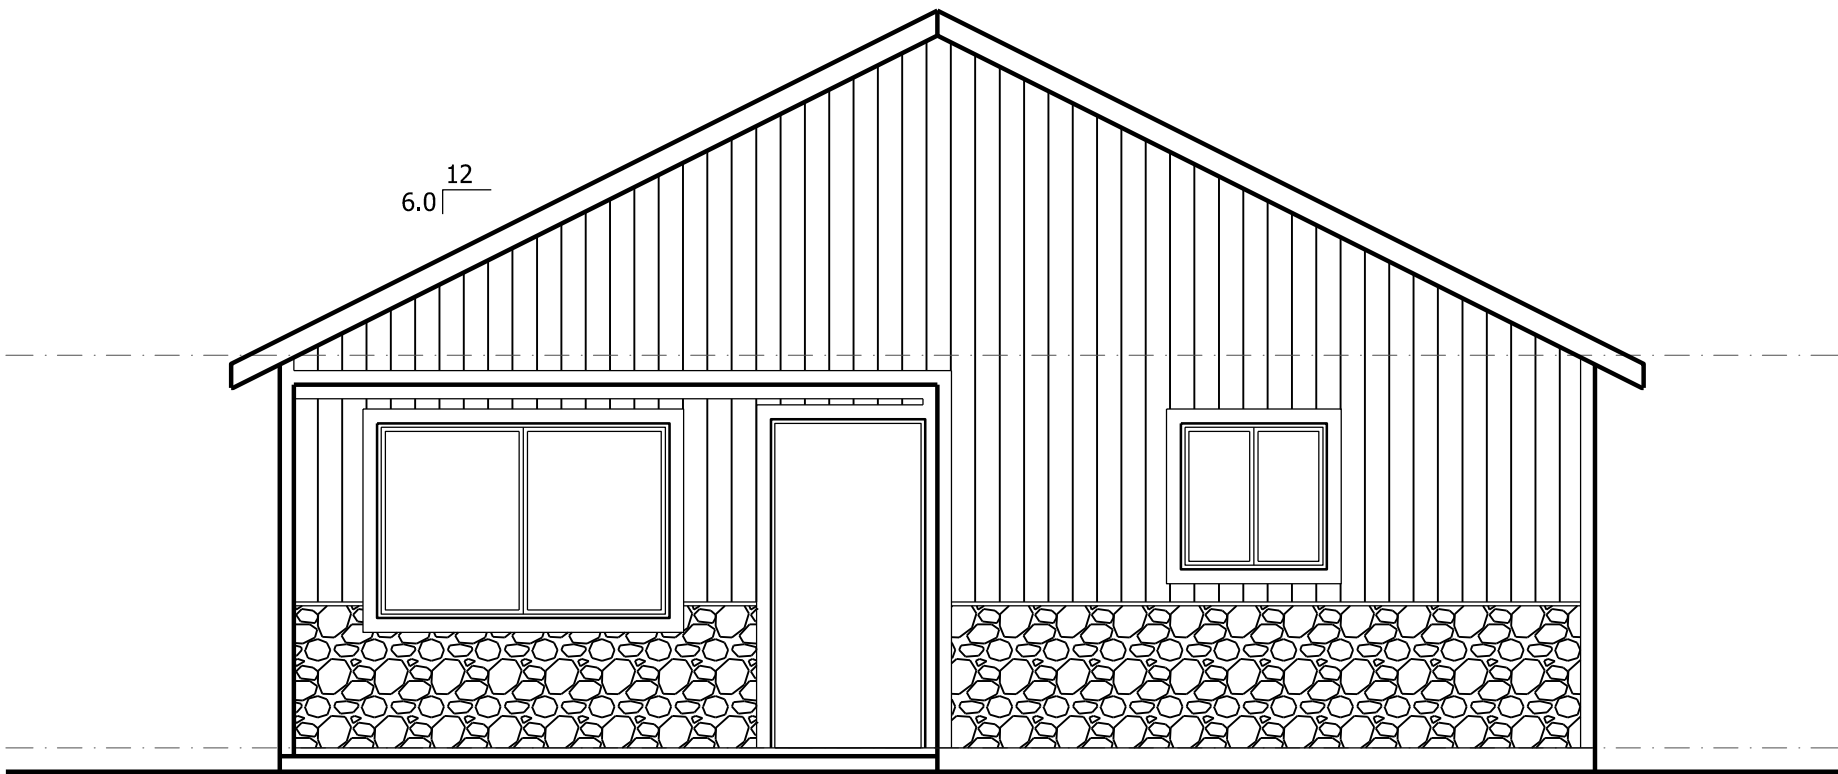

WINDOW SCHEDULE								
NUMBER	SIZE		STYLE	HEAD HEIGHT	FIRE RATING	SHCG	U-FACTOR	NOTES
	WIDTH	HEIGHT						
1	6'-0"	4'-0"	SLIDER	6'-8"	?	.23	.30	—
2	4'-0"	1'-6"	SLIDER	6'-8"	?	.23	.30	EGRESS
3	6'-0"	4'-0"	SLIDER	6'-8"	?	.23	.30	—
4	6'-0"	4'-0"	SLIDER	6'-8"	?	.23	.30	—
5	6'-0"	4'-0"	SLIDER	6'-8"	?	.23	.30	—
6	6'-0"	4'-0"	SLIDER	6'-8"	?	.23	.30	—
7	4'-0"	1'-6"	SLIDER	6'-8"	?	.23	.30	EGRESS
8	3'-0"	3'-0"	SLIDER	6'-8"	?	.23	.30	—
9	3'-0"	3'-0"	SLIDER	6'-8"	?	.23	.30	—
11	6'-0"	4'-0"	SLIDER	6'-8"	?	.23	.30	—

DOOR AND FRAME SCHEDULE				
NUMBER	SIZE	STYLE	FIRE RATING	NOTES
1	3'-0" x 6'-8" x 1-3/4"	SINGLE - EXTERIOR	--	--
2	2'-6" x 6'-8" x 1-3/4"	SINGLE - INTERIOR	--	--
3	2'-6" x 6'-8" x 1-3/4"	SINGLE - INTERIOR	--	--
4	PR 2'-6" x 6'-8" x 1-3/4"	HORIZONTAL BYPASS	--	--
5	2'-6" x 6'-8" x 1-3/4"	SINGLE - INTERIOR	--	--
6	PR 2'-6" x 6'-8" x 1-3/4"	HORIZONTAL BYPASS	--	--
7	2'-6" x 6'-8" x 1-3/4"	SINGLE - INTERIOR	--	--
8	PR 1'-6" x 6'-8" x 1-3/4"	BIFOLD	--	--
9	3'-0" x 6'-8" x 1-3/4"	SINGLE - EXTERIOR	--	--
10	3'-6" x 6'-8" x 0"	GYPSUM OPENING	--	--

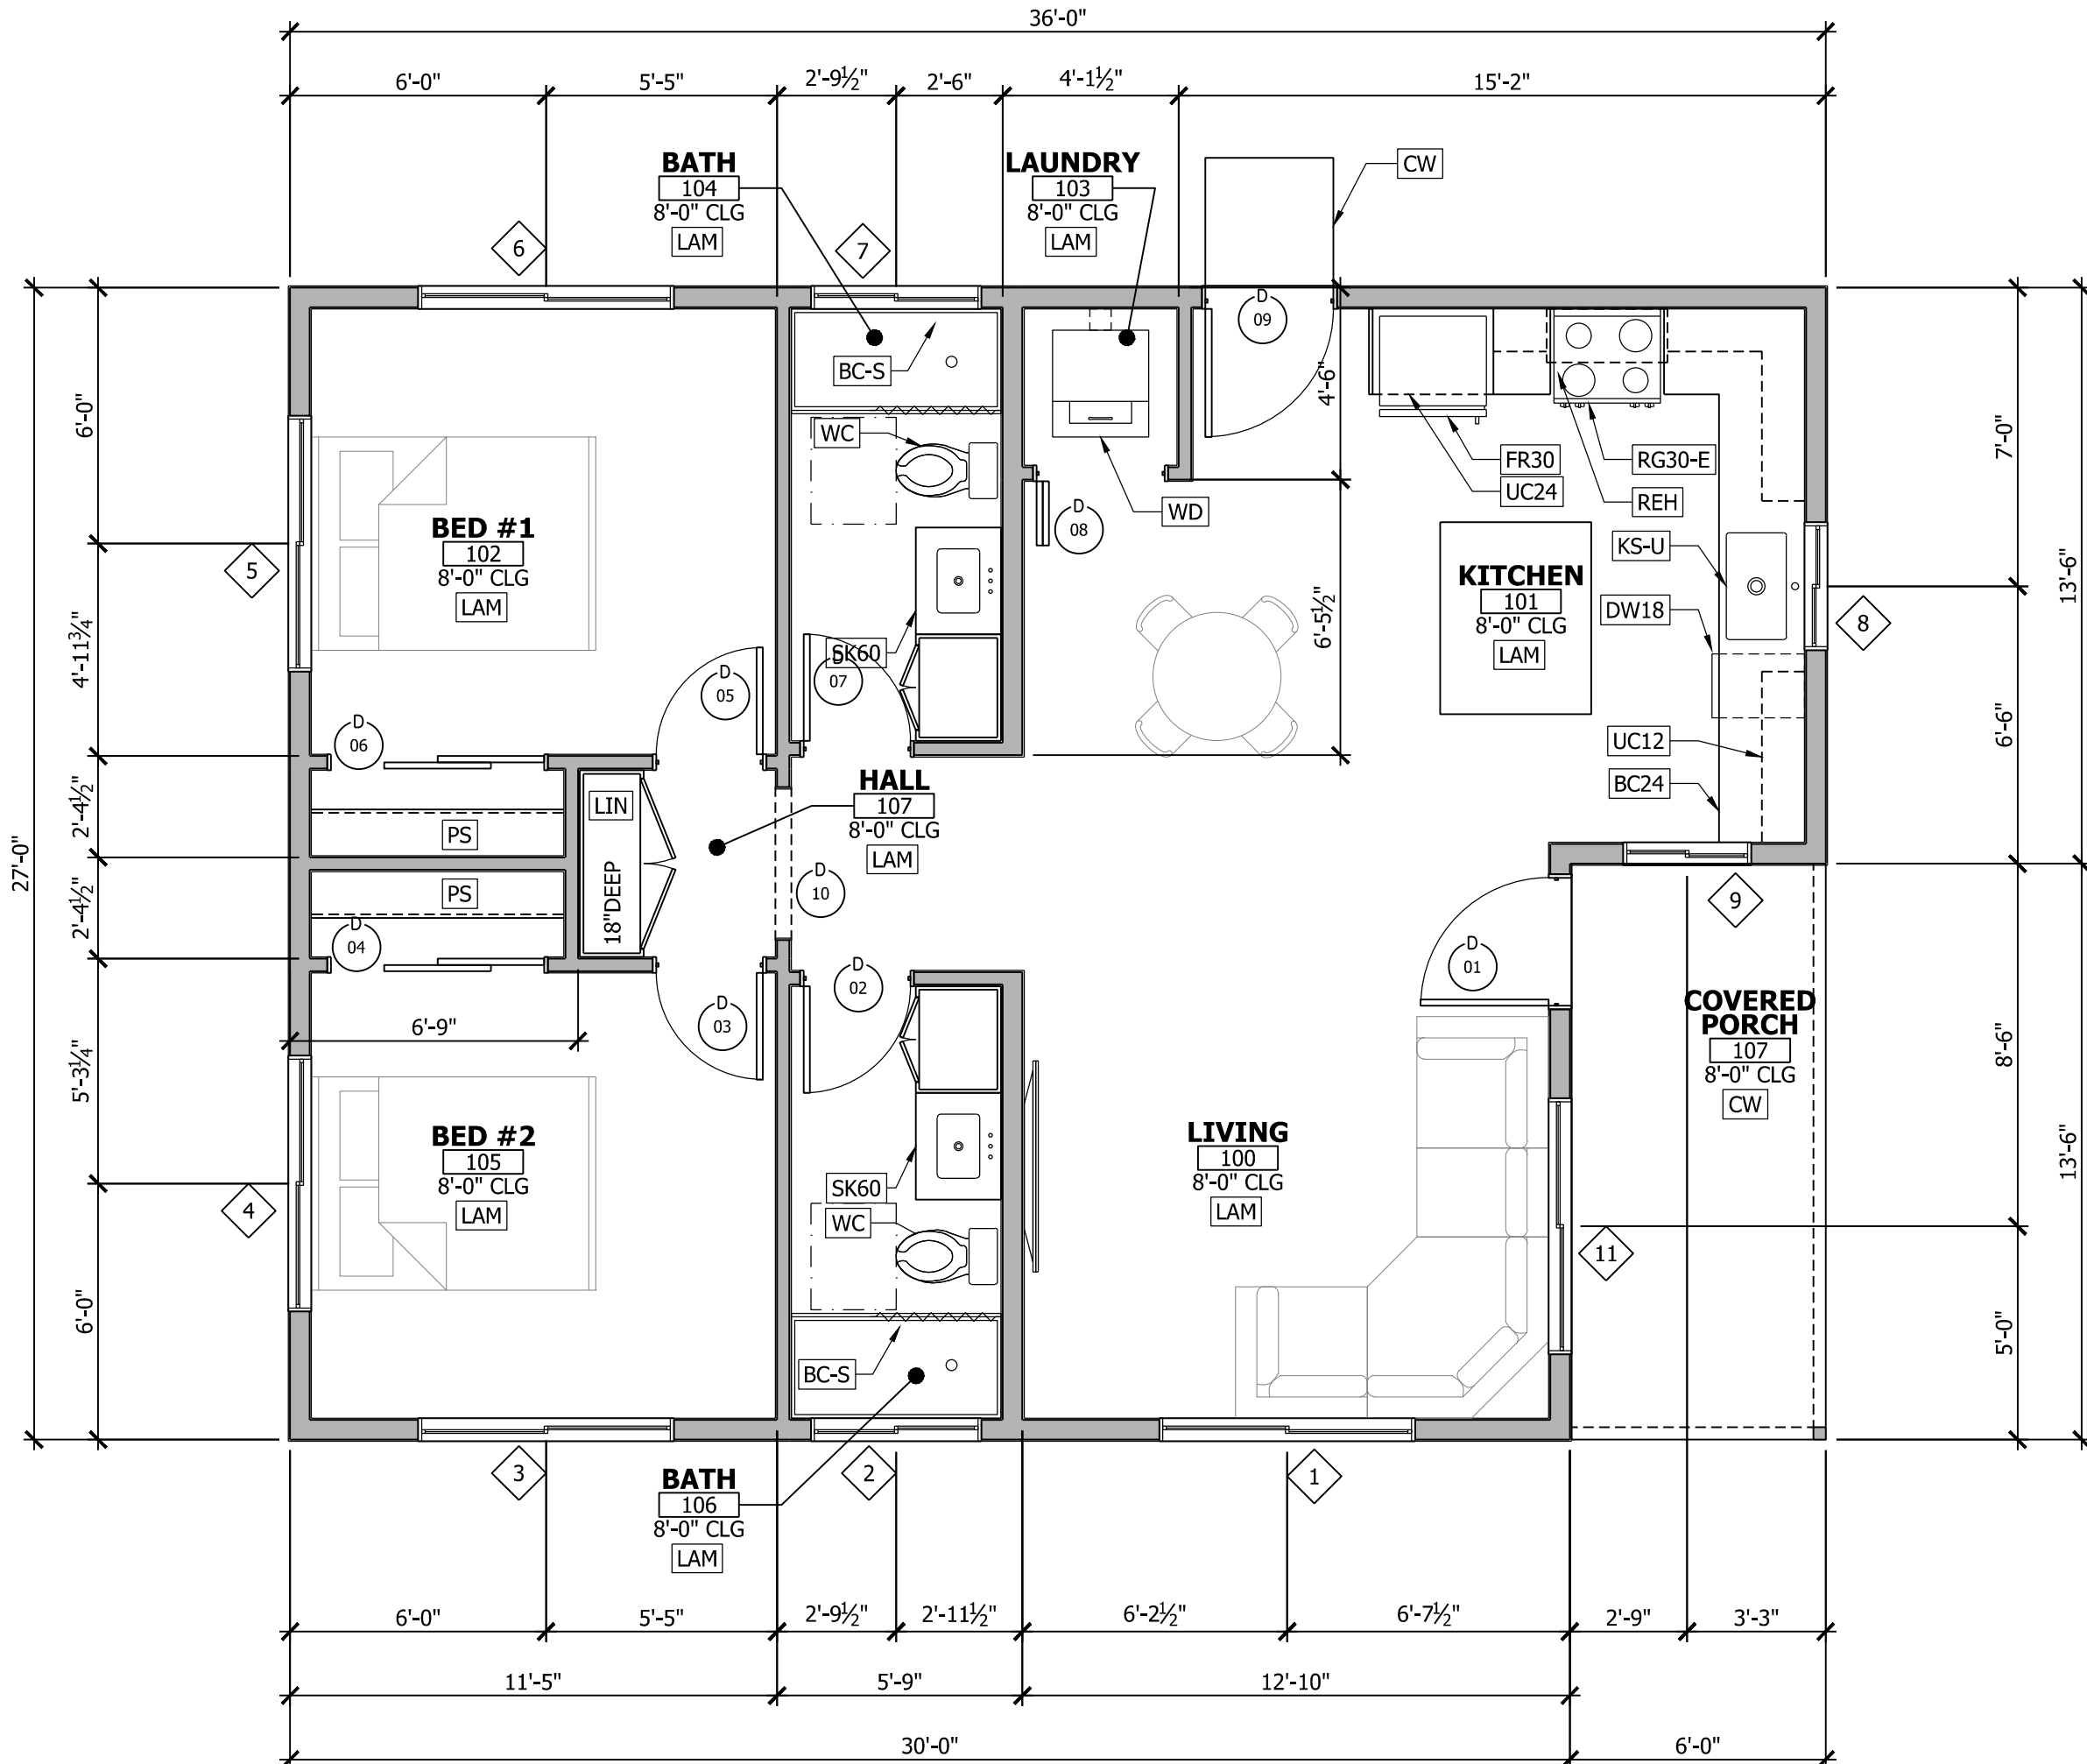

1 FLOOR PLAN

1/4" = 1'-0"

0 1' 2' 3' 4' 5' 10'

891 SF LIVING
81 SF COVERED PORCH