




REFERENCE KEYNOTES	
DIVISION 03 - CONCRETE	
CL	- 4" THICK CONCRETE LANDING, MINIMUM 3'-0" DEEP x DOOR WIDTH. LANDING SHALL NOT EXCEED 1/4 UNIT VERTICAL IN 12 UNITS HORIZONTAL (2%)
DIVISION 04 - MASONRY	
BW1	- BRICK WALL, COLOR No. 1
STV	- STONE VENEER, TYP
STVC	- STONE VENEER CAP
DIVISION 06 - WOOD AND PLASTICS	
1HR	- 1 HOUR FIRE RATED WALL TO UNDERSIDE OF ROOF SHEATHING PER R302.1 (1), EAVES REDUCED TO 0 HRS UNDER R302.1 (1) SUBNOTE (a), USE PRESCRIPTIVE 1-HOUR ASSEMBLY PER R337.7.4
DIVISION 07 - THERMAL AND MOISTURE PROTECTION	
ROOFING AND SIDING -	
TRS	- TILE ROOF SYSTEM
DIVISION 09 - FINISHES	
2X4	- 2X4 TRIM
CMS	- CORRUGATED METAL SIDING
CEMENT PLASTER -	
CPS1	- 3 COAT STUCCO w/ SMOOTH FINISH, TYP
FLOORING -	
LVF	- LUXURY VINYL FLOORING
DIVISION 11 - EQUIPMENT	
DW18	- 18" DISHWASHER
FR30	- FRIDGE, 30" WIDE
MWEH	- MICROWAVE EXHAUST HOOD COMBINATION, MIN VENTILATION RATE OF 100 CFM (CMC TABLE 403.7), HVI RATED & LIMITED TO 3 SONES, HERS VERIFICATION REQUIRED
RG30-E	- 30" RANGE - ELECTRIC
WD	- STACKED WASHER AND DRYER, PROVIDE MIN 2" STANDPIPE
DIVISION 12 - FURNISHINGS	
BC24	- 24" DEEP BASE CABINET
UC12	- 12" DEEP UPPER CABINET
UC24	- 24" DEEP UPPER CABINET
DIVISION 15 - MECHANICAL	
40HPE	- 40 GALLON HYBRID HEAT PUMP ELECTRIC HOT WATER HEATER, DRAIN TO EXTERIOR
MSH	- MINI SPLIT HEAD
MSU	- MINI SPLIT OUTDOOR UNIT, INSTALLED PER MANUFACTURER SPECIFICATIONS
DIVISION 17 - PLUMBING	
SK30	- SINK w/VANITY 30"
SK-U30	- UNDERMOUNT SINK 30"
TS33-CGD	- TILE SHOWER 3x3, CORNER W/GLASS
WC	- WATER CLOSET, MINIMUM 30" CLEAR WIDTH CENTERED ON WATER CLOSET & 24" CLEAR SPACE OFF NOSE OF WATER CLOSET.

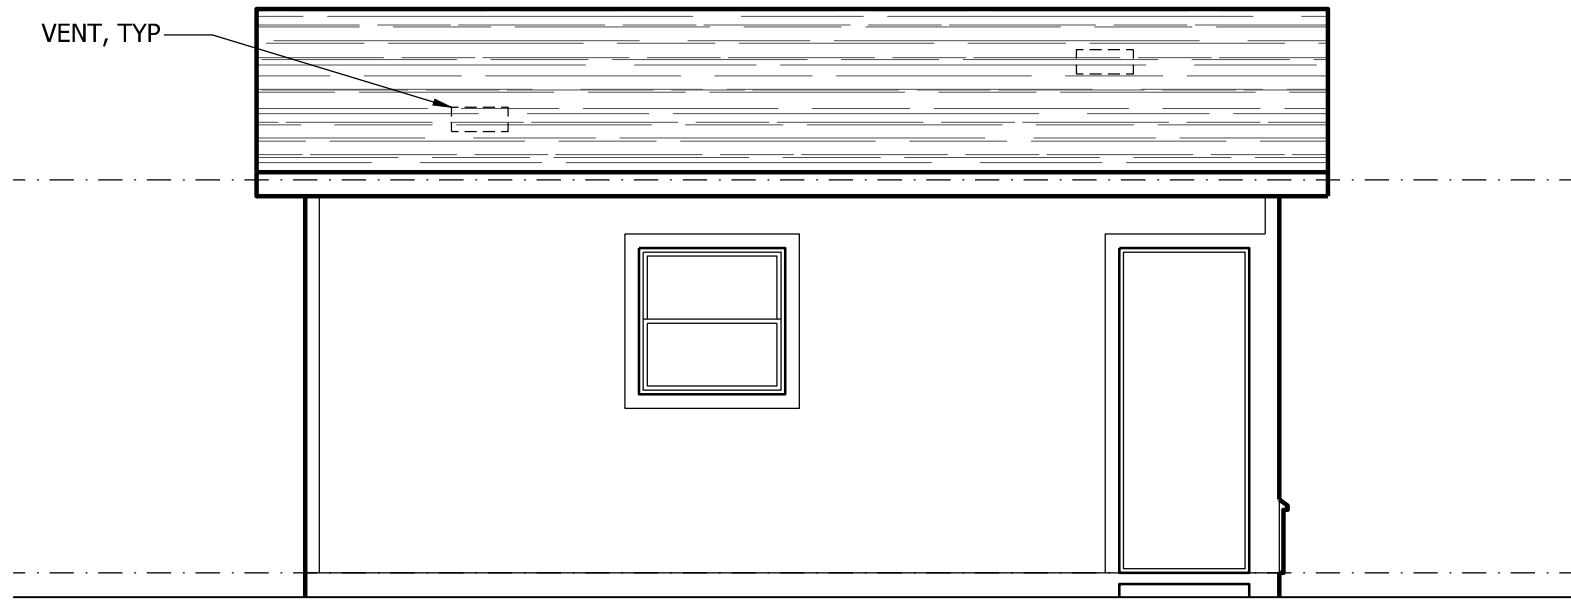


C REAR ELEVATION
1 1/4" = 1'-0"

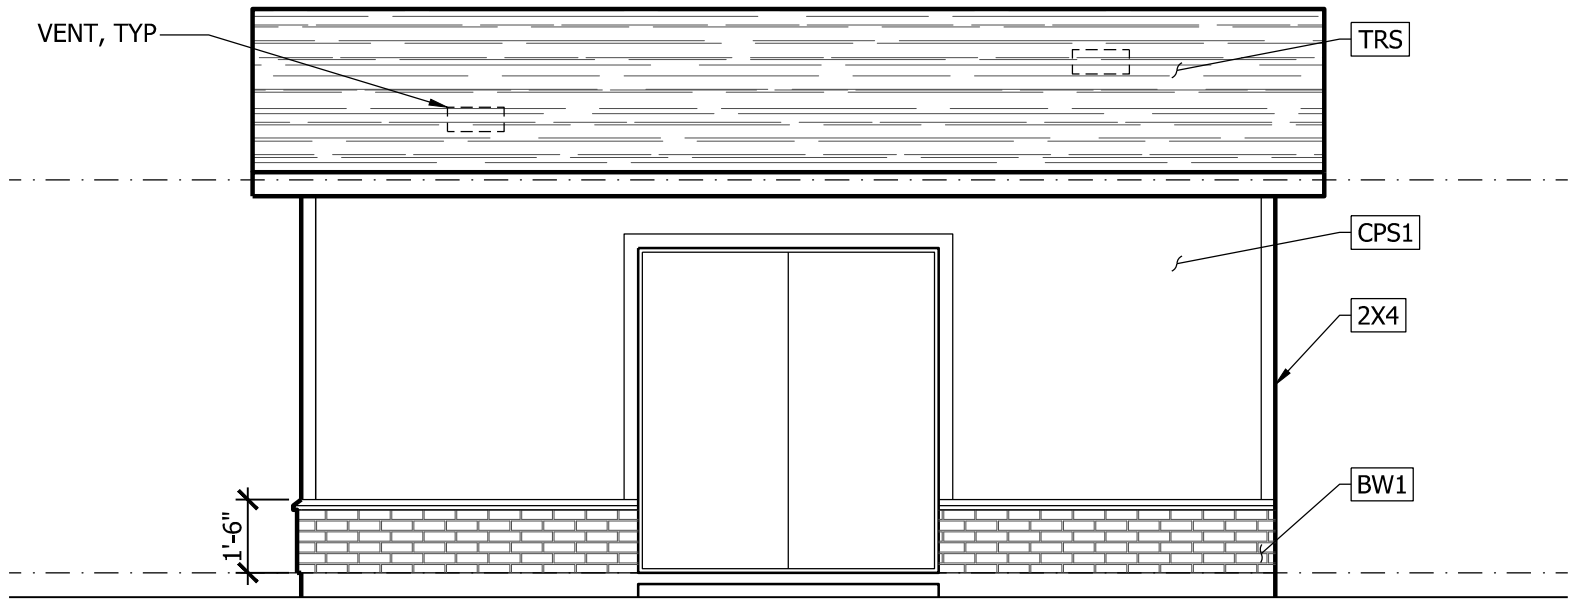


A FRONT ELEVATION
1 1/4" = 1'-0"

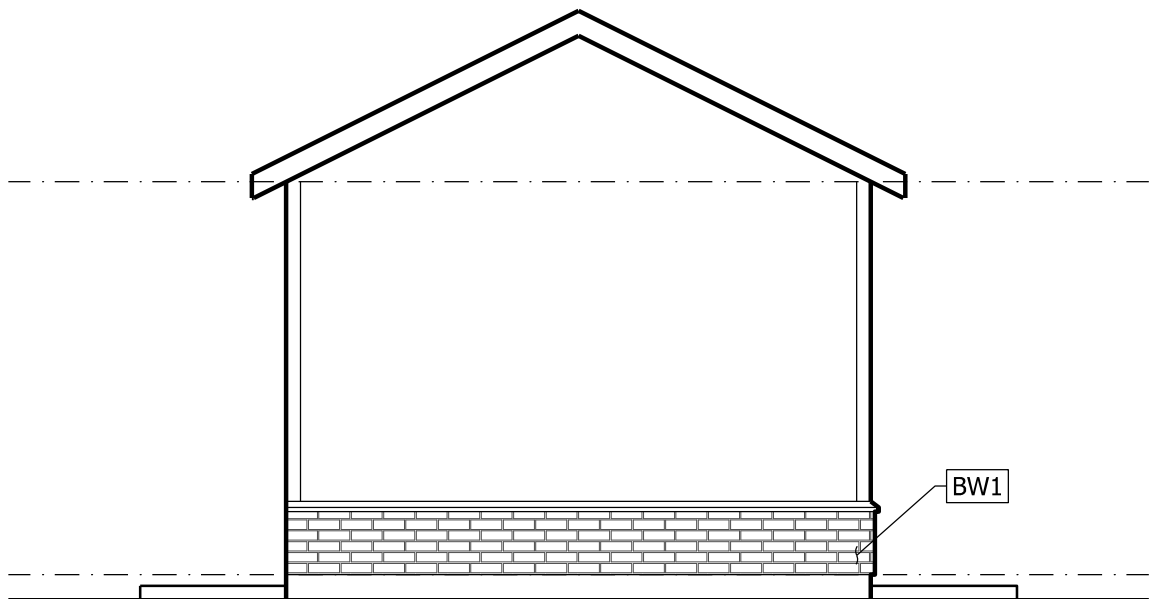


D LEFT ELEVATION
1 1/4" = 1'-0"

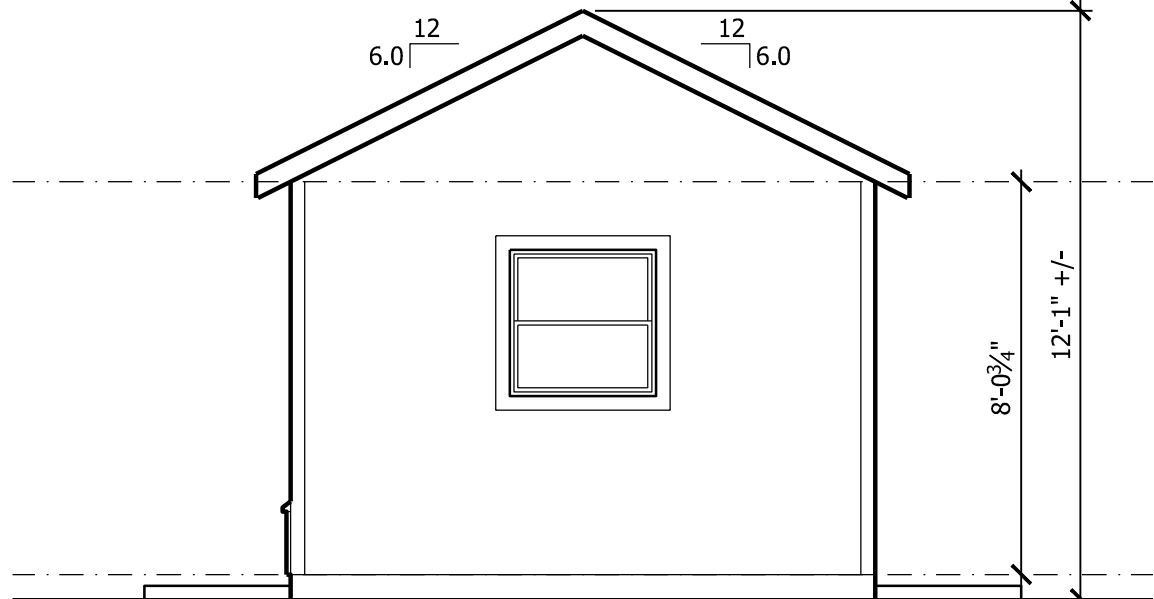


B RIGHT ELEVATION
1 1/4" = 1'-0"

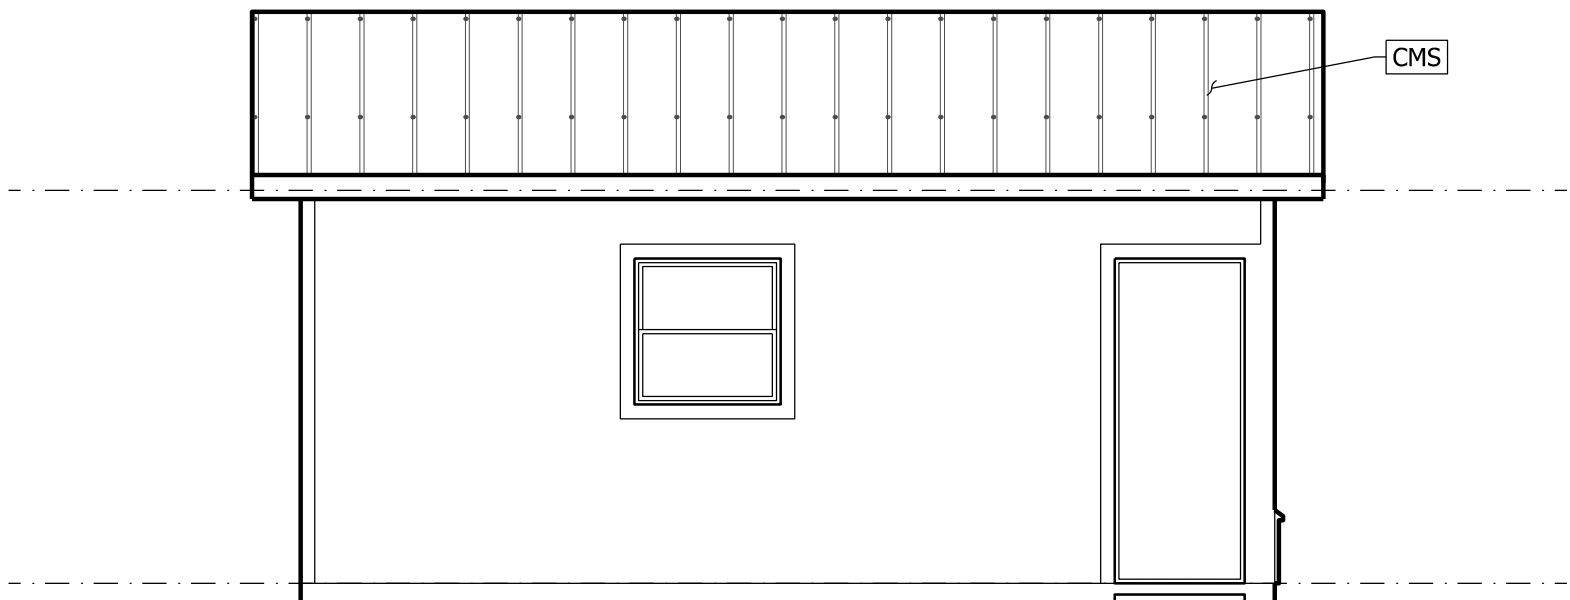


C2 REAR ELEVATION
1 1/4" = 1'-0"

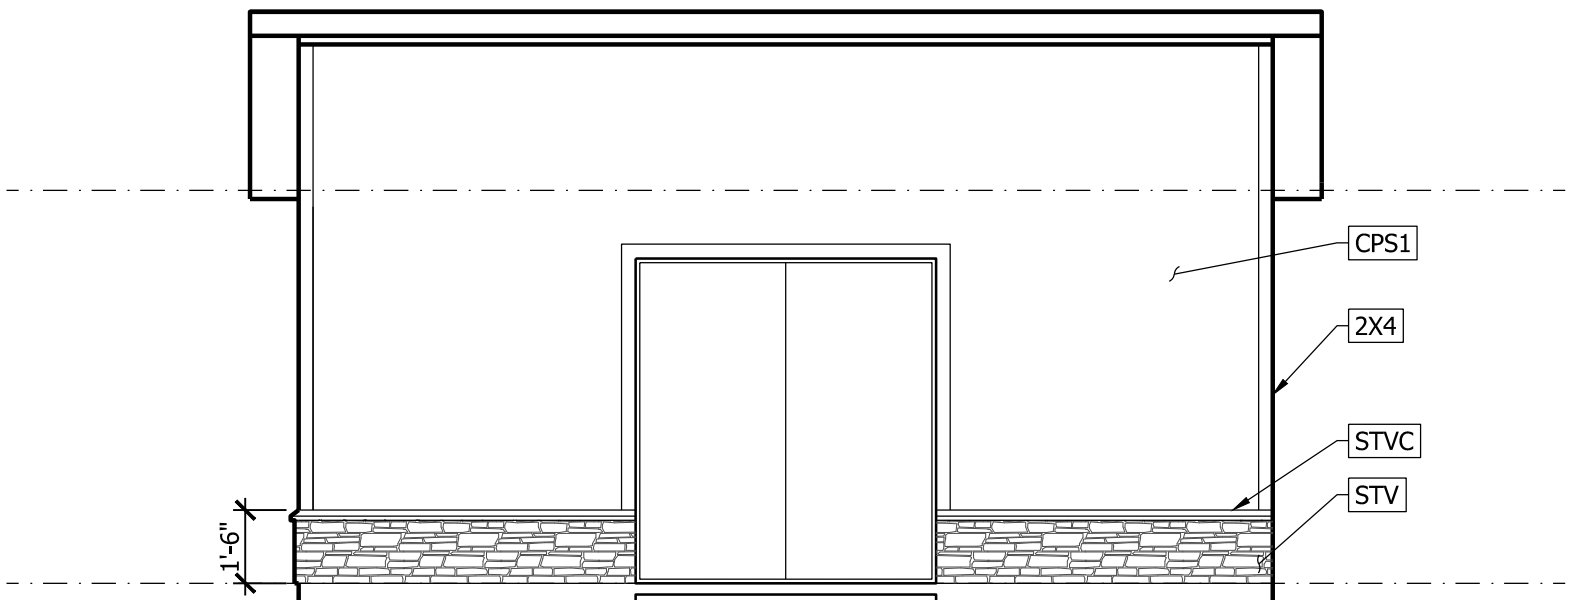

A2 FRONT ELEVATION
1 1/4" = 1'-0"

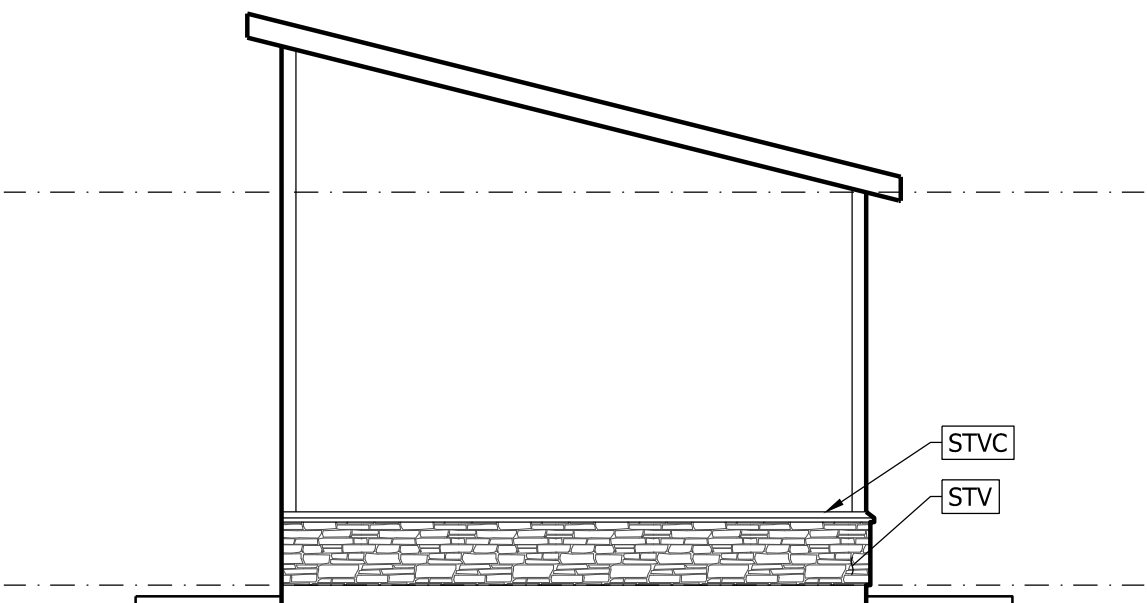

D2 LEFT ELEVATION
1 1/4" = 1'-0"

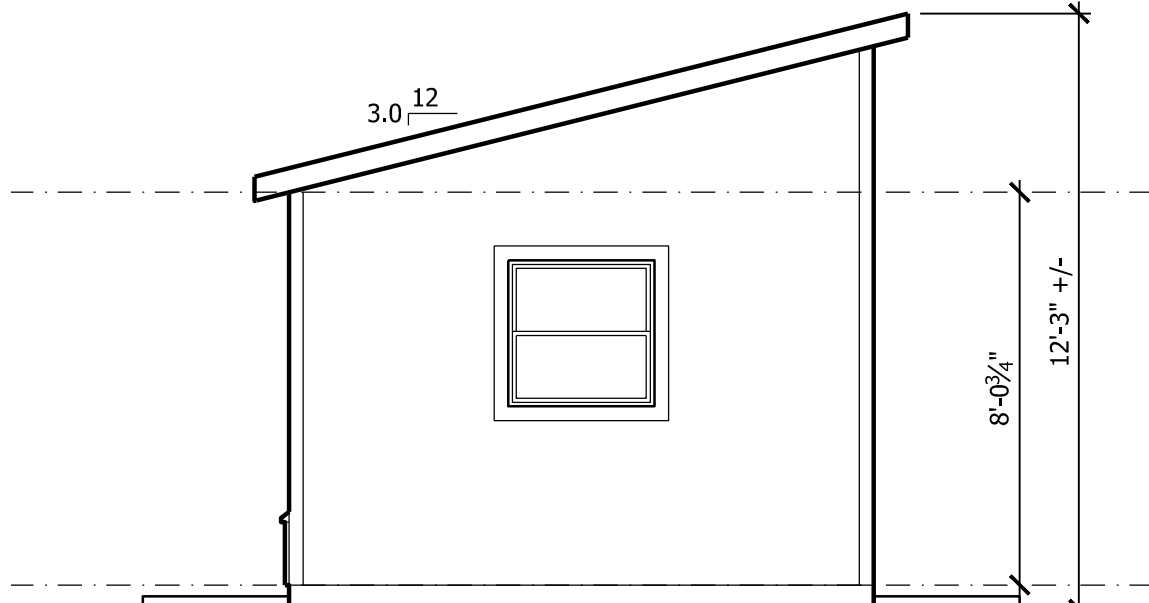

B2 RIGHT ELEVATION
1 1/4" = 1'-0"

WINDOW SCHEDULE							
NUMBER	SIZE		STYLE	HEAD HEIGHT	SHCG	U-FACTOR	NOTES
	WIDTH	HEIGHT					
1	3'-0"	3'-0"	SINGLE HUNG	6'-8"	.23	.30	
2	3'-0"	3'-0"	SINGLE HUNG	6'-8"	.23	.30	

DOOR AND FRAME SCHEDULE				
NUMBER	SIZE	STYLE	FIRE RATING	NOTES
1	PR 3'-0" x 6'-8" x 1-3/4"	DOUBLE - EXTERIOR	--	--
2	2'-6" x 6'-8" x 1-3/4"	SINGLE - INTERIOR	--	--
3	2'-6" x 6'-8" x 1-3/4"	SINGLE - INTERIOR	--	LOUVERED 100 SQ IN MIN

