



REFERENCE KEYNOTES		
DIVISION 03 - CONCRETE		
CL	-	4" THICK CONCRETE LANDING, MINIMUM 3'-0" DEEP x DOOR WIDTH. LANDING SHALL NOT EXCEED 1/4 UNIT VERTICAL IN 12 UNITS HORIZONTAL (2%)
CW	-	CONCRETE WALK
DIVISION 06 - WOOD AND PLASTICS		
MISCELLANEOUS -		
WT24	-	2x4 WOOD TRIM
DIVISION 07 - THERMAL AND MOISTURE PROTECTION		
ROOF ACCESSORIES -		
AA	-	22"x30" ATTIC ACCESS, PERMANTLY ATTACH INSULATION USING ADHESIVE OR MECHANICAL FASTENERS TO ACCESS PANEL. ACCESS SHALL BE GASKETED TO PREVENT AIR LEAKAGE
ROOFING AND SIDING -		
SHG	-	CLASS 'A' LIFETIME COMPOSITION ROOF SHINGLES o/ 15LB FELT COMPLIANT WITH TABLE R905.1(1). FASTEN ROOFING WITH CORROSION RESISTANT FASTENERS CRC R905.2.5
DIVISION 09 - FINISHES		
BBS	-	5/8" T1-11 BOARD AND BATTEN SIDING o/ TWO LAYER GRADE 'D' PAPER OR 1 LAYER TYVEK. NAILING PER STRUCTURAL
FLOORING -		
LAM	-	LAMINATE FLOORING
DIVISION 10 - SPECIALTIES		
HS12	-	HIGH SHELF, 12" DEEP
DIVISION 11 - EQUIPMENT		
DW18	-	18" DISHWASHER
FR30	-	FRIDGE, 30" WIDE
MWEH	-	MICROWAVE EXHAUST HOOD COMBINATION, MIN VENTILATION RATE OF 100 CFM (CMC TABLE 403.7), HVI RATED & LIMITED TO 3 SONES, HERS VERIFICATION REQUIRED
RG30-E	-	30" RANGE - ELECTRIC
WD	-	STACKED WASHER AND DRYER, PROVIDE MIN 2" STANDPIPE
DIVISION 12 - FURNISHINGS		
BC24	-	24" DEEP BASE CABINET
UC12	-	12" DEEP UPPER CABINET
UC24	-	24" DEEP UPPER CABINET
DIVISION 13 - SPECIAL CONSTRUCTION		
PS	-	CLOSET POLE & SHELF
S18	-	18" DEEP SHELVES
DIVISION 15 - MECHANICAL		
50HPE	-	50 GALLON HYBRID HEAT PUMP ELECTRIC HOT WATER HEATER
MSH	-	MINI SPLIT HEAD
DIVISION 16 - ELECTRICAL		
EPP	-	ELECTRICAL SUB PANEL, 120/240V 125A, W/ UFER GROUND, PROVIDE 30"x30" WORKING AREA CENTERED IN FRONT OF PANEL
DIVISION 17 - PLUMBING		
KS-U	-	UNDERMOUNT KITCHEN SINK
SK30	-	SINK w/VANITY 30"
TS33	-	TILE SHOWER 3x3, CURB OR FINISHED THRESHOLD SHALL COMPLY WITH CPC 408.5
WC	-	WATER CLOSET, MINIMUM 30" CLEAR WIDTH CENTERED ON WATER CLOSET & 24" CLEAR SPACE OFF NOSE OF WATER CLOSET.

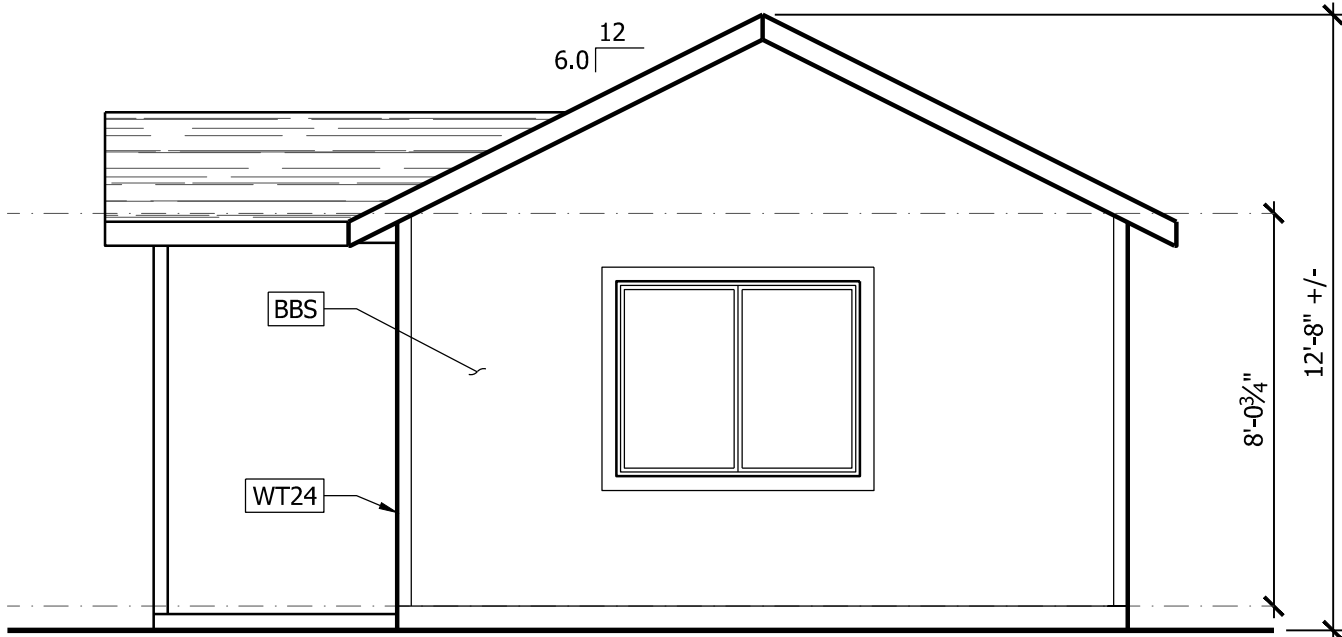


C RIGHT ELEVATION

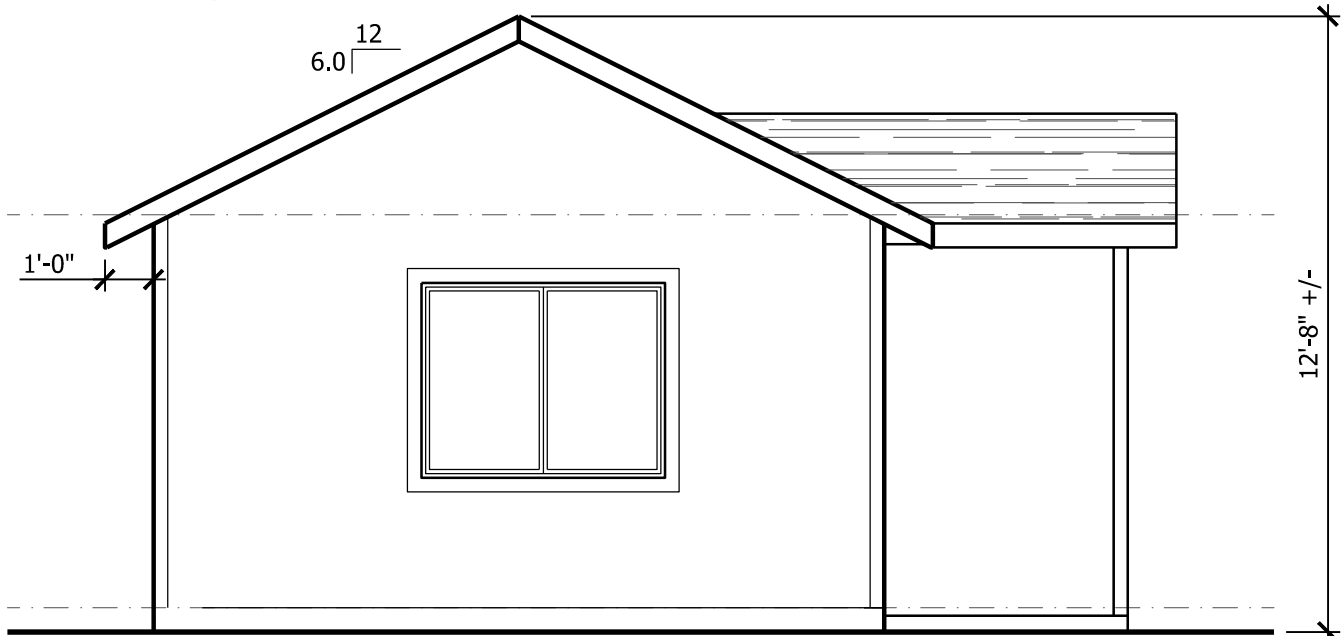

D LEFT ELEVATION




WINDOW SCHEDULE						
NUMBER	SIZE		STYLE	HEAD HEIGHT	SHCG	U-FACTOR
	WIDTH	HEIGHT				
1	5'-0"	4'-0"	SLIDER	6'-8"	.23	.30
2	5'-0"	4'-0"	SLIDER	6'-8"	.23	.30
3	2'-0"	2'-0"	SLIDER	6'-8"	.23	.30
4	5'-0"	4'-0"	SLIDER	6'-8"	.23	.30
5	3'-0"	3'-0"	SLIDER	6'-8"	.23	.30
6	5'-0"	4'-0"	SLIDER	6'-8"	.23	.30
7	5'-0"	4'-0"	SLIDER	6'-8"	.23	.30
8	5'-0"	4'-0"	SLIDER	6'-8"	.23	.30

DOOR AND FRAME SCHEDULE				
NUMBER	SIZE	STYLE	FIRE RATING	NOTES
1	PR 2'-3" x 6'-8" x 1-3/4"	HORIZONTAL BYPASS	--	--
2	2'-6" x 6'-8" x 1-3/4"	SINGLE - INTERIOR	--	--
3	PR 3'-0" x 6'-8" x 1-3/4"	DOUBLE - EXTERIOR	--	TEMP
4	2'-4" x 6'-8" x 1-3/4"	SINGLE - INTERIOR	--	--
5	2'-6" x 6'-8" x 1-3/4"	SINGLE - INTERIOR	--	--
6	PR 2'-3" x 6'-8" x 1-3/4"	HORIZONTAL BYPASS	--	--
7	2'-8" x 6'-8" x 1-3/4"	SINGLE - EXTERIOR	--	--
8	PR 2'-6" x 6'-8" x 1-3/4"	HORIZONTAL BYPASS	--	--

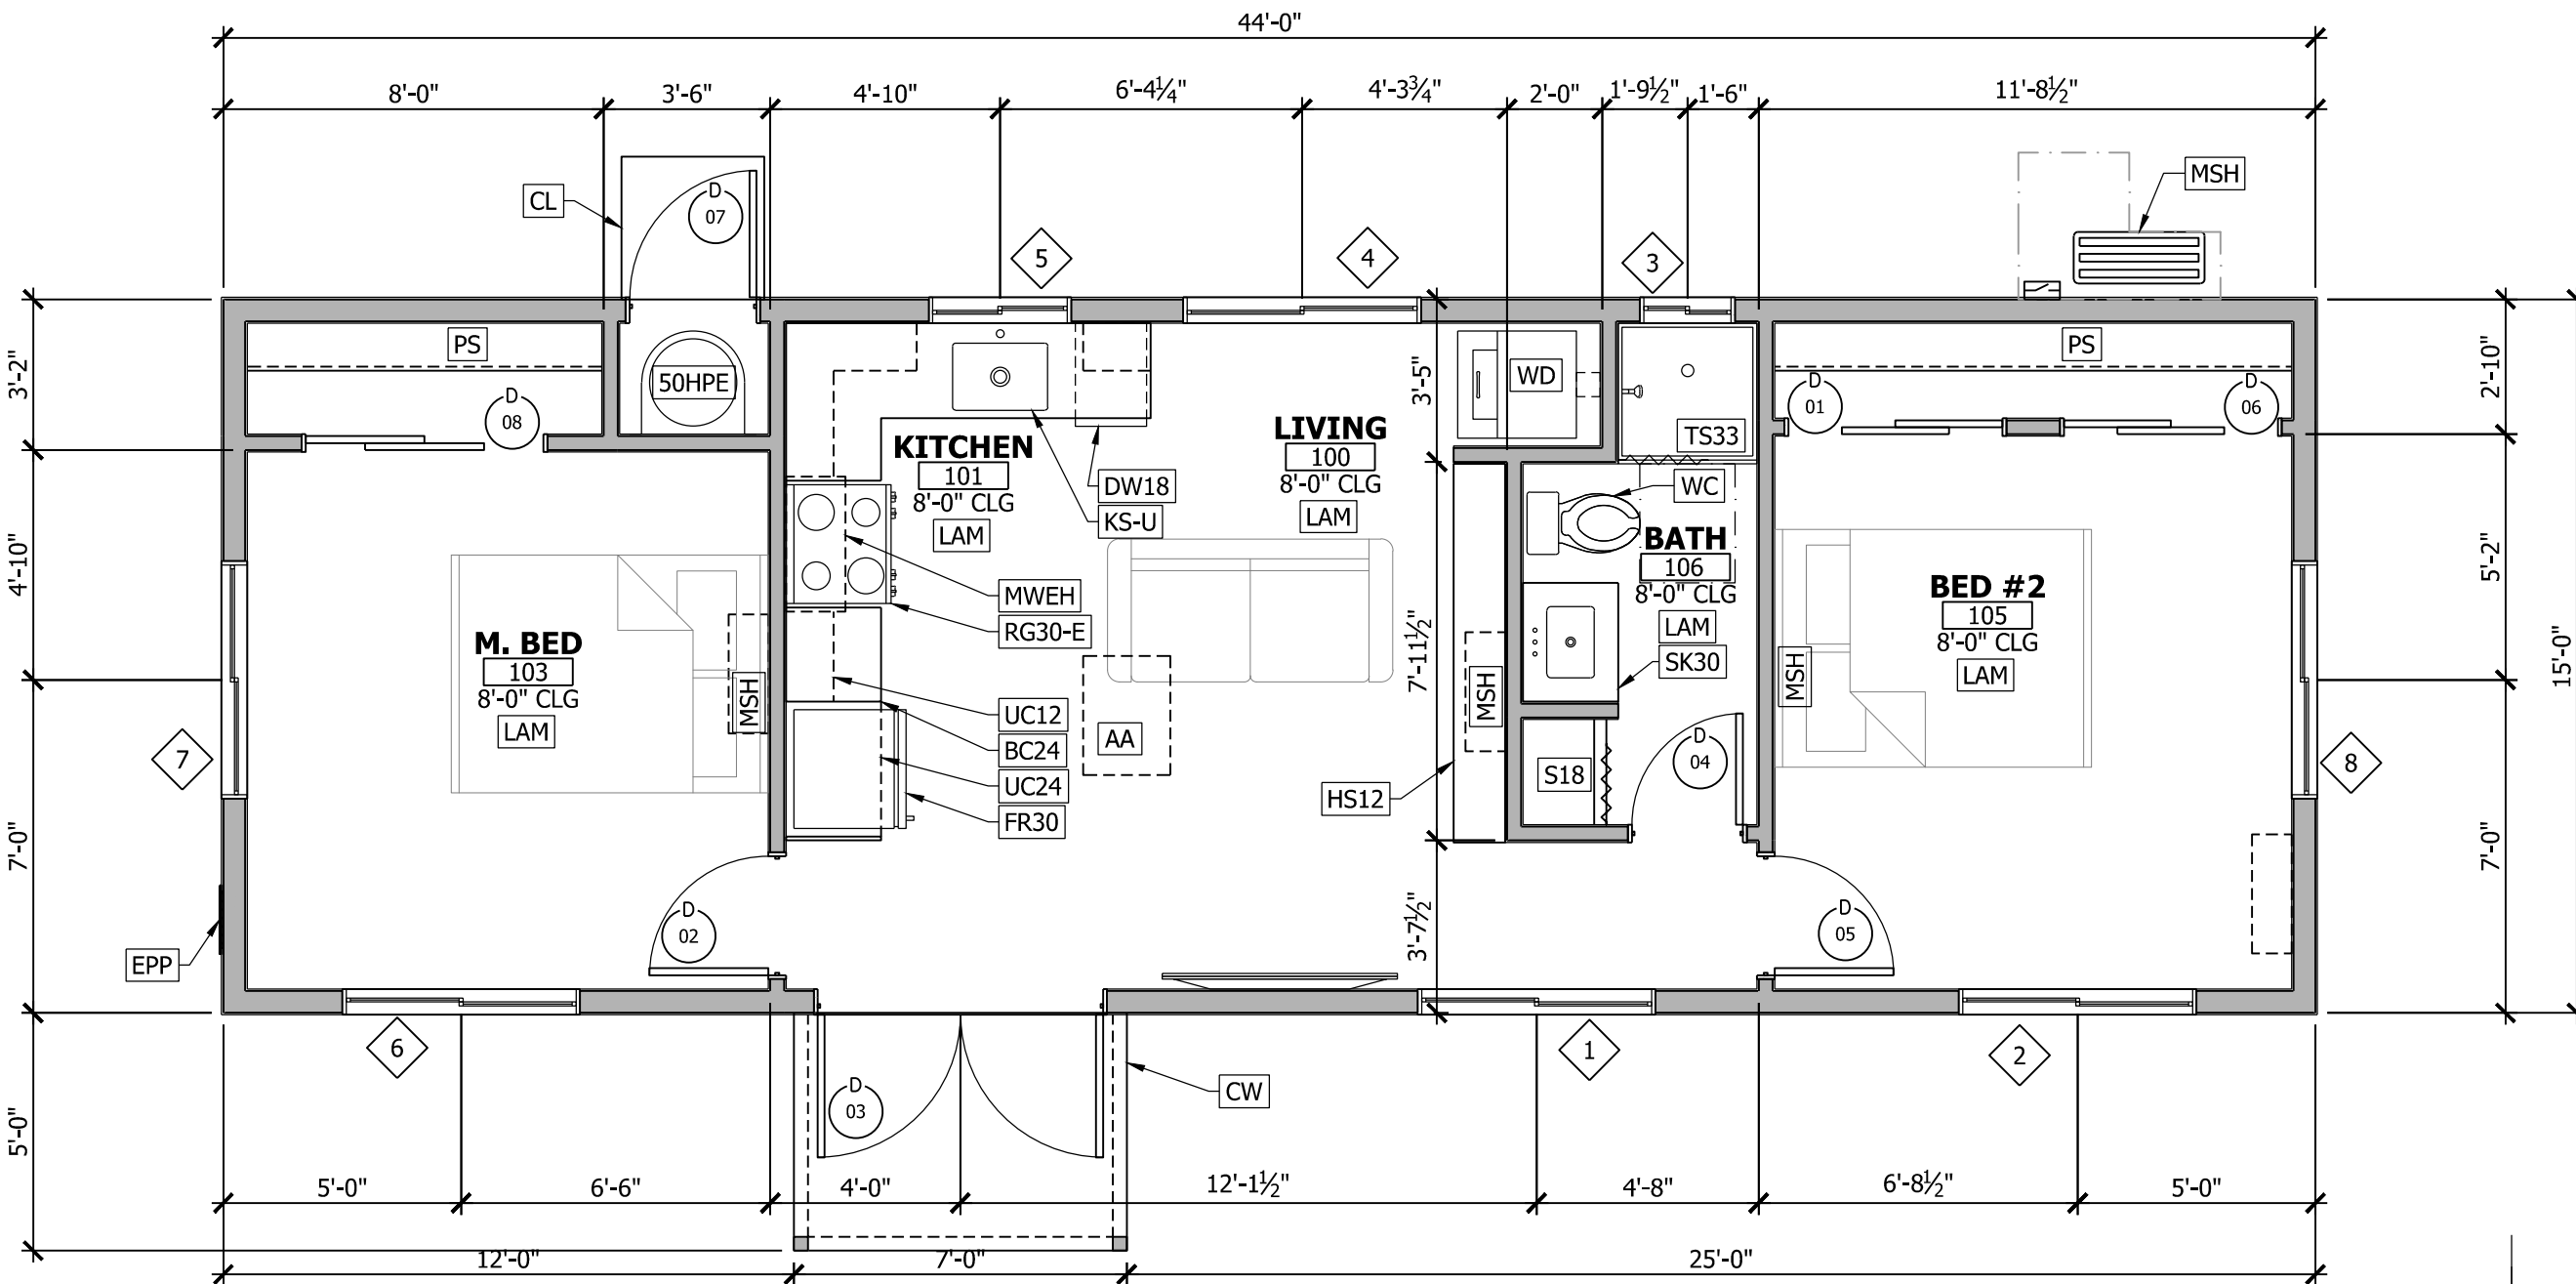


1 FLOOR PLAN

660 SF LIVING
35 SF COVERED PORCH

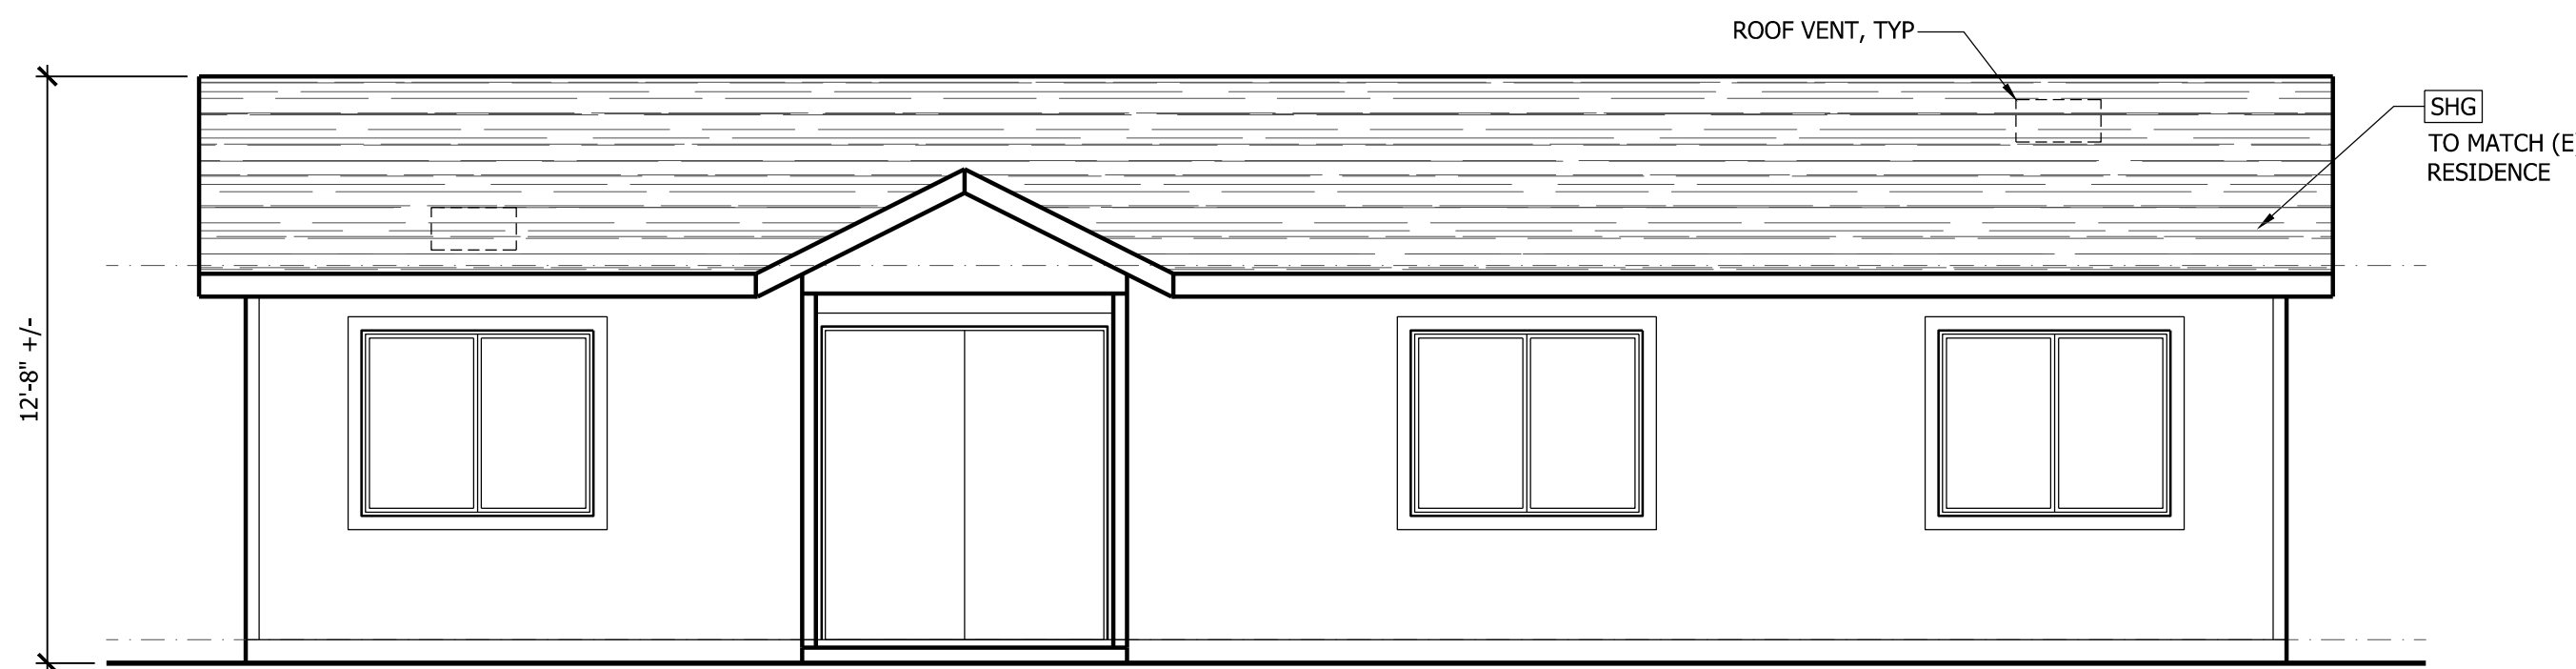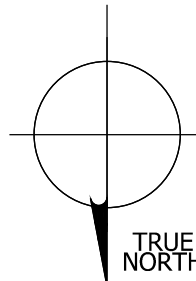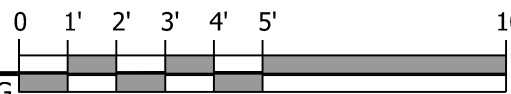

A FRONT ELEVATION

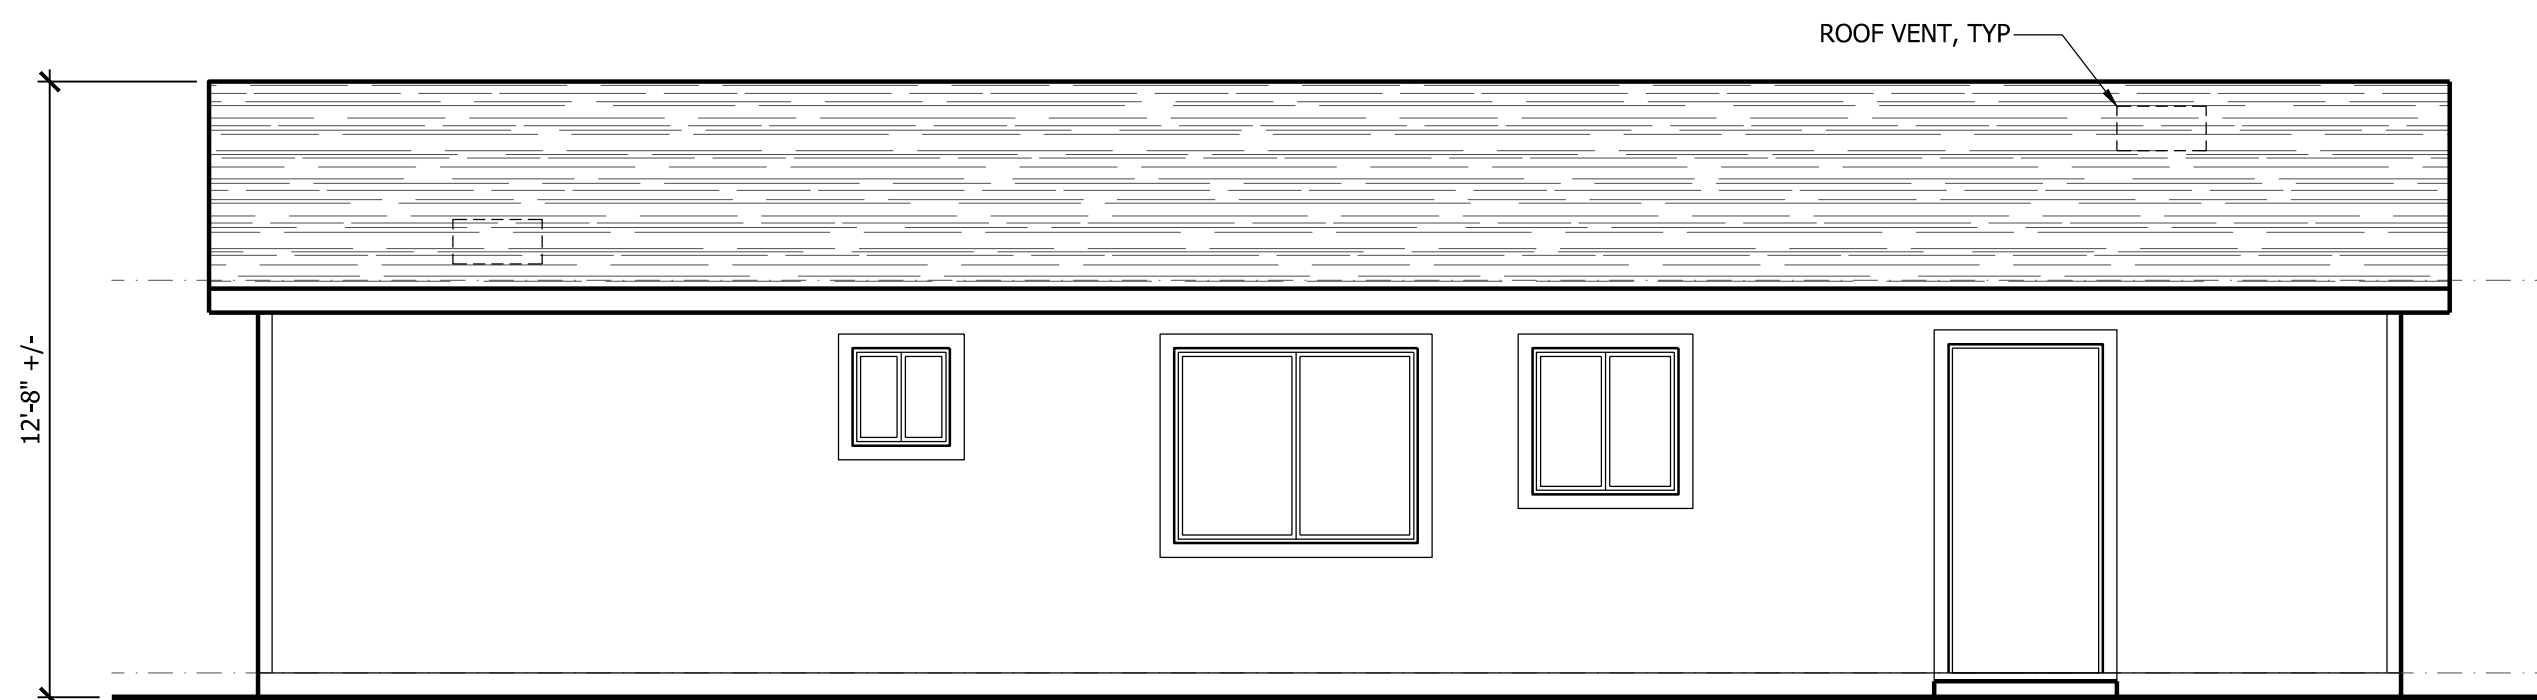

B REAR ELEVATION