

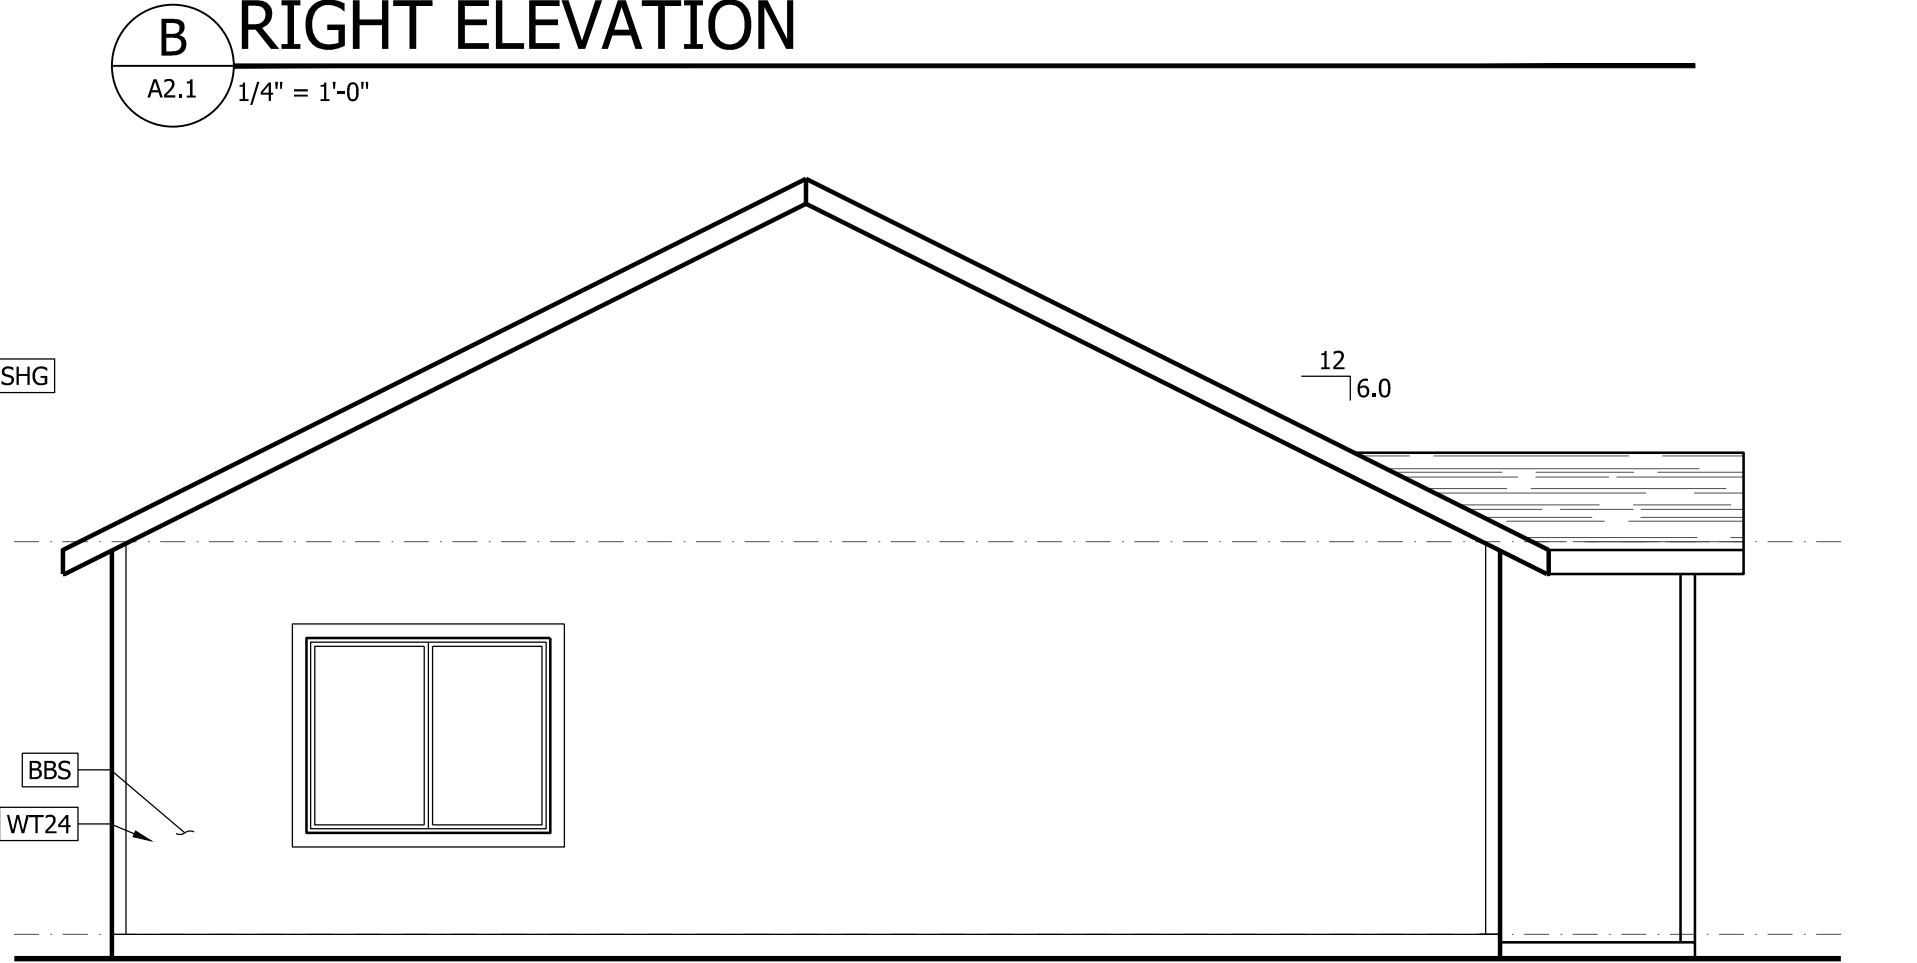
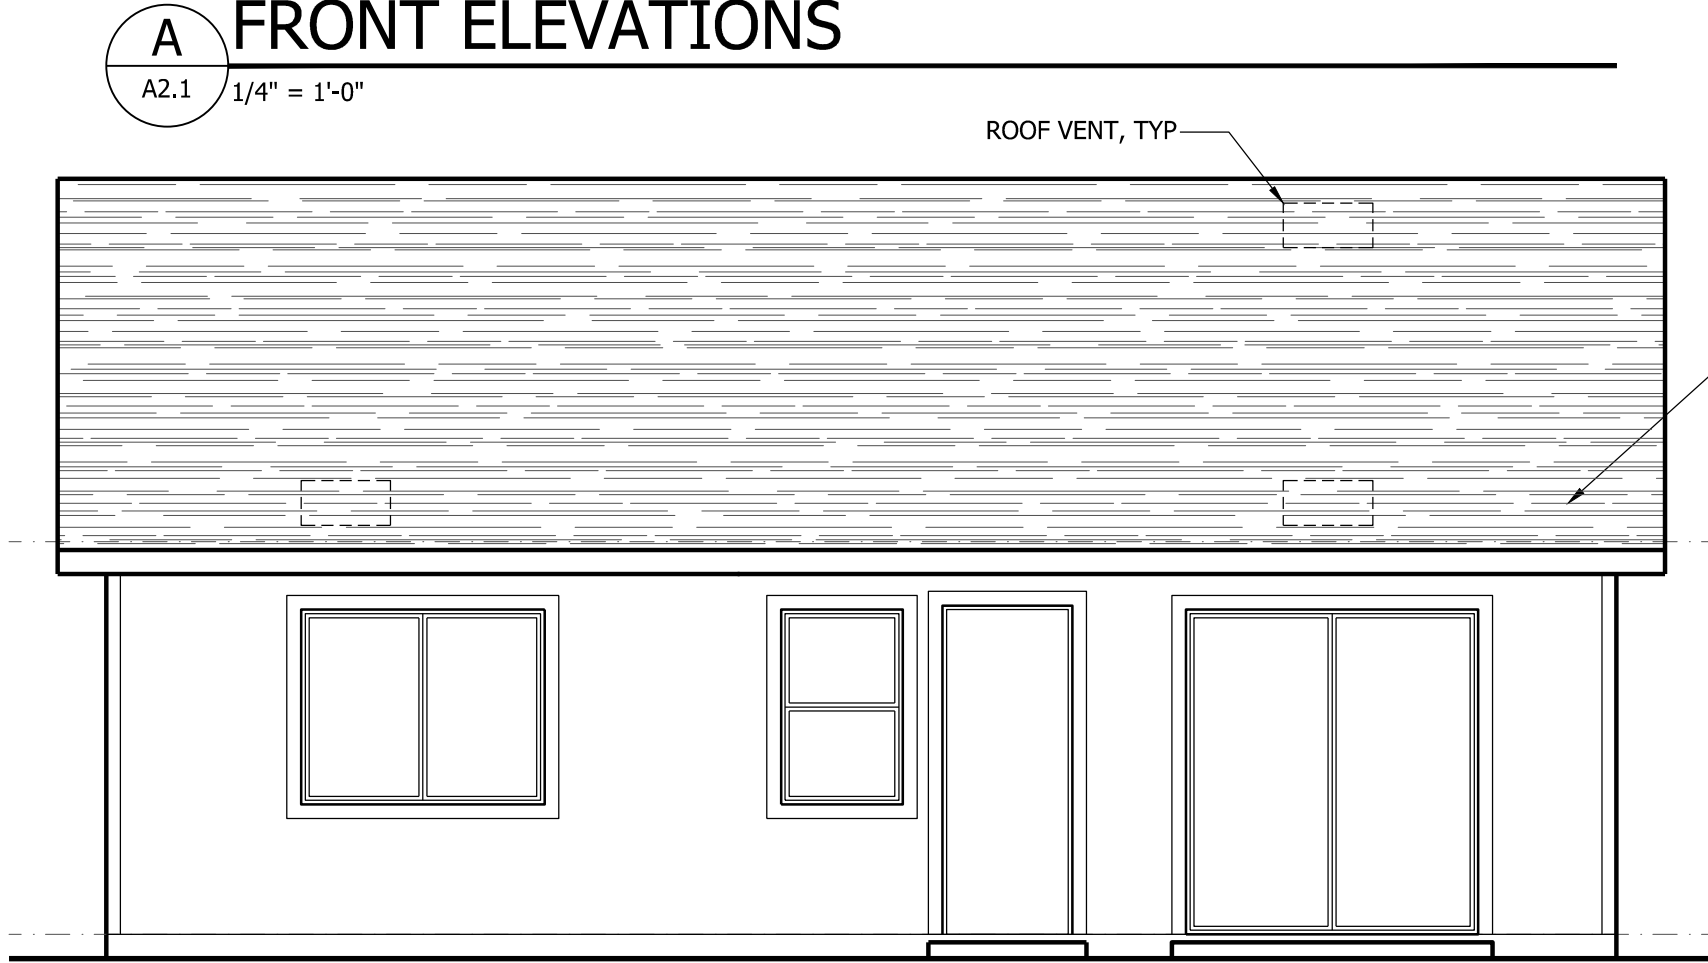


REFERENCE KEYNOTES	
DIVISION 03 - CONCRETE	
CL	- 4" THICK CONCRETE LANDING, MINIMUM 3'-0" DEEP x DOOR WIDTH. LANDING SHALL NOT EXCEED 1/4 UNIT VERTICAL IN 12 UNITS HORIZONTAL (2%)
CW	- CONCRETE WALK
DIVISION 06 - WOOD AND PLASTICS	
MISCELLANEOUS -	
WT24	- 2x4 WOOD TRIM
DIVISION 07 - THERMAL AND MOISTURE PROTECTION	
ROOF ACCESSORIES -	
AA	- 22"x30" ATTIC ACCESS, PERMANTLY ATTACH INSULATION USING ADHESIVE OR MECHANICAL FASTENERS TO ACCESS PANEL. ACCESS SHALL BE GASKETED TO PREVENT AIR LEAKAGE
ROOFING AND SIDING -	
SHG	- CLASS 'A' LIFETIME COMPOSITION ROOF SHINGLES o/ 15LB FELT COMPLIANT WITH TABLE R905.1(1). FASTEN ROOFING WITH CORROSION RESISTANT FASTENERS CRC R905.2.5
DIVISION 09 - FINISHES	
BBS	- 5/8" T1-11 BOARD AND BATTEN SIDING o/ TWO LAYER GRADE 'D' PAPER OR 1 LAYER TYVEK. NAILING PER STRUCTURAL
FLOORING -	
LVF	- LUXURY VINYL FLOORING
DIVISION 11 - EQUIPMENT	
D	- CLOTHES DRYER
DW18	- 18" DISHWASHER
FR30	- FRIDGE, 30" WIDE
MWEH	- MICROWAVE EXHAUST HOOD COMBINATION, MIN VENTILATION RATE OF 100 CFM (CMC TABLE 403.7), HVI RATED & LIMITED TO 3 SONES, HERS VERIFICATION REQUIRED
RG30-E	- 30" RANGE - ELECTRIC
W	- CLOTHES WASHER
DIVISION 12 - FURNISHINGS	
BC24	- 24" DEEP BASE CABINET
UC12	- 12" DEEP UPPER CABINET
UC24	- 24" DEEP UPPER CABINET
DIVISION 13 - SPECIAL CONSTRUCTION	
PS	- CLOSET POLE & SHELF
S24	- 24" DEEP SHELVES
DIVISION 15 - MECHANICAL	
50HPE	- 50 GALLON HYBRID HEAT PUMP ELECTRIC HOT WATER HEATER
MSH	- MINI SPLIT HEAD
MSU	- MINI SPLIT OUTDOOR UNIT, INSTALLED PER MANUFACTURER SPECIFICATIONS
DIVISION 16 - ELECTRICAL	
EPP	- ELECTRICAL SUB PANEL, 120/240V 125A, W/ UFER GROUND, PROVIDE 30"x30" WORKING AREA CENTERED IN FRONT OF PANEL
DIVISION 17 - PLUMBING	
KS	- KITCHEN SINK
SK36	- SINK w/VANITY 36"
TS33	- TILE SHOWER 3x3, CURB OR FINISHED THRESHOLD SHALL COMPLY WITH CPC 408.5
WC	- WATER CLOSET, MINIMUM 30" CLEAR WIDTH CENTERED ON WATER CLOSET & 24" CLEAR SPACE OFF NOSE OF WATER CLOSET.

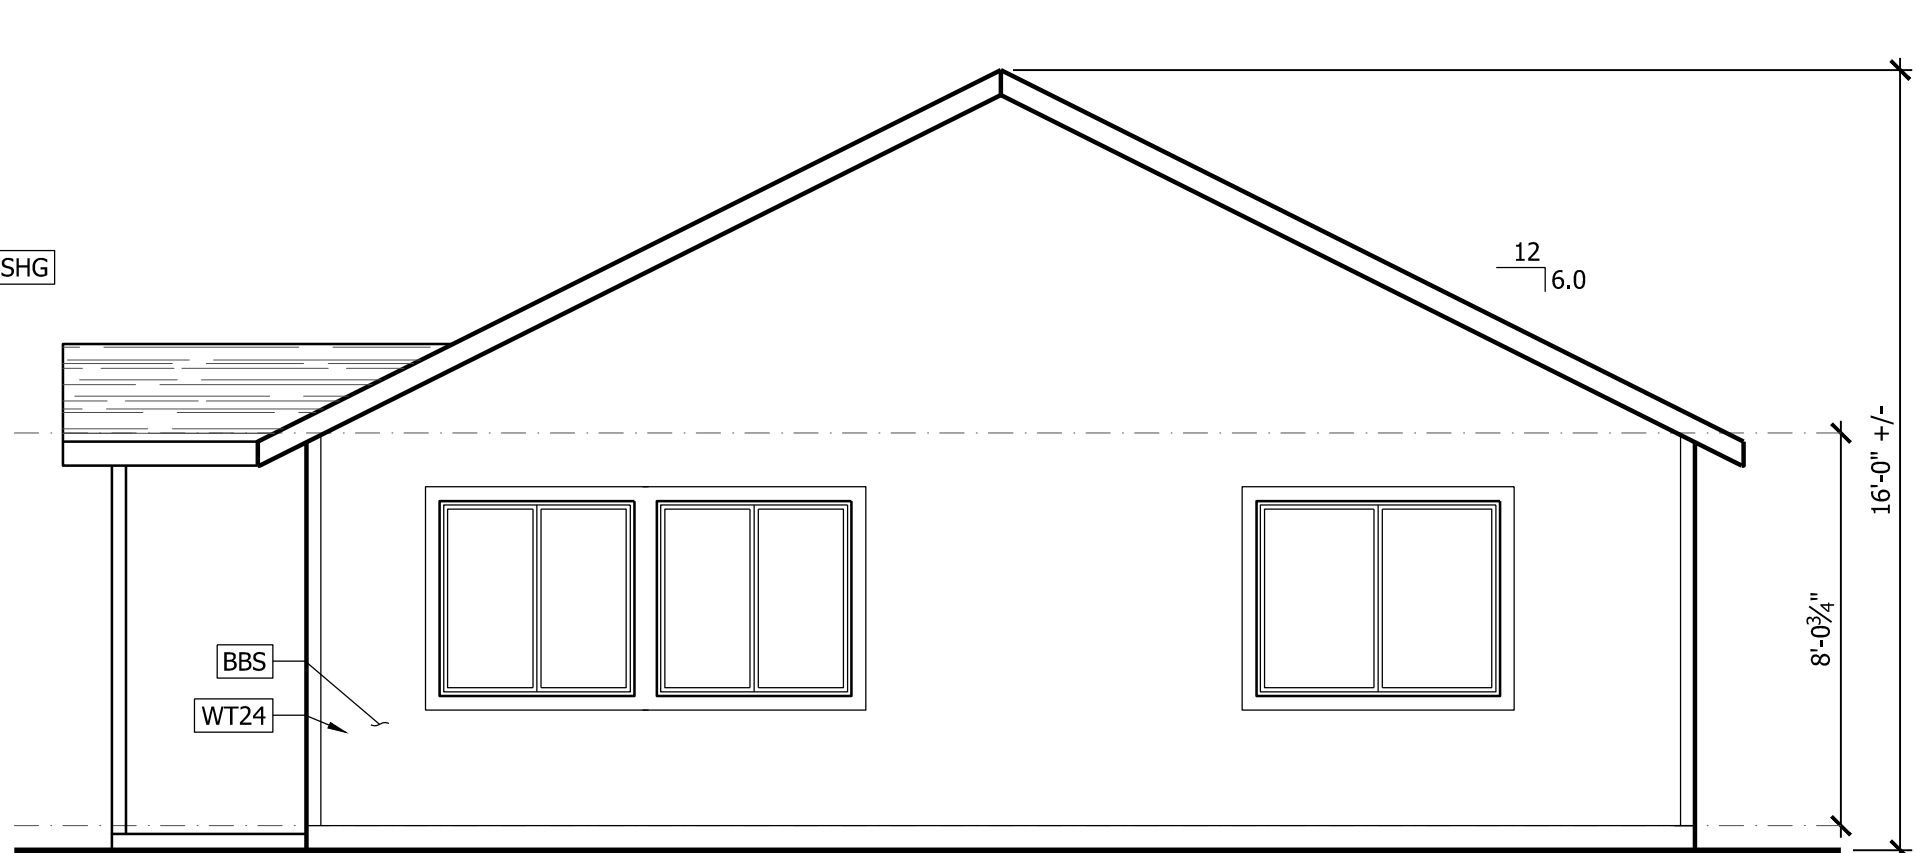

WINDOW SCHEDULE						
NUMBER	SIZE		STYLE	HEAD HEIGHT	SHCG	U-FACTOR
	WIDTH	HEIGHT				
1	3'-0"	3'-0"	SLIDER	6'-8"	.23	.30
2	4'-0"	4'-0"	SLIDER	6'-8"	.23	.30
3	4'-0"	4'-0"	SLIDER	6'-8"	.23	.30
4	4'-0"	4'-0"	SLIDER	6'-8"	.23	.30
5	4'-0"	4'-0"	SLIDER	6'-8"	.23	.30
6	5'-0"	4'-0"	SLIDER	6'-8"	.23	.30
7	5'-0"	4'-0"	SLIDER	6'-8"	.23	.30
8	2'-6"	4'-0"	SINGLE HUNG	6'-8"	.23	.30
9	5'-0"	4'-0"	SLIDER	6'-8"	.23	.30

DOOR AND FRAME SCHEDULE			
NUMBER	SIZE	STYLE	NOTES
2	3'-0" x 6'-8" x 1-3/4"	SINGLE - EXTERIOR	- - -
3	2'-6" x 6'-8" x 1-3/4"	SINGLE - INTERIOR	- - -
4	PR 3'-0" x 6'-8" x 1-3/4"	HORIZONTAL BYPASS	- - -
5	2'-6" x 6'-8" x 1-3/4"	SINGLE - INTERIOR	- - -
6	2'-6" x 6'-8" x 1-3/4"	SINGLE - INTERIOR	- - -
7	2'-6" x 6'-8" x 1-3/4"	SINGLE - INTERIOR	- - -
8	PR 3'-0" x 6'-8" x 1-3/4"	HORIZONTAL BYPASS	- - -
9	2'-6" x 6'-8" x 1-3/4"	SINGLE - EXTERIOR	- - -
10	PR 3'-0" x 6'-8" x 1-1/4"	SLIDING - EXTERIOR	- - -

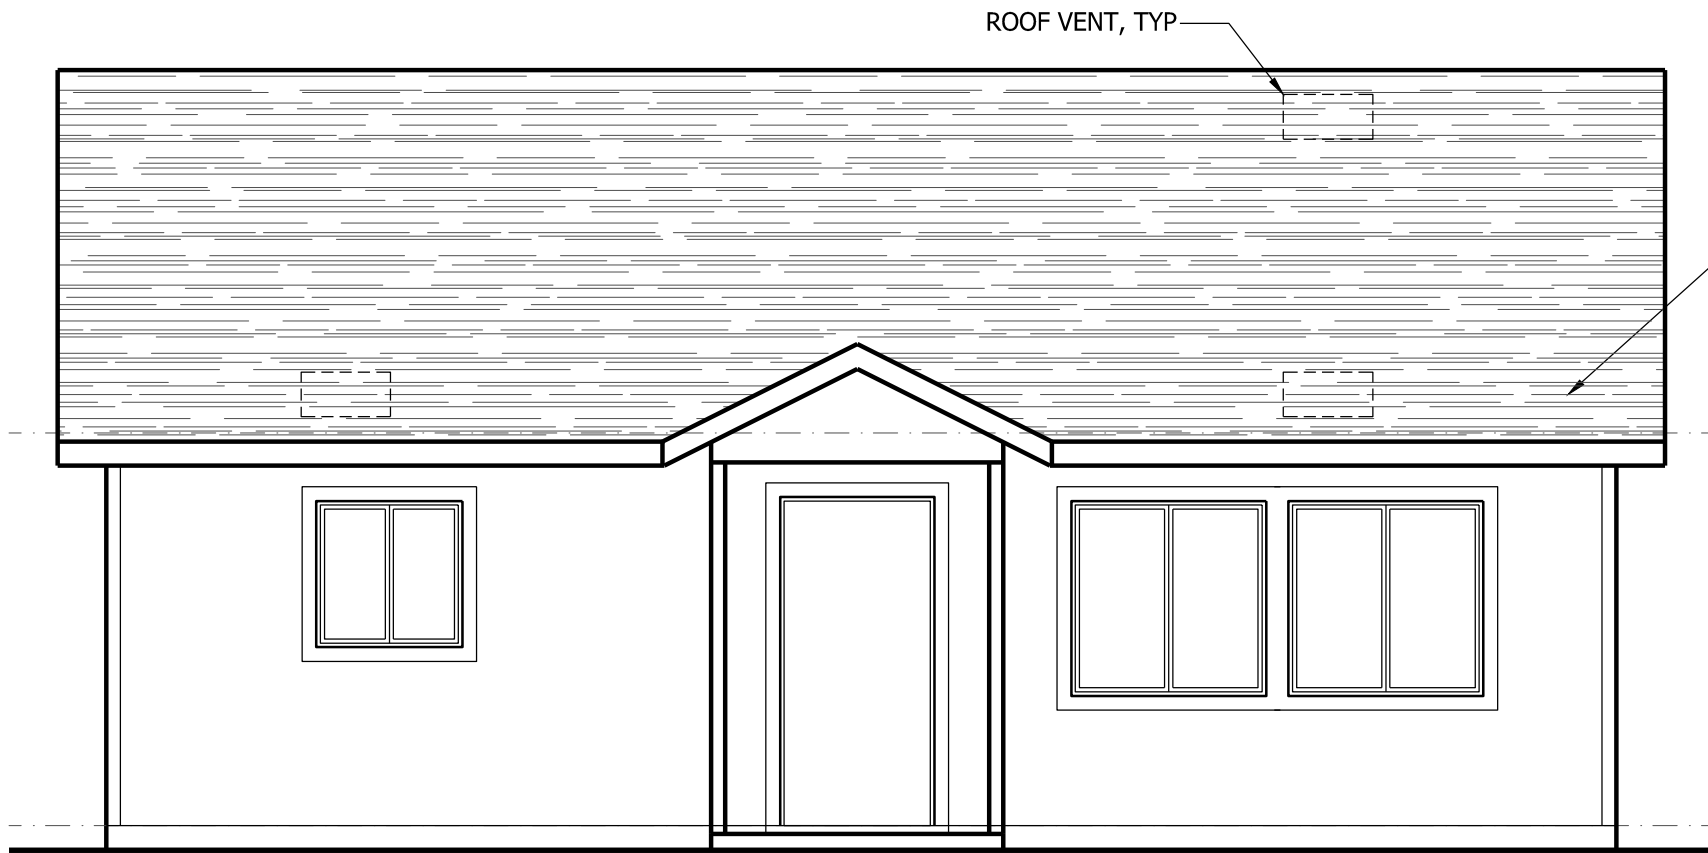