




REFERENCE KEYNOTES	
DIVISION 03 - CONCRETE	
CW	- CONCRETE WALK
DIVISION 06 - WOOD AND PLASTICS	
R-F	- RAISED FOUNDATION
WDDK	- WOOD DECK
MISCELLANEOUS -	
WT24	- 2x4 WOOD TRIM
DIVISION 07 - THERMAL AND MOISTURE PROTECTION	
ROOF ACCESSORIES -	
AAL	- ATTIC ACCESS w/LADDER
ST	- SOLAR TUBE
ROOFING AND SIDING -	
SHG	- CLASS 'A' LIFETIME COMPOSITION ROOF SHINGLES o/ 15LB FELT COMPLIANT WITH TABLE R905.1(1). FASTEN ROOFING WITH CORROSION RESISTANT FASTENERS CRC R905.2.5
DIVISION 09 - FINISHES	
BBS	- 5/8" T1-11 BOARD AND BATTEN SIDING o/ TWO LAYER GRADE "D" PAPER OR 1 LAYER TYVEK. NAILING PER STRUCTURAL
FLOORING -	
LAM	- LAMINATE FLOORING
DIVISION 10 - SPECIALTIES	
TV-FP	- TV MOUNTED ABOVE GAS FIREPLACE, FURR OUT WALL AS REQUIRED PER FIREPLACE SPECIFICATIONS
DIVISION 11 - EQUIPMENT	
DW18	- 18" DISHWASHER
FR36	- FRIDGE, 36" WIDE
MWEH	- MICROWAVE EXHAUST HOOD COMBINATION, MIN VENTILATION RATE OF 100 CFM (CMC TABLE 403.7), HVI RATED & LIMITED TO 3 SONES, HERS VERIFICATION REQUIRED
RG30-E	- 30" RANGE - ELECTRIC
WD	- STACKED WASHER AND DRYER, PROVIDE MIN 2" STANDPIPE
DIVISION 12 - FURNISHINGS	
BC24	- 24" DEEP BASE CABINET
UC12	- 12" DEEP UPPER CABINET
UC24	- 24" DEEP UPPER CABINET
DIVISION 15 - MECHANICAL	
40HPE	- 40 GALLON HYBRID HEAT PUMP ELECTRIC HOT WATER HEATER, DRAIN TO EXTERIOR
MSH	- MINI SPLIT HEAD
MSU	- MINI SPLIT OUTDOOR UNIT, INSTALLED PER MANUFACTURER SPECIFICATIONS
DIVISION 16 - ELECTRICAL	
EMP	- 120/240V 125A METER & MAIN PANEL
DIVISION 17 - PLUMBING	
KS	- KITCHEN SINK
SH-P-ADA	- PREFAB SHOWER ADA
SK36	- SINK w/VANITY 36"
WC	- WATER CLOSET, MINIMUM 30" CLEAR WIDTH CENTERED ON WATER CLOSET & 24" CLEAR SPACE OFF NOSE OF WATER CLOSET.

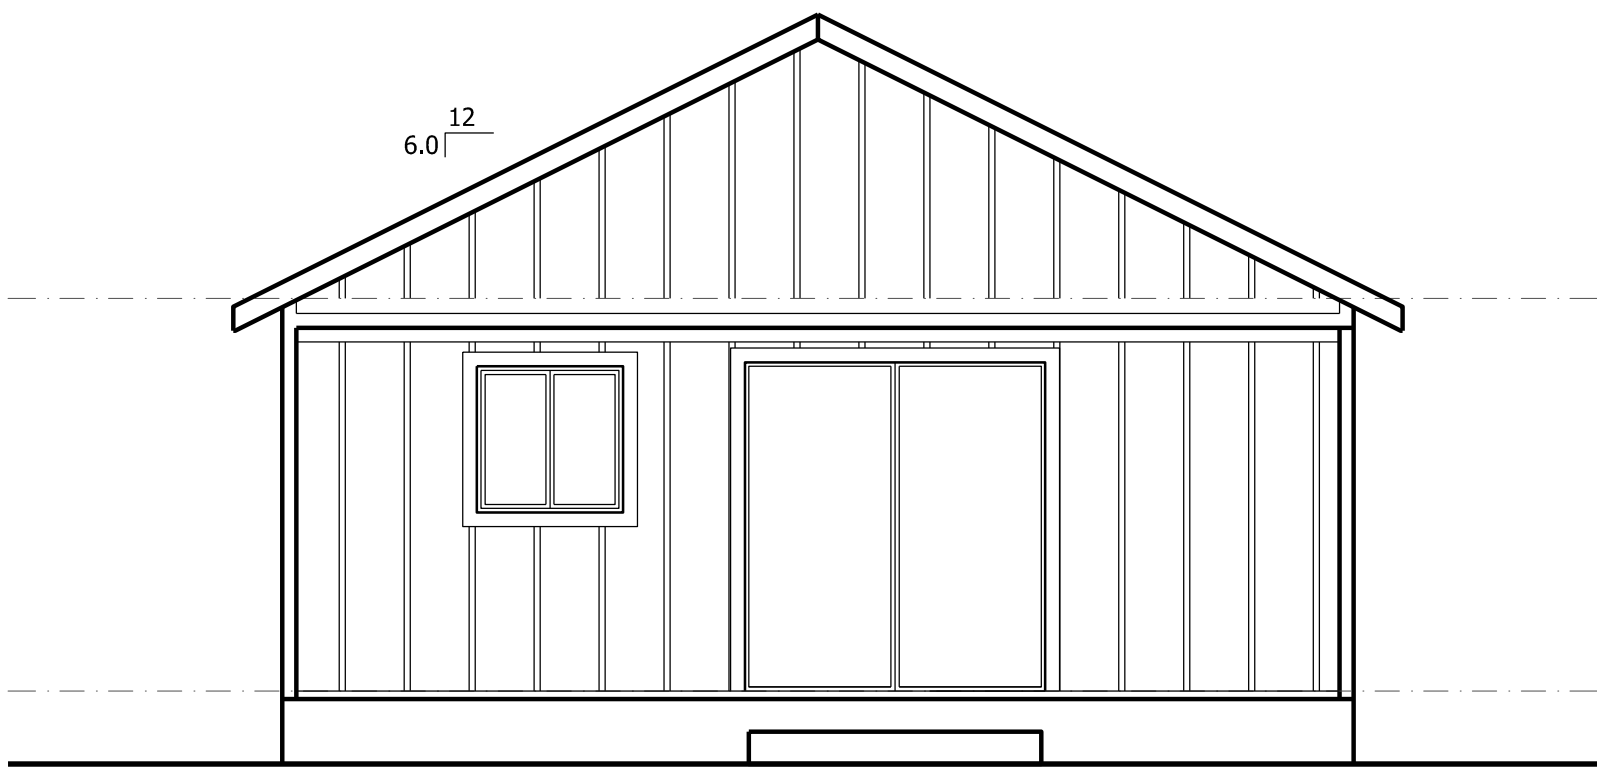


B LEFT ELEVATION
A2.1 1/4" = 1'-0"

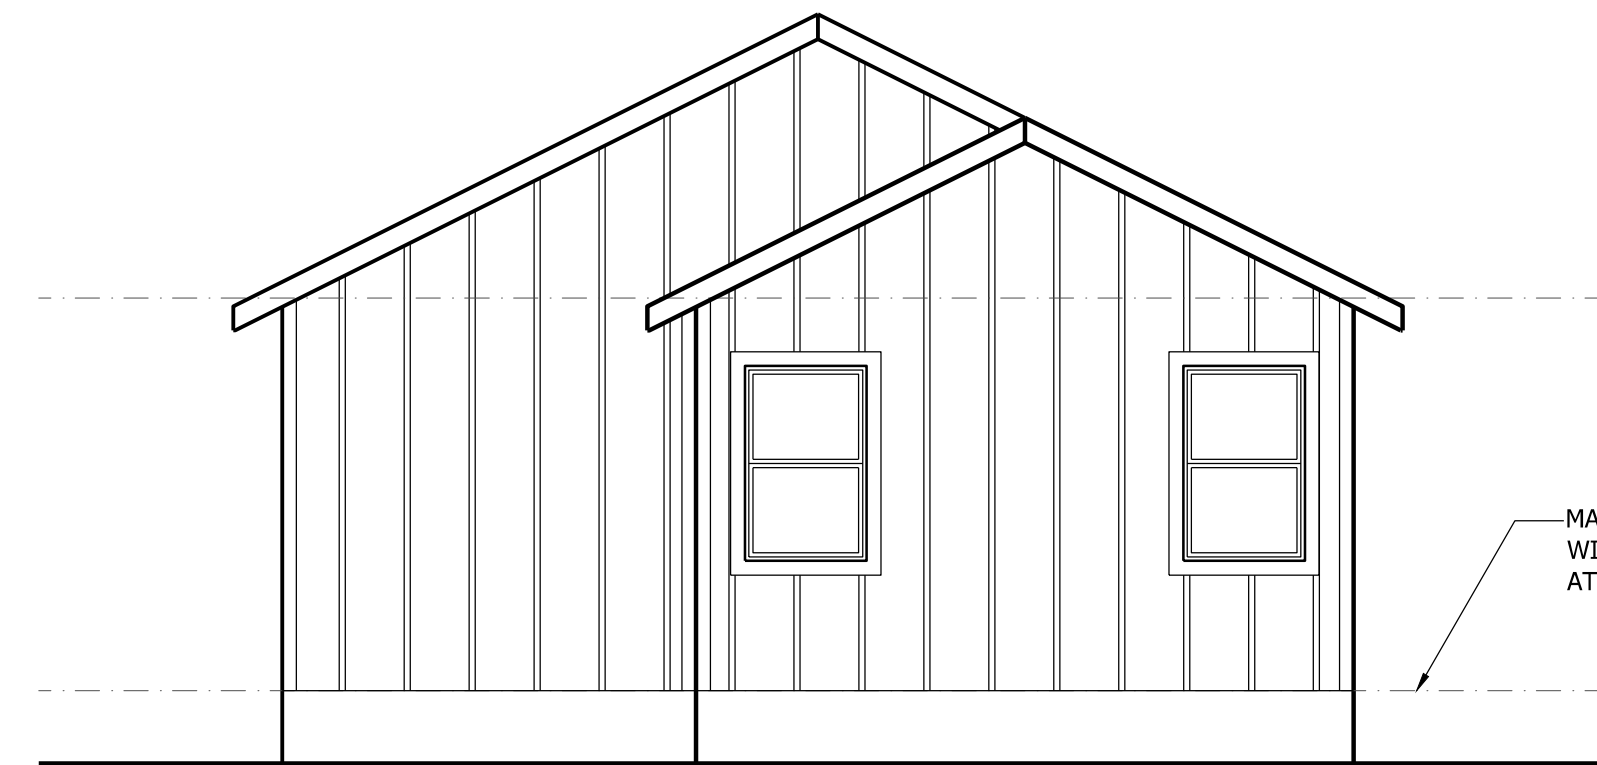

C RIGHT ELEVATION
A2.1 1/4" = 1'-0"

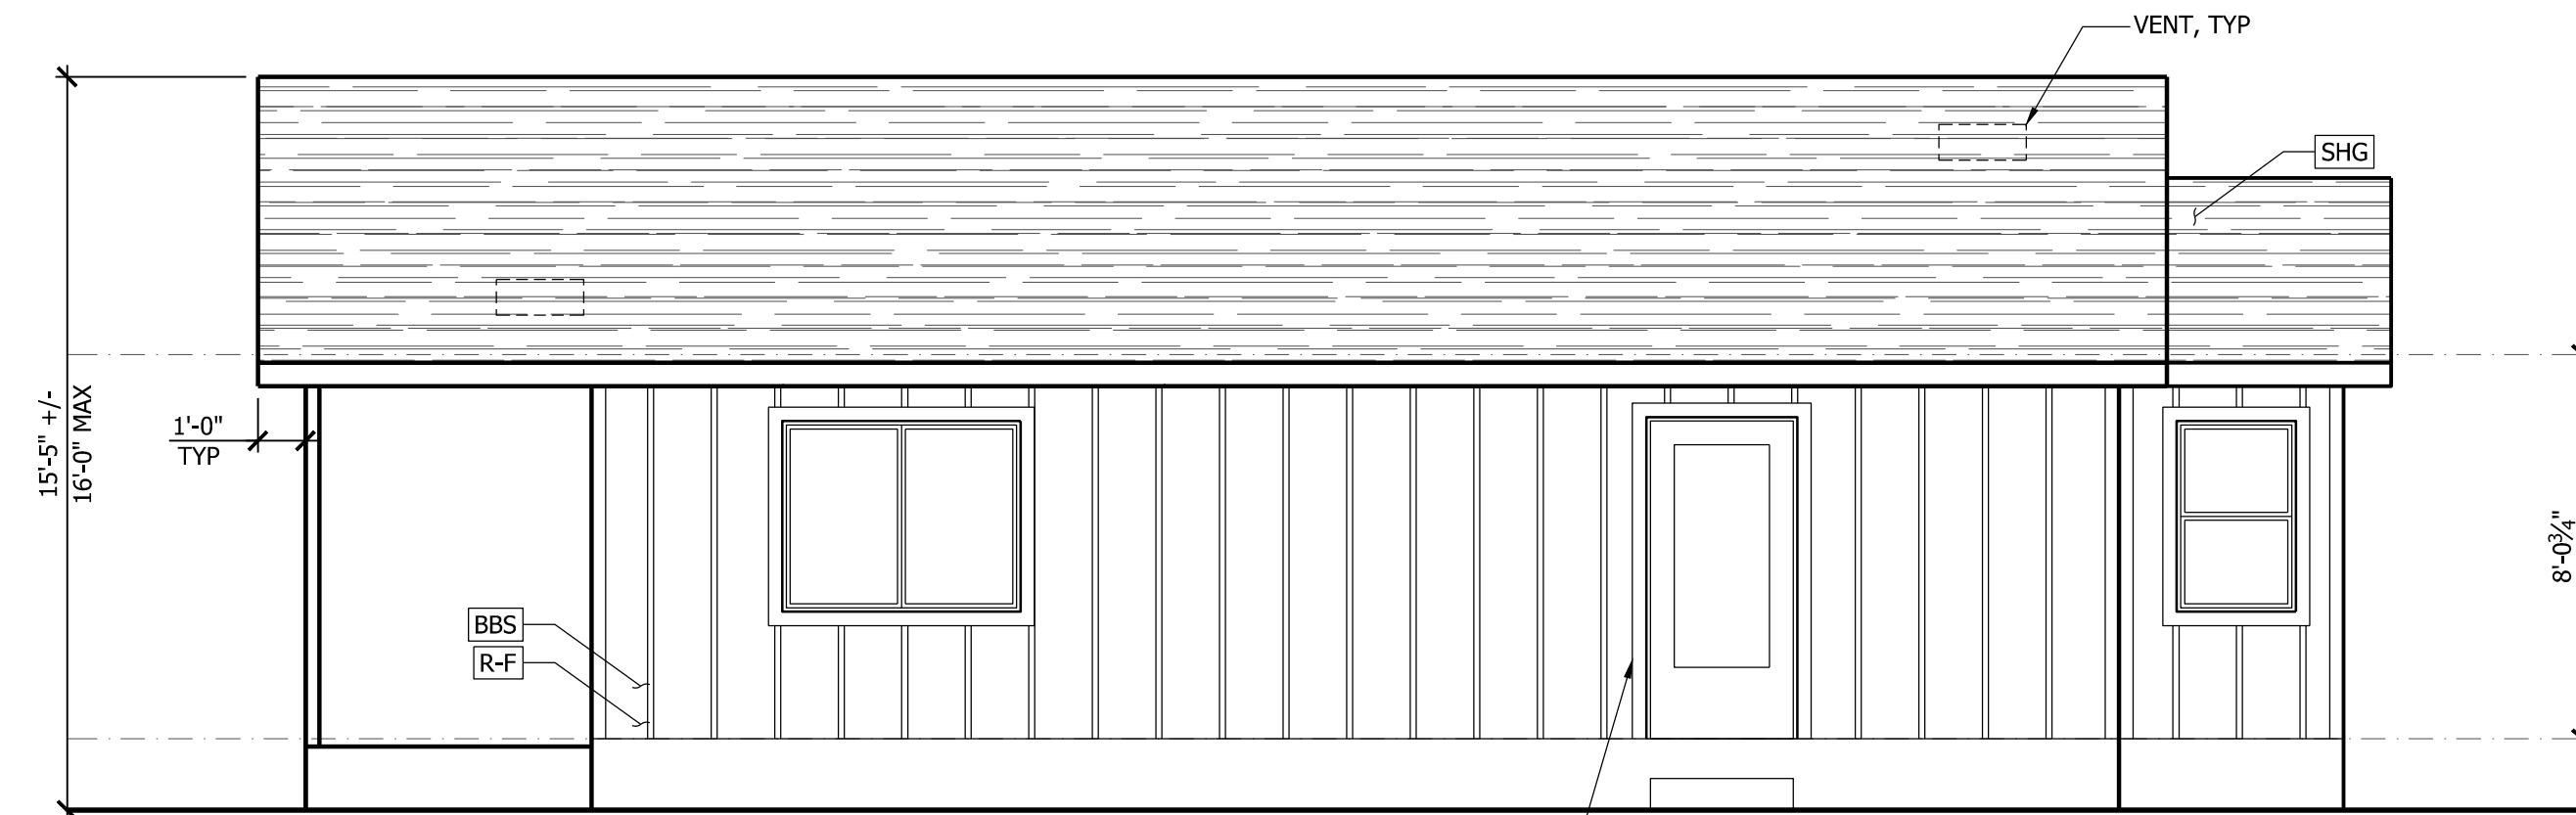


A FRONT ELEVATION
A2.1 1/4" = 1'-0"

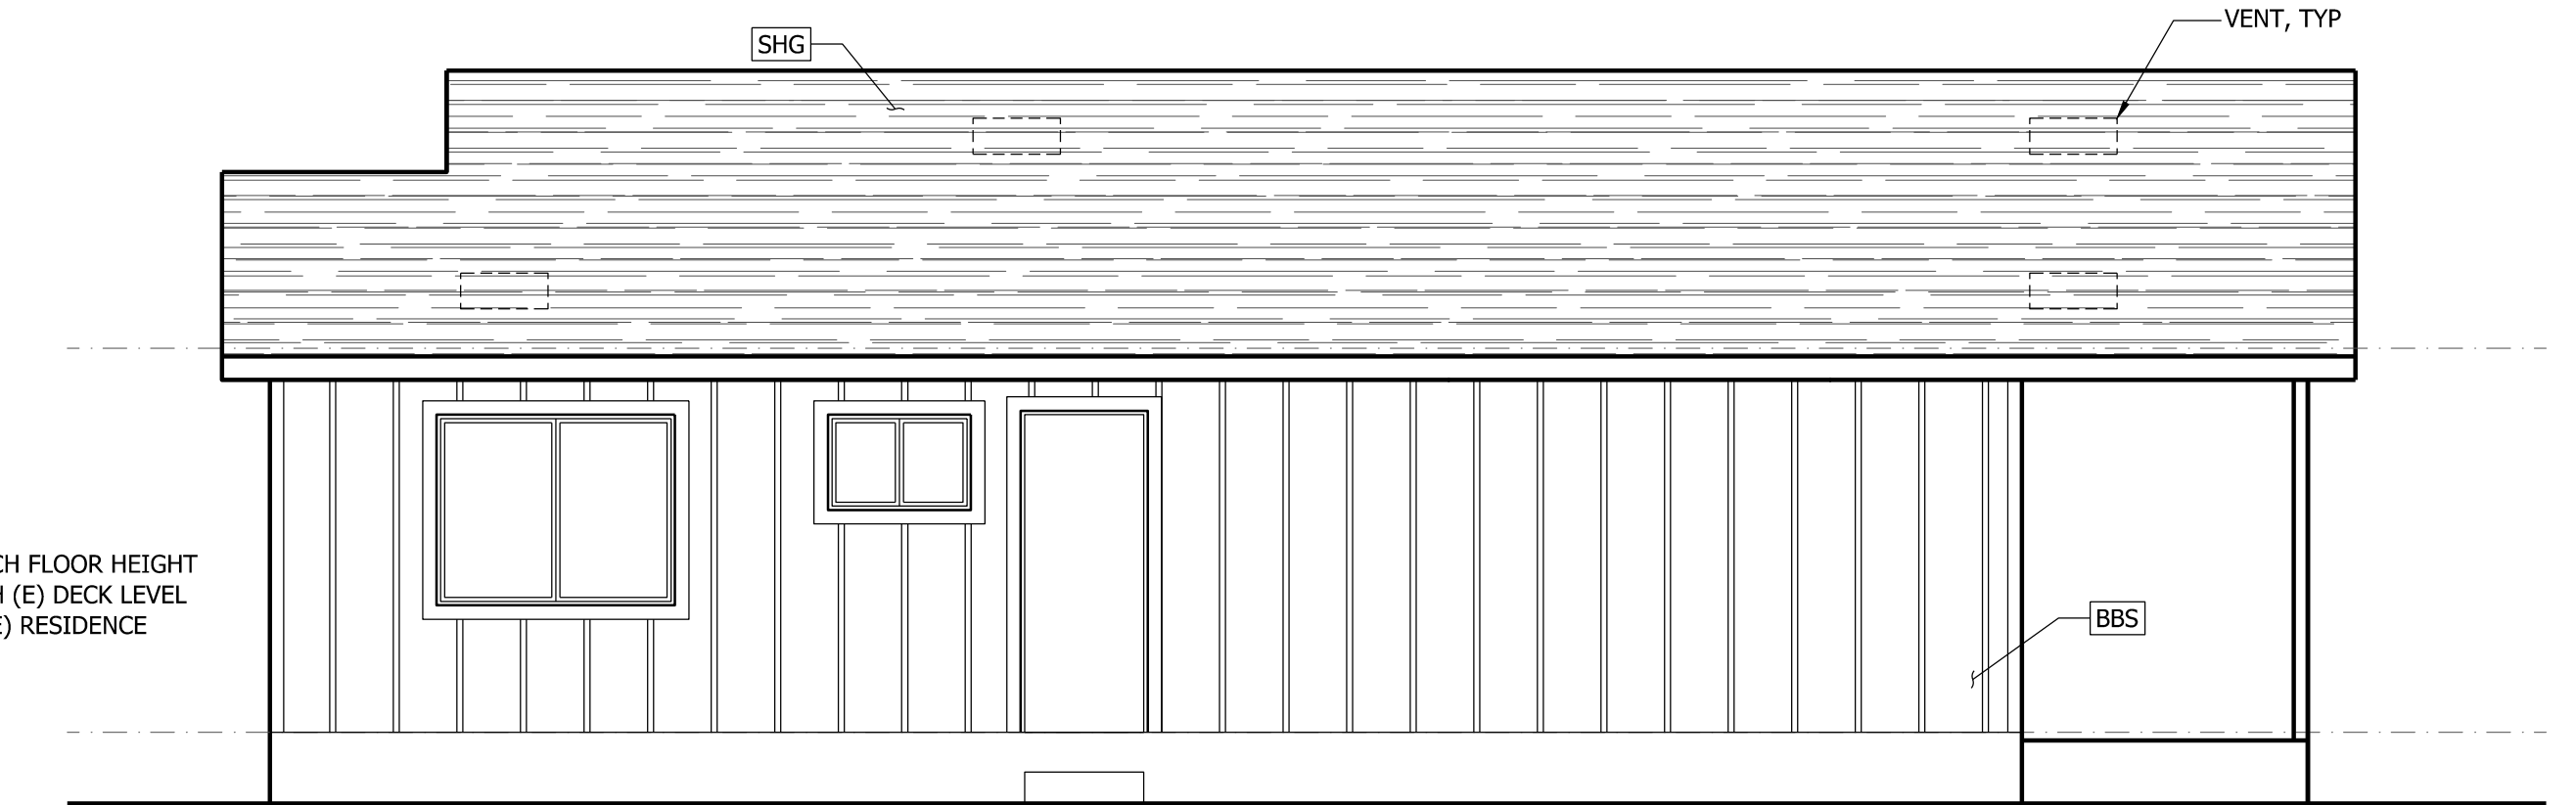

D REAR ELEVATION
A2.1 1/4" = 1'-0"

WINDOW SCHEDULE							
NUMBER	SIZE		STYLE	HEAD HEIGHT	SHCG	U-FACTOR	NOTES
1	2'-6"	4'-0"	SINGLE HUNG	6'-8"	.23	.30	--
2	5'-0"	4'-0"	SLIDER	6'-8"	.23	.30	--
3	3'-0"	3'-0"	SLIDER	6'-8"	.23	.30	--
4	3'-0"	2'-0"	SLIDER	6'-8"	.23	.30	FROSTED/TEMP
5	2'-6"	4'-0"	SINGLE HUNG	6'-8"	.23	.30	--
6	2'-6"	4'-0"	SINGLE HUNG	6'-8"	.23	.30	--
7	5'-0"	4'-0"	SLIDER	6'-8"	.23	.30	EGRESS

DOOR AND FRAME SCHEDULE				
NUMBER	SIZE	STYLE	FIRE RATING	NOTES
1	3'-0" x 6'-8" x 1-3/4"	SINGLE - EXTERIOR	--	--
2	PR 3'-0" x 6'-8" x 1-1/4"	SLIDING - EXTERIOR	--	--
3	2'-6" x 6'-8" x 1-3/4"	SINGLE - INTERIOR	--	--
4	3'-0" x 6'-8" x 1-3/4"	SINGLE - INTERIOR	--	--
5	3'-0" x 6'-8" x 1-3/4"	POCKET	--	--
7	PR 1'-3" x 6'-8" x 1-3/4"	BIFOLD	--	LOUVERED, MIN 100 SQ IN
8	2'-6" x 6'-8" x 1-3/4"	SINGLE - EXTERIOR	--	--
9	2'-6" x 6'-8" x 1-3/4"	POCKET	--	--

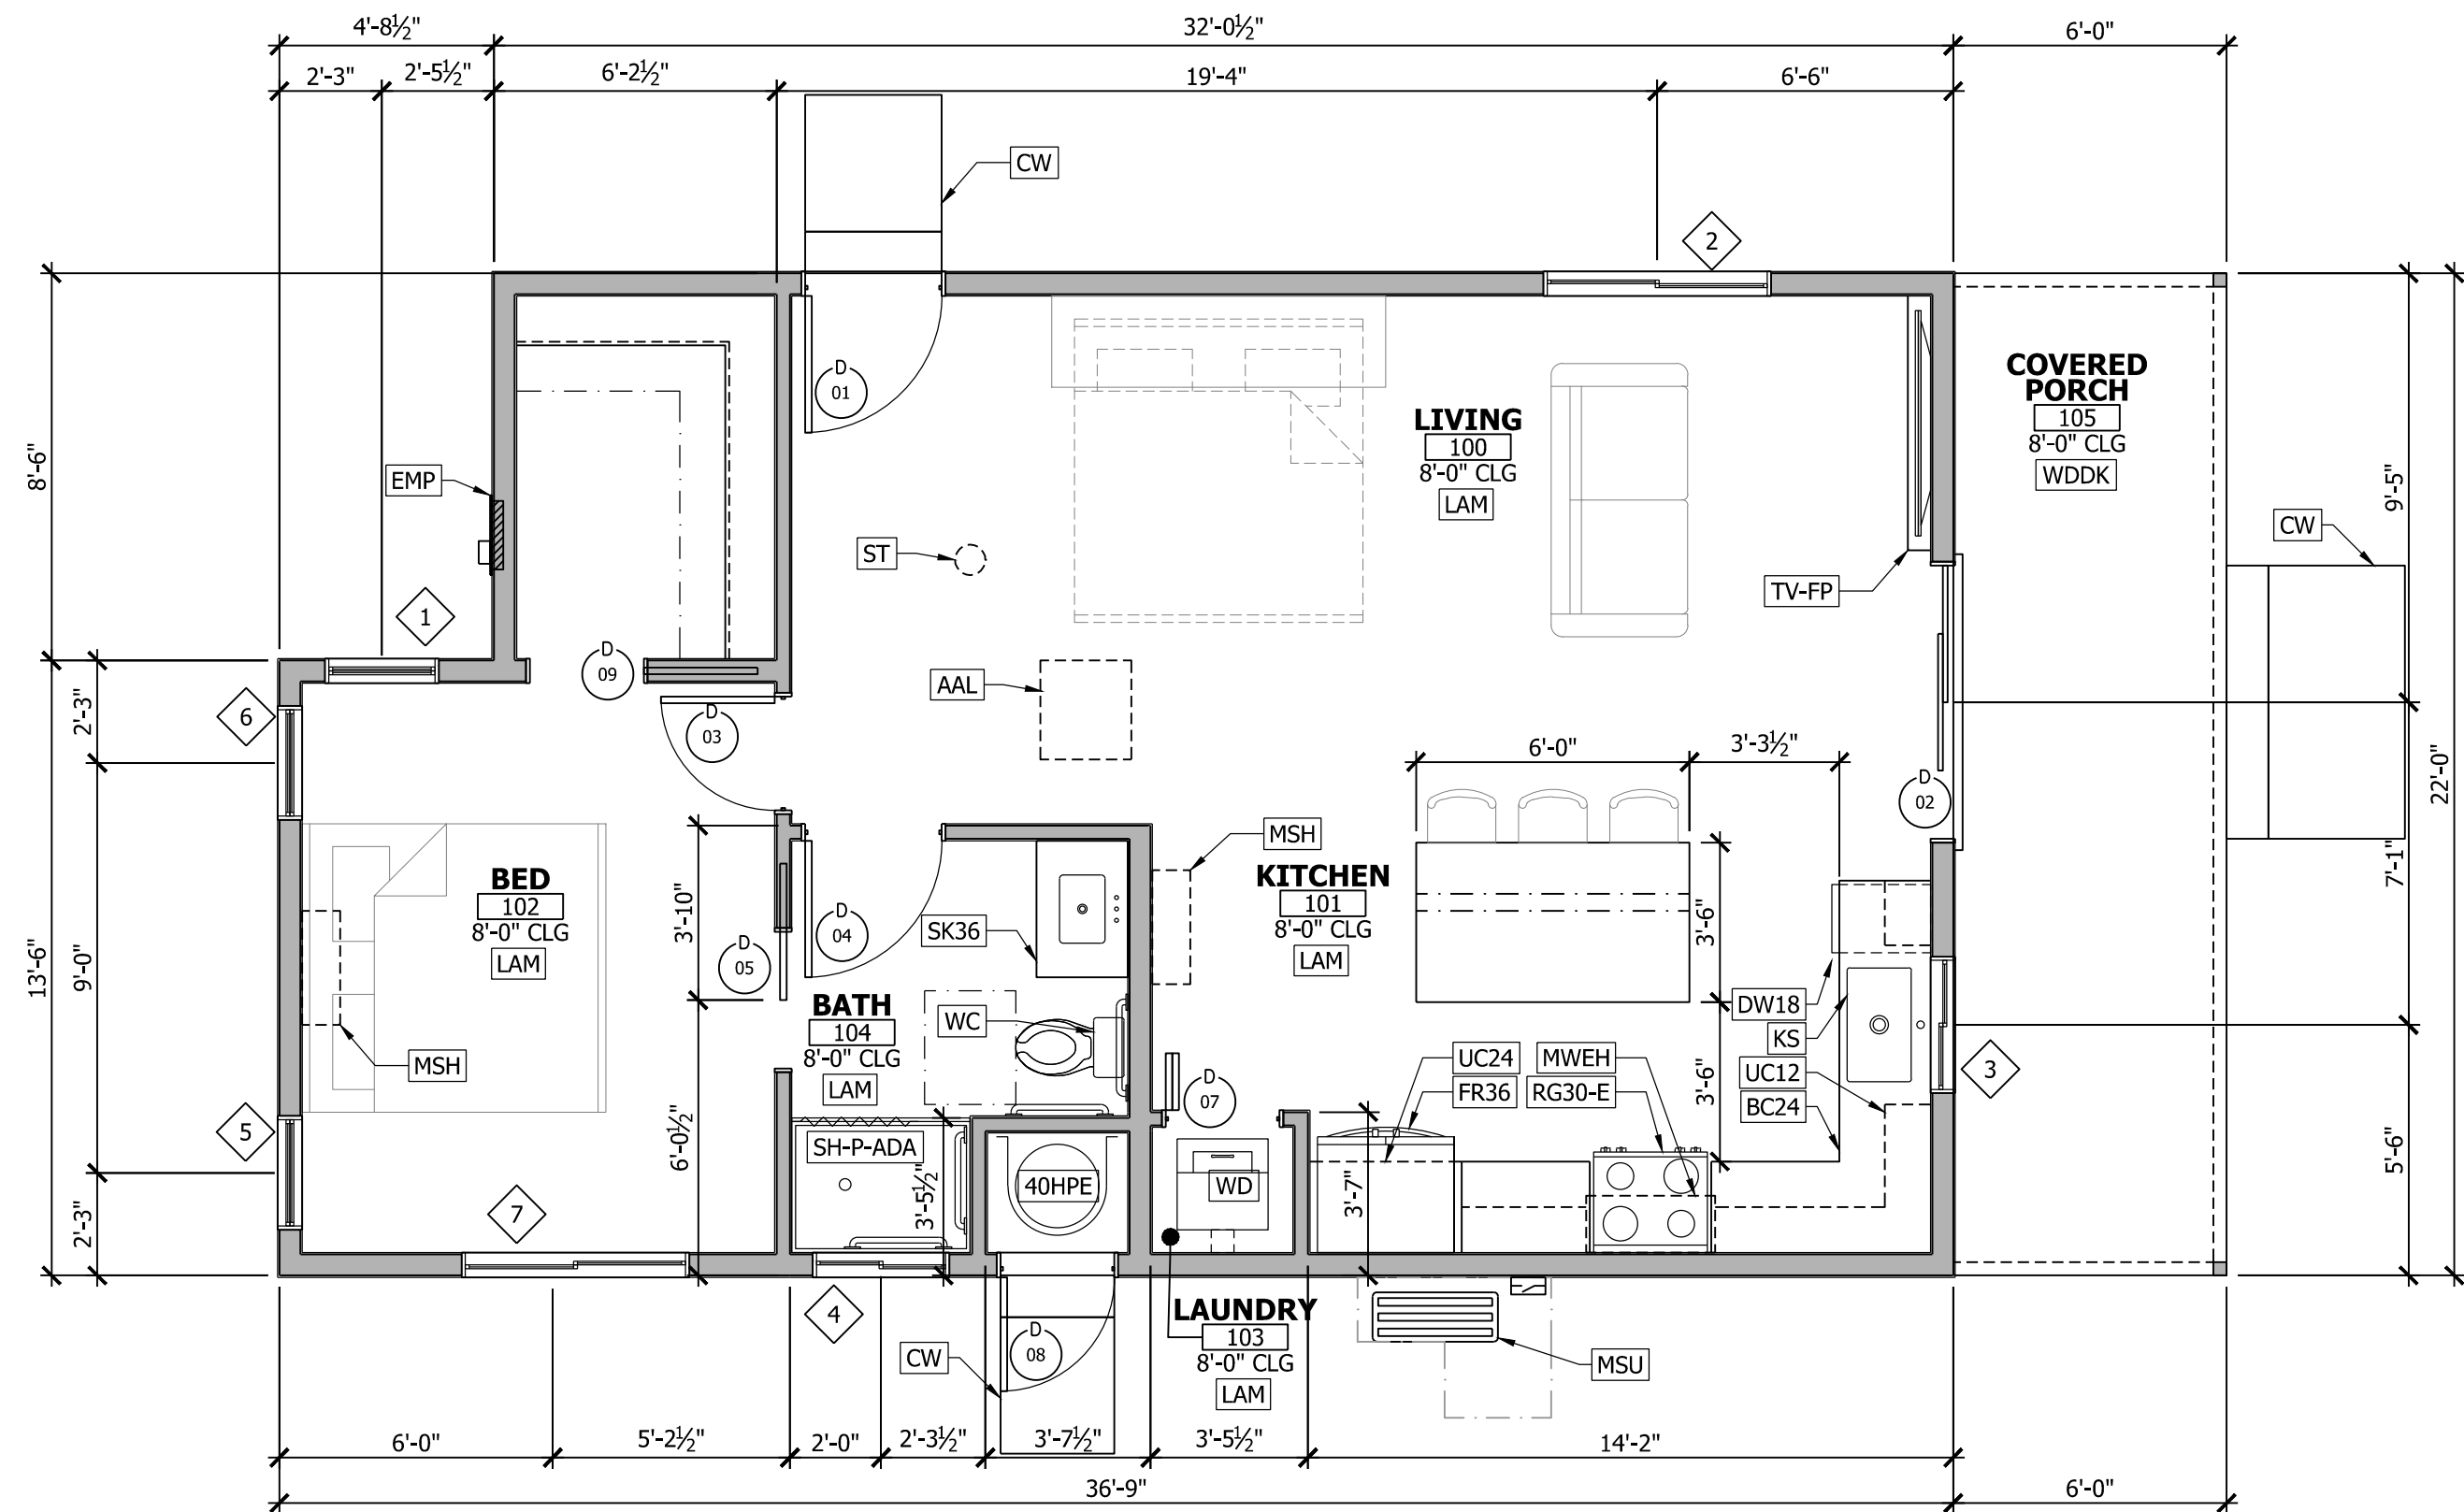

1 FLOOR PLAN
A2.1 1/4" = 1'-0"

