



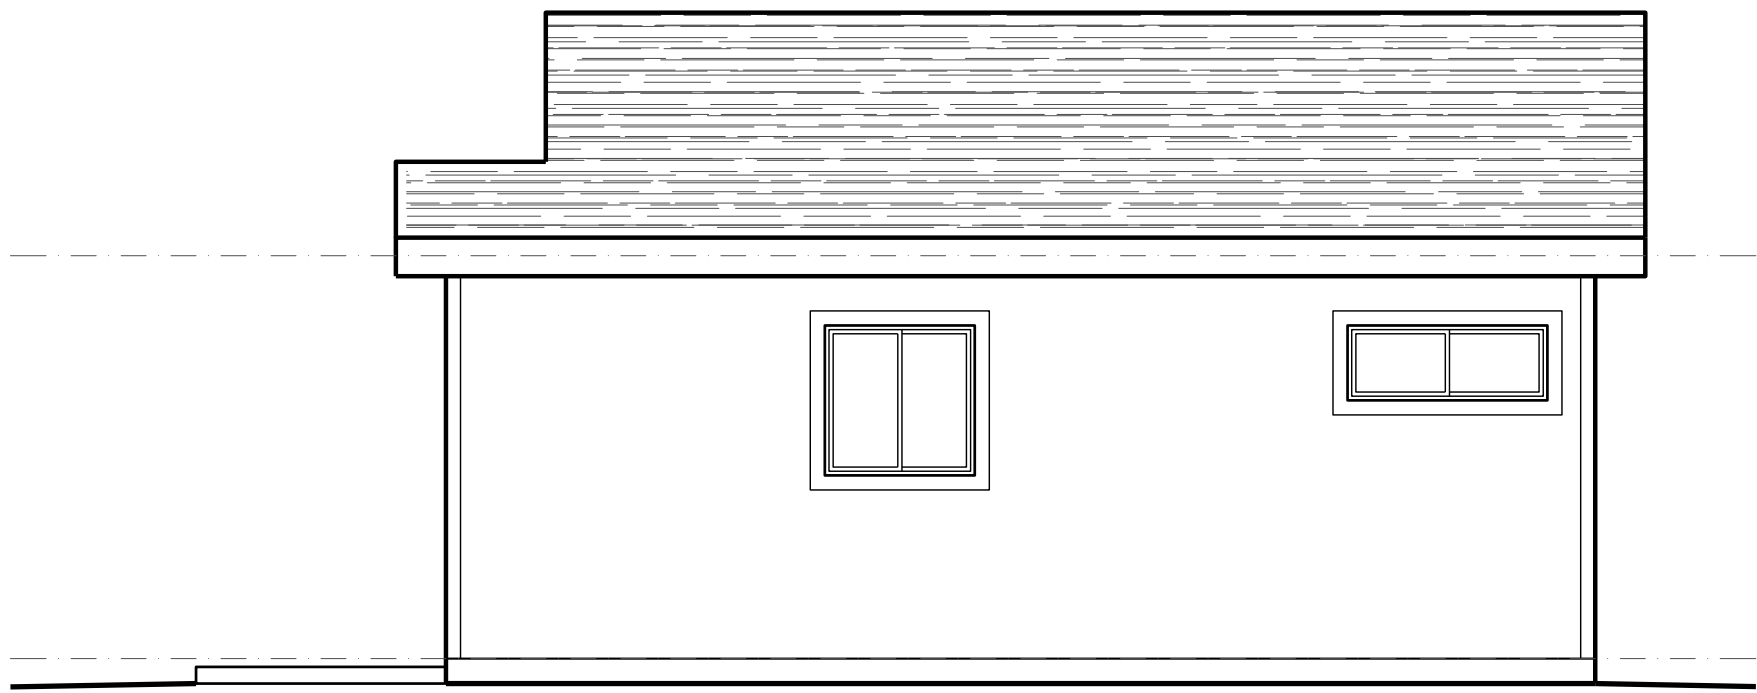


C REAR ELEVATION

A2.1 1/4" = 1'-0"

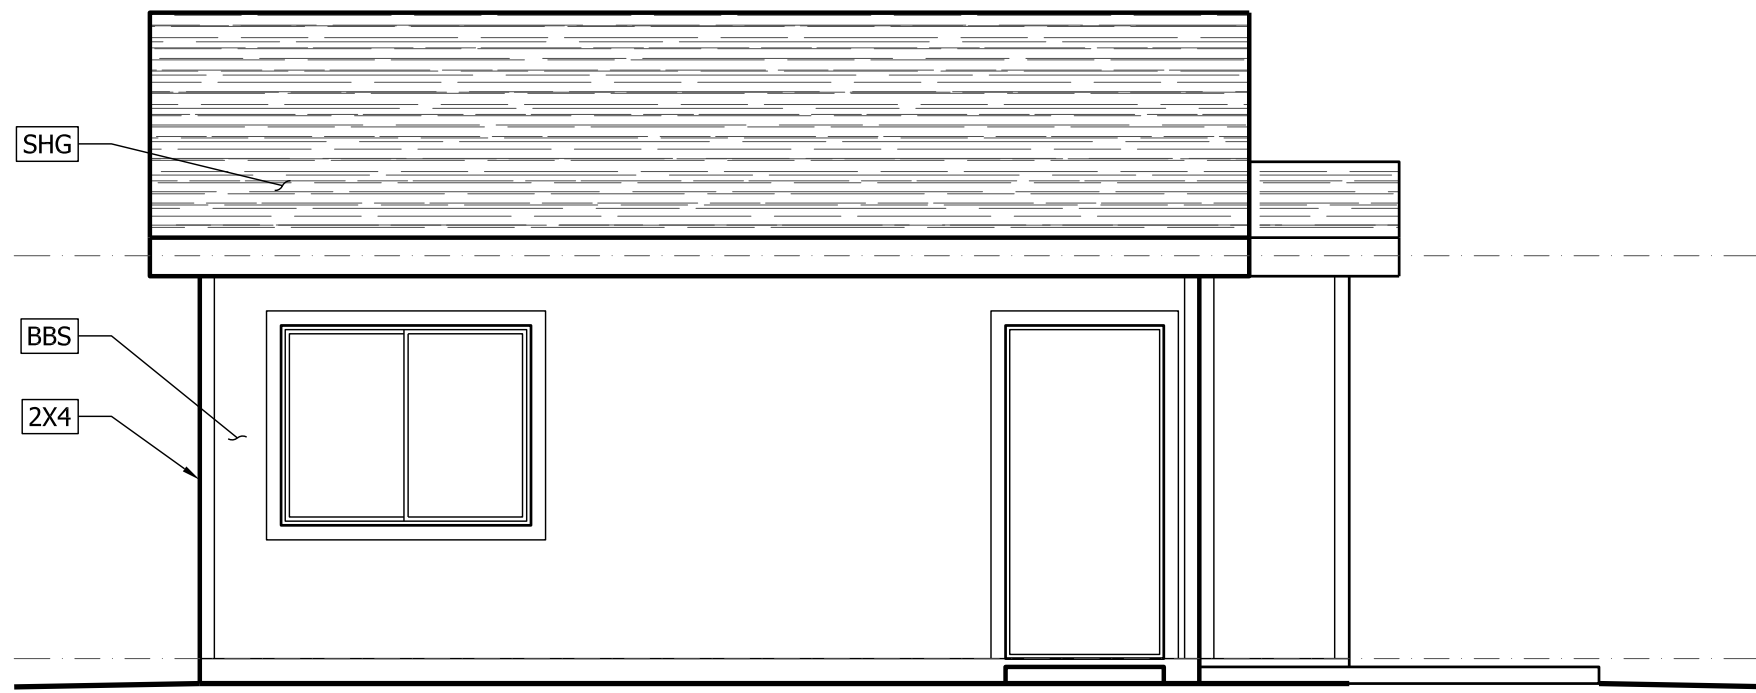


A FRONT ELEVATION

A2.1 1/4" = 1'-0"

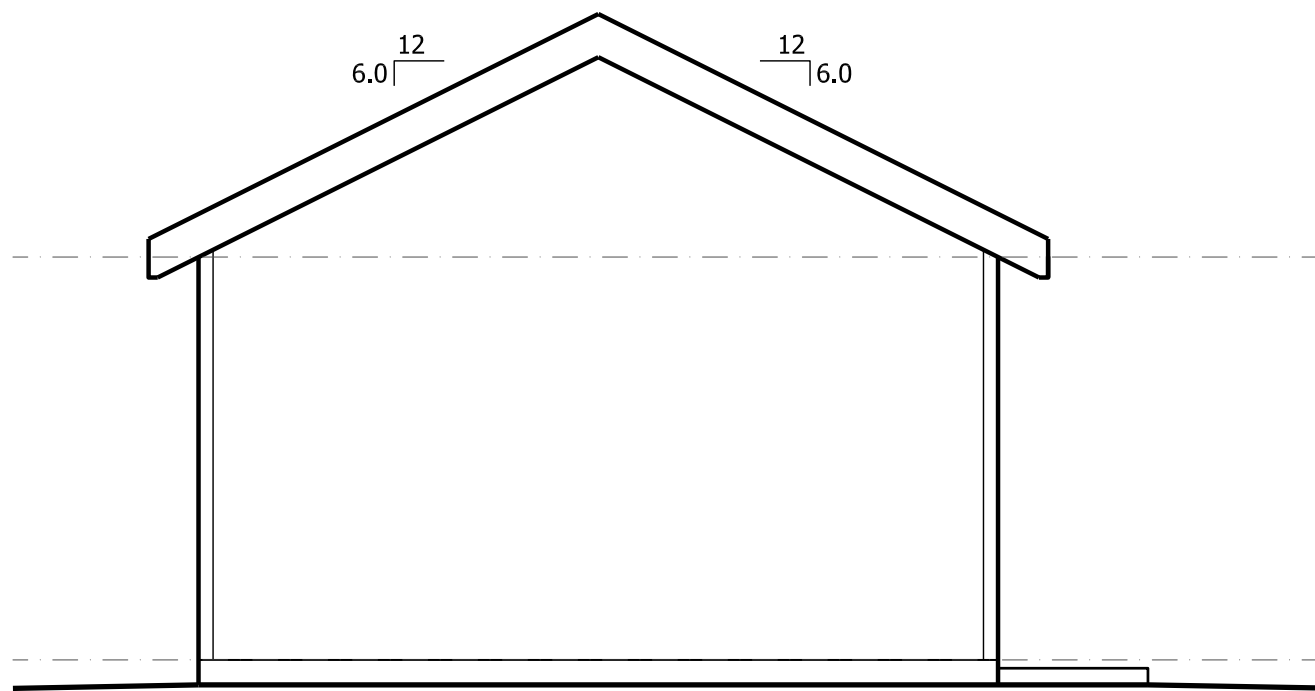

D LEFT ELEVATION

A2.1 1/4" = 1'-0"

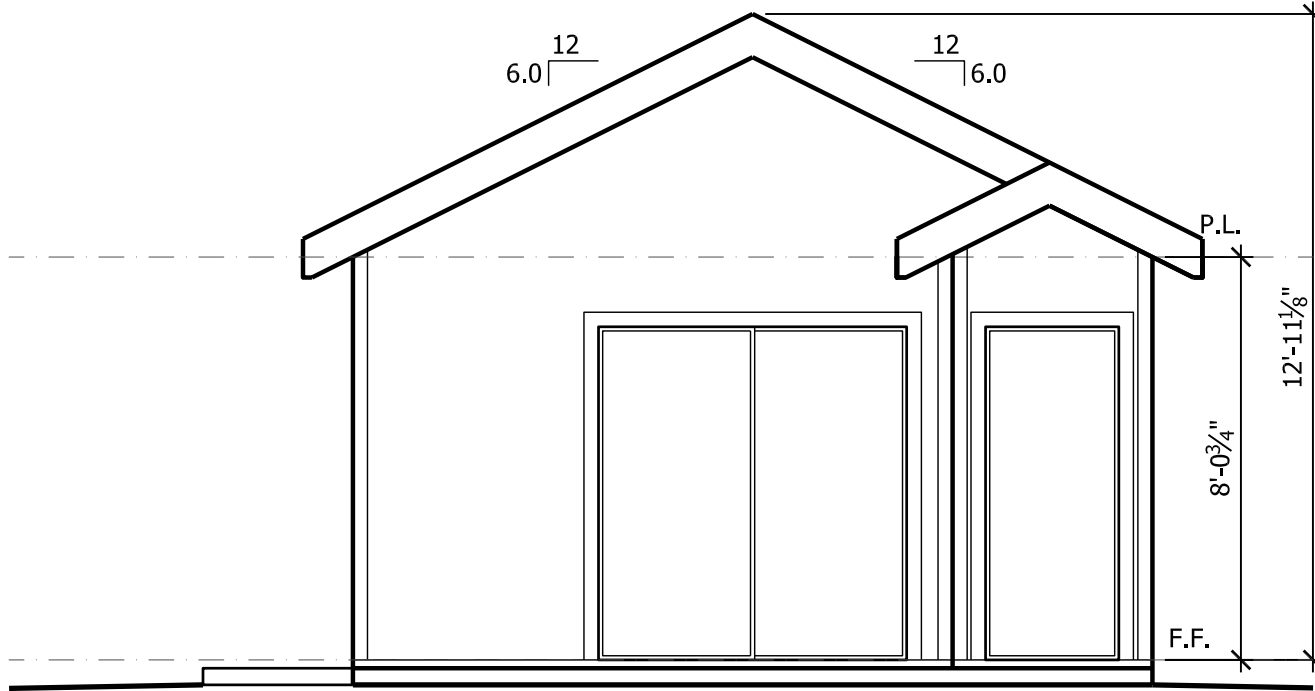

B RIGHT ELEVATION

A2.1 1/4" = 1'-0"


DOOR AND FRAME SCHEDULE

NUMBER	SIZE	STYLE	FIRE RATING	NOTES
1	3'-0" x 6'-8" x 1-3/4"	SINGLE - EXTERIOR	--	--
2	PR 3'-0" x 6'-8" x 1-1/4"	SLIDING - EXTERIOR	--	--
3	2'-6" x 6'-8" x 1-3/4"	SINGLE - INTERIOR	--	--
4	2'-6" x 6'-8" x 1-3/4"	SINGLE - INTERIOR	--	--
5	2'-6" x 6'-8" x 1-3/4"	SINGLE - EXTERIOR	--	--

WINDOW SCHEDULE

NUMBER	SIZE	STYLE	HEAD HEIGHT	SHCG	U-FACTOR	NOTES
	WIDTH	HEIGHT				
1	5'-0"	4'-0"	SLIDER	6'-8"	.23	.30
2	4'-0"	1'-6"	SLIDER	6'-8"	.23	.30 FROSTED
3	3'-0"	3'-0"	SLIDER	6'-8"	.23	.30

REFERENCE KEYNOTES	
DIVISION 03 - CONCRETE	
CL	4" THICK CONCRETE LANDING, MINIMUM 3'-0" DEEP x DOOR WIDTH. LANDING SHALL NOT EXCEED 1/4 UNIT VERTICAL IN 12 UNITS HORIZONTAL (2%)
DIVISION 07 - THERMAL AND MOISTURE PROTECTION	
ROOFING AND SIDING -	
SHG	CLASS 'A' LIFETIME COMPOSITION ROOF SHINGLES o/ 15LB FELT COMPLIANT WITH TABLE R905.1(1). FASTEN ROOFING WITH CORROSION RESISTANT FASTENERS CRC R905.2.5
DIVISION 09 - FINISHES	
2X4	2X4 TRIM
BBS	5/8" T1-11 BOARD AND BATTEN SIDING o/ TWO LAYER GRADE 'D' PAPER OR 1 LAYER TYVEK. NAILING PER STRUCTURAL
FLOORING -	
LVF	LUXURY VINYL FLOORING
DIVISION 11 - EQUIPMENT	
DW18	18" DISHWASHER
FR30	FRIDGE, 30" WIDE
MWEH	MICROWAVE EXHAUST HOOD COMBINATION, MIN VENTILATION RATE OF 100 CFM (CMC TABLE 403.7), HVI RATED & LIMITED TO 3 SONES, HERS VERIFICATION REQUIRED
RG30-E	30" RANGE - ELECTRIC
WD	STACKED WASHER AND DRYER, PROVIDE MIN 2" STANDPIPE
DIVISION 12 - FURNISHINGS	
BC24	24" DEEP BASE CABINET
UC12	12" DEEP UPPER CABINET
UC24	24" DEEP UPPER CABINET
DIVISION 15 - MECHANICAL	
40HPE	40 GALLON HYBRID HEAT PUMP ELECTRIC HOT WATER HEATER, DRAIN TO EXTERIOR
MSH	MINI SPLIT HEAD
MSU	MINI SPLIT OUTDOOR UNIT, INSTALLED PER MANUFACTURER SPECIFICATIONS
DIVISION 16 - ELECTRICAL	
EPP	ELECTRICAL SUB PANEL, 120/240V 125A, W/ UFER GROUND
DIVISION 17 - PLUMBING	
BC-S	BATHTUB SHOWER COMBO
KS-U24	UNDERMOUNT KITCHEN SINK, 24"
SK24	SINK w/VANITY 24"
WC	WATER CLOSET, MINIMUM 30" CLEAR WIDTH CENTERED ON WATER CLOSET & 24" CLEAR SPACE OFF NOSE OF WATER CLOSET.

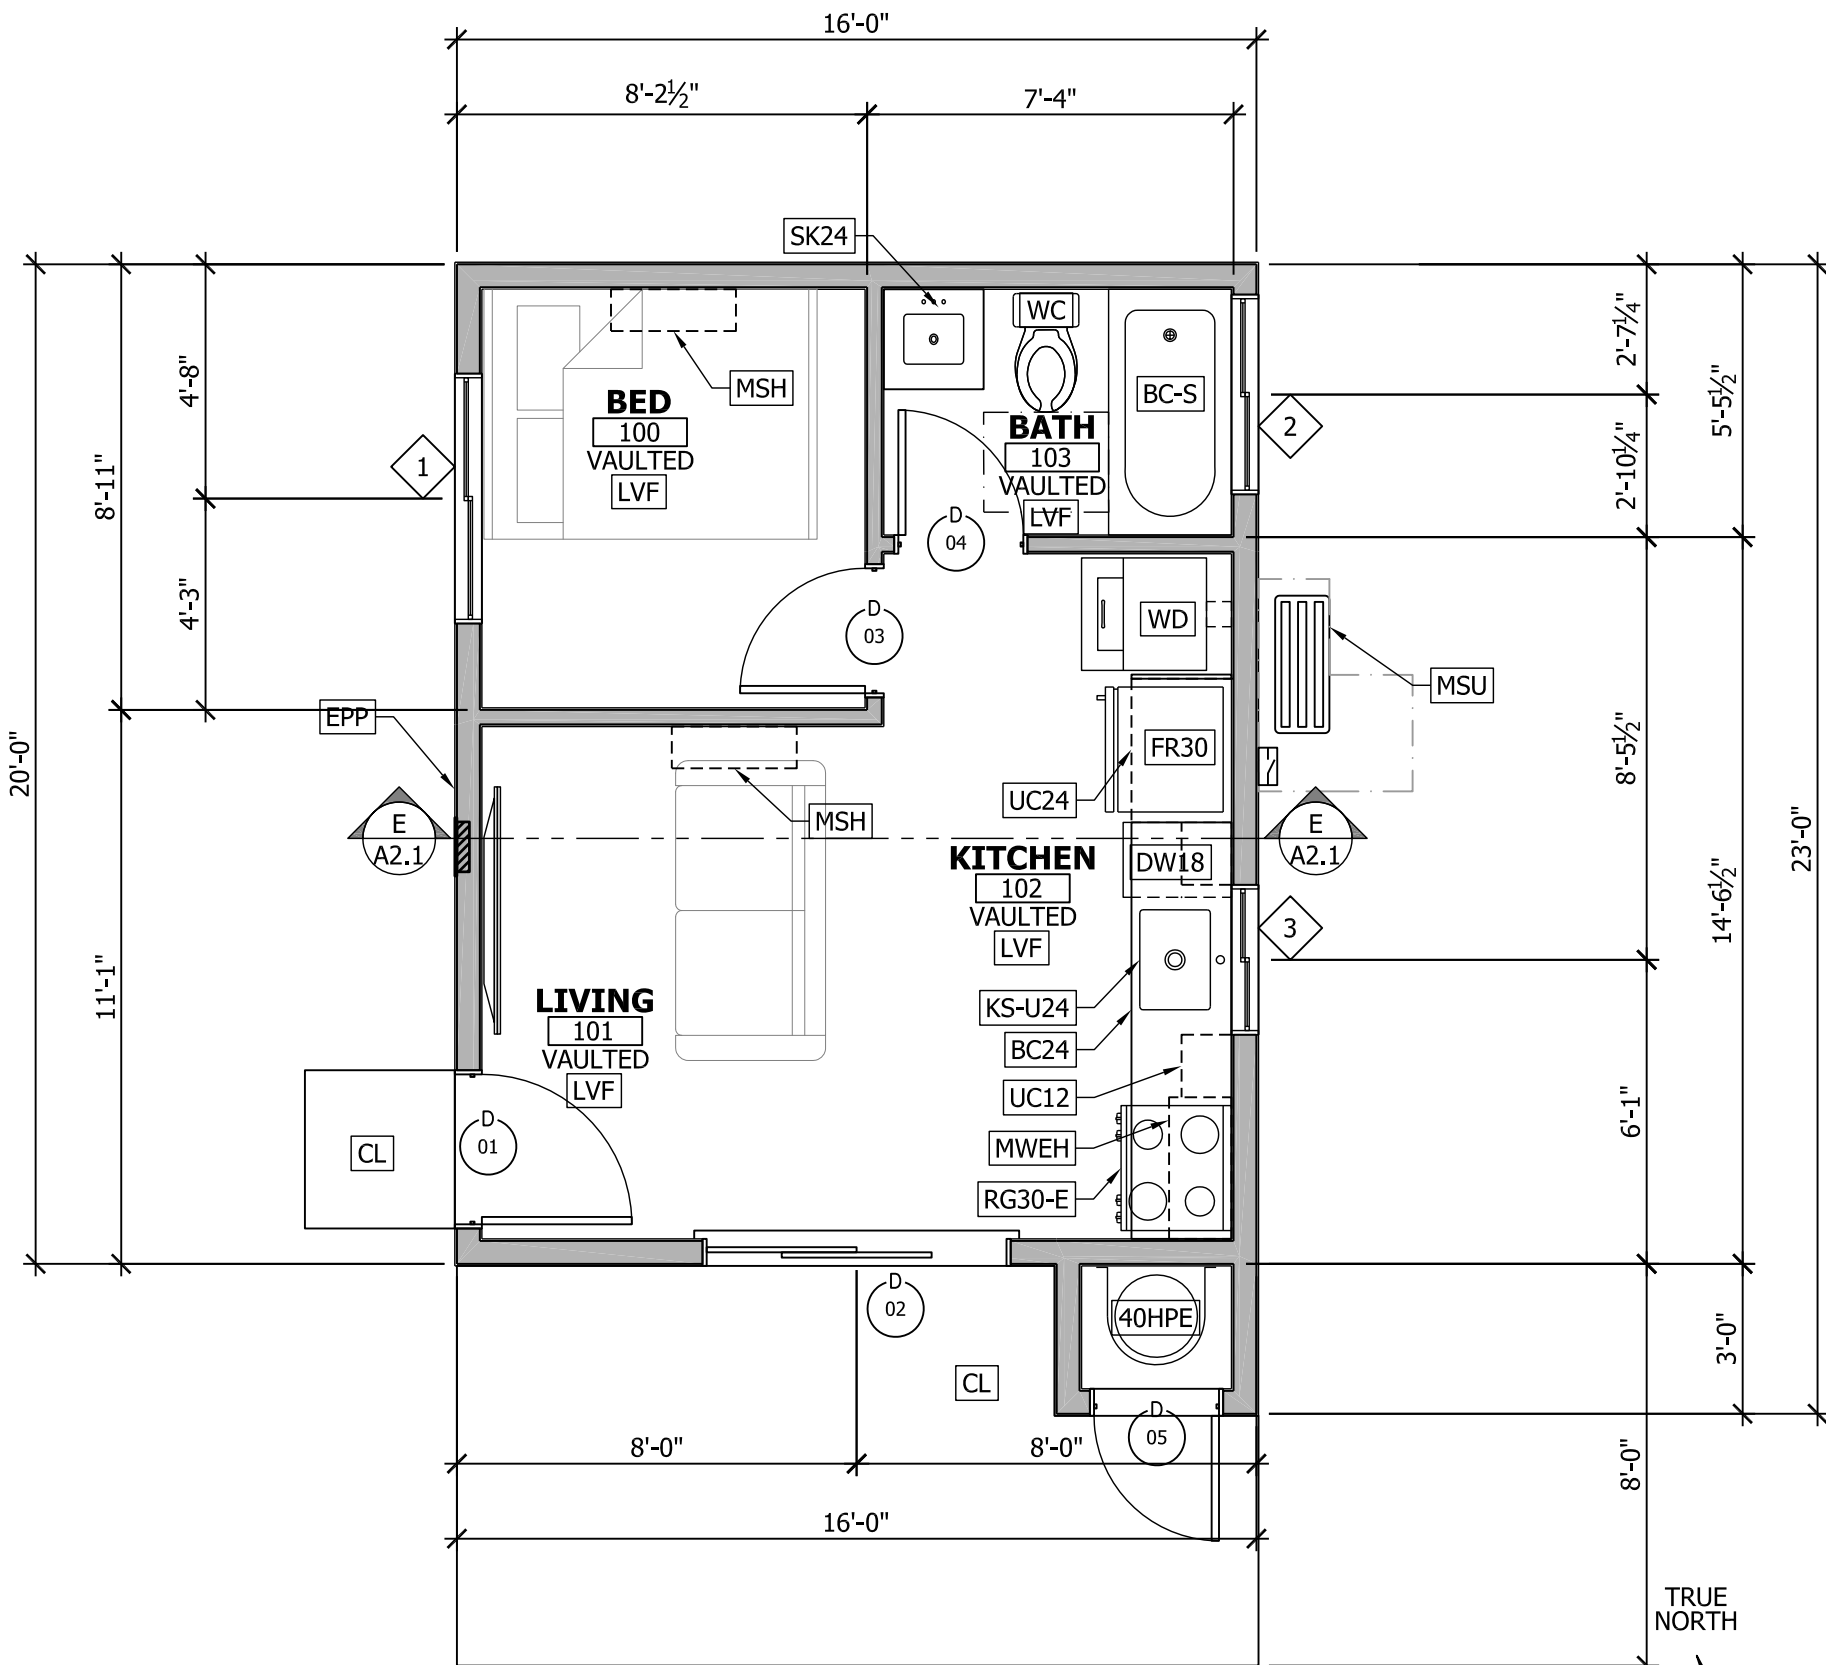

1 FLOOR PLAN #1

A2.1 1/4" = 1'-0"

320 SF LIVING
12 SF STORAGE

