



REFERENCE KEYNOTES	
DIVISION 03 - CONCRETE	
CL	- 4" THICK CONCRETE LANDING, MINIMUM 3'-0" DEEP x DOOR WIDTH. LANDING SHALL NOT EXCEED 1/4 UNIT VERTICAL IN 12 UNITS HORIZONTAL (2%)
DIVISION 06 - WOOD AND PLASTICS	
MISCELLANEOUS -	
WT24	- 2x4 WOOD TRIM
DIVISION 07 - THERMAL AND MOISTURE PROTECTION	
ROOF ACCESSORIES -	
AA	- 22"x30" ATTIC ACCESS, PERMANTLY ATTACH INSULATION USING ADHESIVE OR MECHANICAL FASTENERS TO ACCESS PANEL. ACCESS SHALL BE GASKETED TO PREVENT AIR LEAKAGE
ROOFING AND SIDING -	
SHG	- CLASS 'A' LIFETIME COMPOSITION ROOF SHINGLES o/ 15LB FELT COMPLIANT WITH TABLE R905.1(1). FASTEN ROOFING WITH CORROSION RESISTANT FASTENERS CRC R905.2.5
DIVISION 09 - FINISHES	
BBS	- 5/8" T1-11 BOARD AND BATTEN SIDING o/ TWO LAYER GRADE 'D' PAPER OR 1 LAYER TYVEK. NAILING PER STRUCTURAL
FLOORING -	
LAM	- LAMINATE FLOORING
DIVISION 11 - EQUIPMENT	
DW24	- 24" DISHWASHER
FR36	- FRIDGE, 36" WIDE
MWEH	- MICROWAVE EXHAUST HOOD COMBINATION, MIN VENTILATION RATE OF 100 CFM (CMC TABLE 403.7), HVI RATED & LIMITED TO 3 SONES, HERS VERIFICATION REQUIRED
RG30-E	- 30" RANGE - ELECTRIC
WD	- STACKED WASHER AND DRYER, PROVIDE MIN 2" STANDPIPE
DIVISION 12 - FURNISHINGS	
BC24	- 24" DEEP BASE CABINET
UC12	- 12" DEEP UPPER CABINET
DIVISION 13 - SPECIAL CONSTRUCTION	
PS	- CLOSET POLE & SHELF
DIVISION 15 - MECHANICAL	
MSH	- MINI SPLIT HEAD
MSU	- MINI SPLIT OUTDOOR UNIT, INSTALLED PER MANUFACTURER SPECIFICATIONS
WH-E	- WATER HEATER, ELECTRIC
DIVISION 16 - ELECTRICAL	
EPP	- ELECTRICAL SUB PANEL, 120/240V 125A, W/ UFER GROUND, PROVIDE 30"x30" WORKING AREA CENTERED IN FRONT OF PANEL
DIVISION 17 - PLUMBING	
KS	- KITCHEN SINK
SK48	- SINK w/VANITY 48"
TS35	- TILE SHOWER 3x5
WC	- WATER CLOSET, MINIMUM 30" CLEAR WIDTH CENTERED ON WATER CLOSET & 24" CLEAR SPACE OFF NOSE OF WATER CLOSET.

WINDOW SCHEDULE							
NUMBER	SIZE		STYLE	HEAD HEIGHT	SHCG	U-FACTOR	NOTES
	WIDTH	HEIGHT					
1	4'-0"	3'-0"	SLIDER	6'-8"	.23	.30	--
2	4'-0"	4'-0"	SLIDER	6'-8"	.23	.30	--
3	4'-0"	4'-0"	SLIDER	6'-8"	.23	.30	TEMP
4	4'-0"	3'-0"	SLIDER	6'-8"	.23	.30	--
5	2'-0"	3'-0"	SINGLE HUNG	6'-8"	.23	.30	FROSTED
6	3'-0"	3'-0"	SLIDER	6'-8"	.23	.30	--
7	2'-0"	3'-0"	SINGLE HUNG	6'-8"	.23	.30	FROSTED


DOOR AND FRAME SCHEDULE				
NUMBER	SIZE	STYLE	FIRE RATING	NOTES
1	3'-0" x 6'-8" x 1-3/4"	SINGLE - EXTERIOR	--	--
2	3'-0" x 6'-8" x 1-3/4"	SINGLE - INTERIOR	--	--
3	3'-0" x 6'-8" x 1-3/4"	SINGLE - EXTERIOR	--	--
4	3'-0" x 6'-8" x 1-3/4"	SINGLE - EXTERIOR	--	--
5	2'-6" x 6'-8" x 1-3/4"	SINGLE - INTERIOR	--	--
6	2'-4" x 6'-8" x 1-3/4"	POCKET	--	--
7	2'-6" x 6'-8" x 1-3/4"	SINGLE - EXTERIOR	--	--
8	2'-6" x 6'-8" x 1-3/4"	POCKET	--	--
9	PR 3'-0" x 6'-8" x 1-3/4"	HORIZONTAL BYPASS	--	--
10	2'-6" x 6'-8" x 1-3/4"	POCKET	--	--

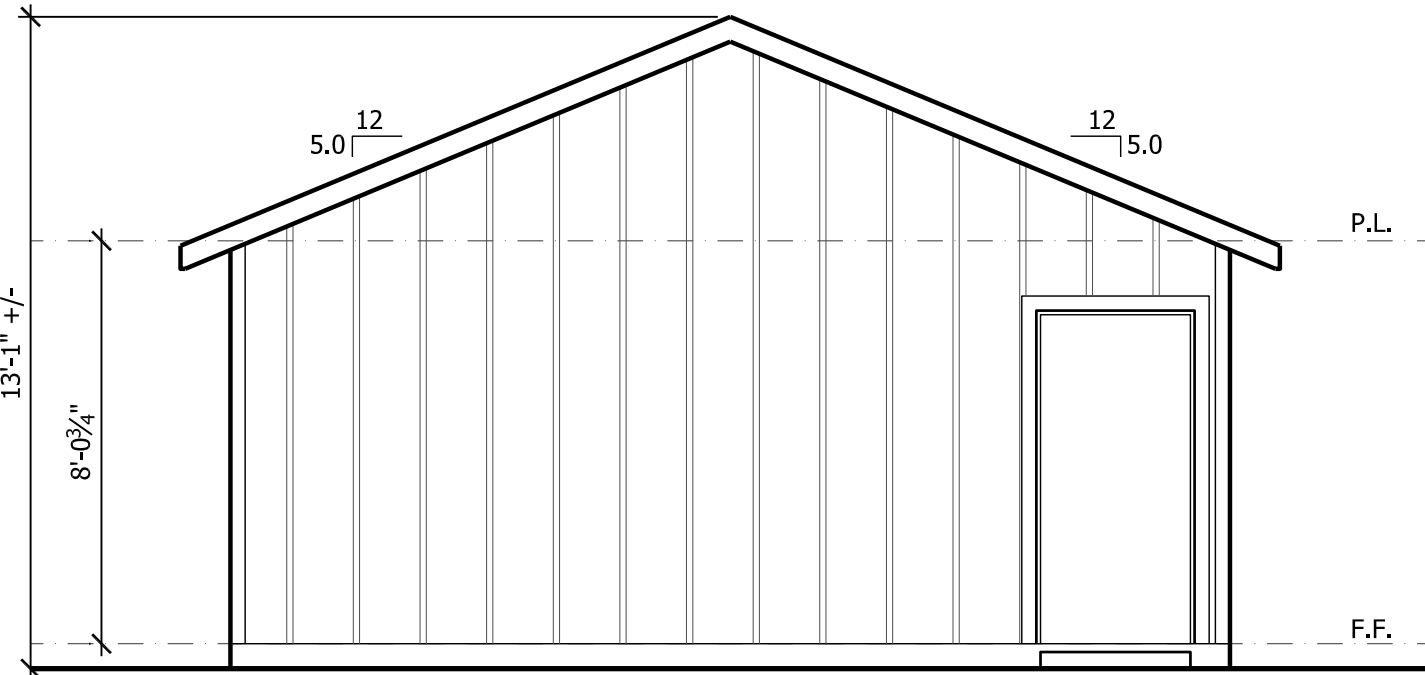


C LEFT ELEVATION
1 1/4" = 1'-0"

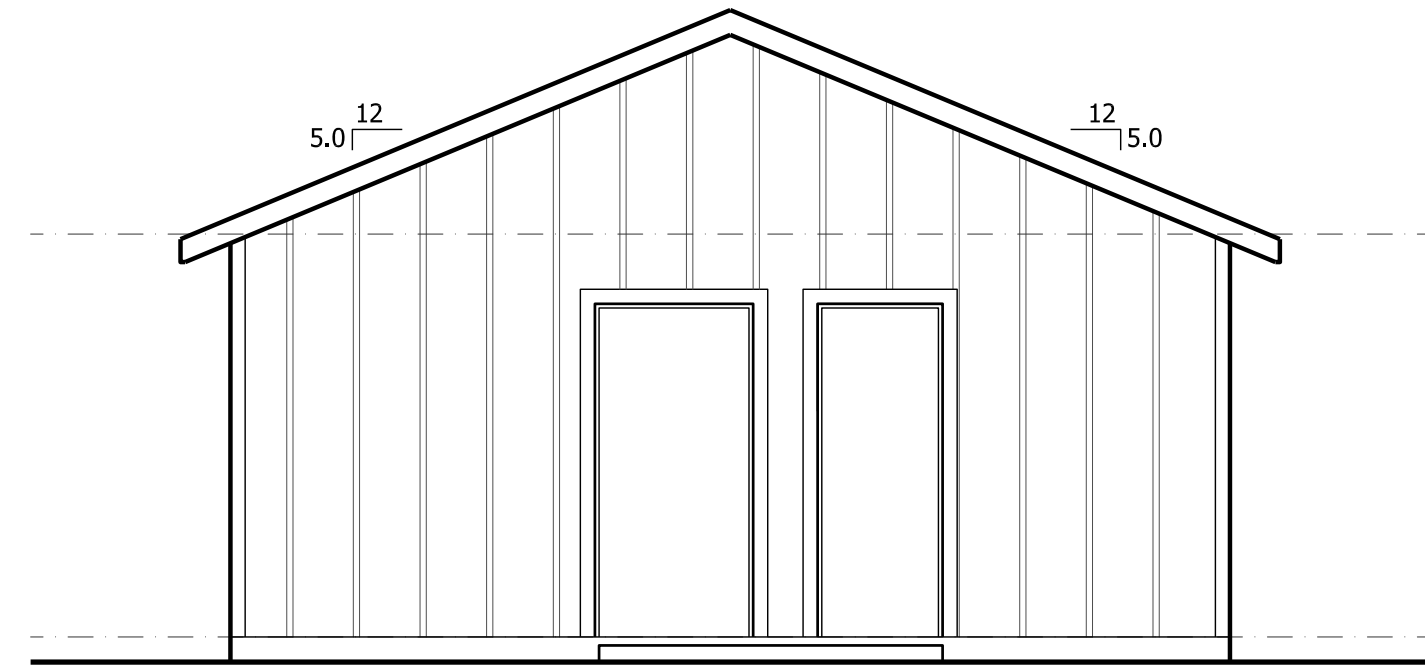


D RIGHT ELEVATION
1 1/4" = 1'-0"

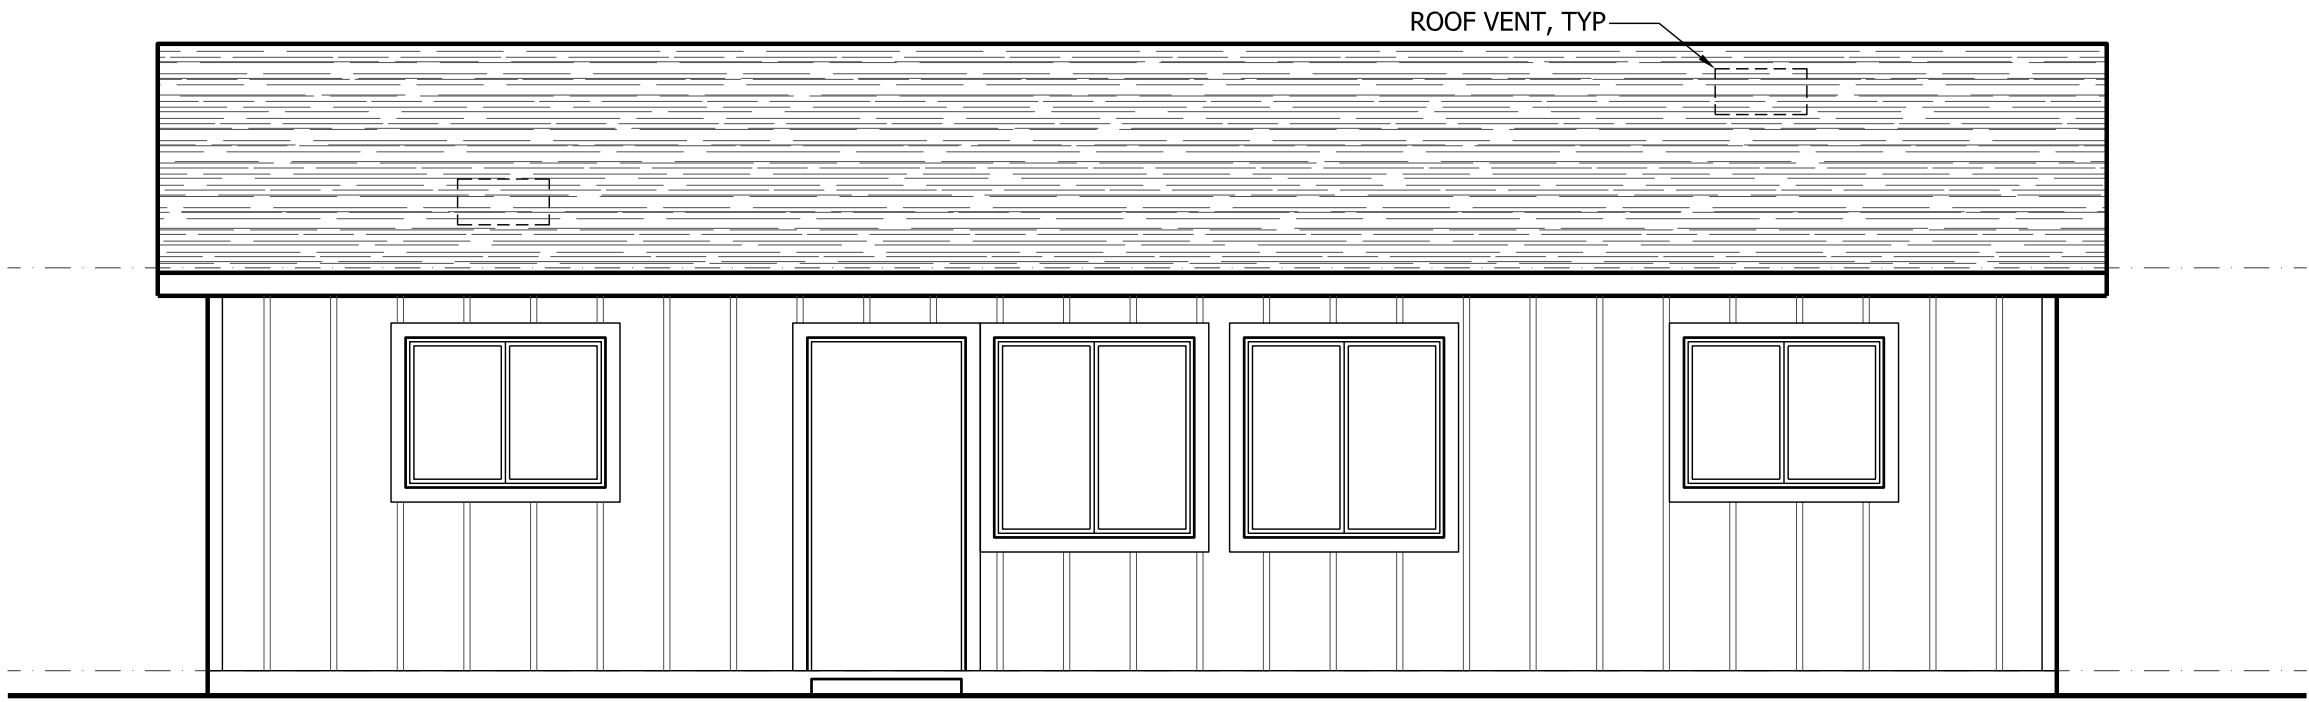

A FRONT ELEVATION
1 1/4" = 1'-0"

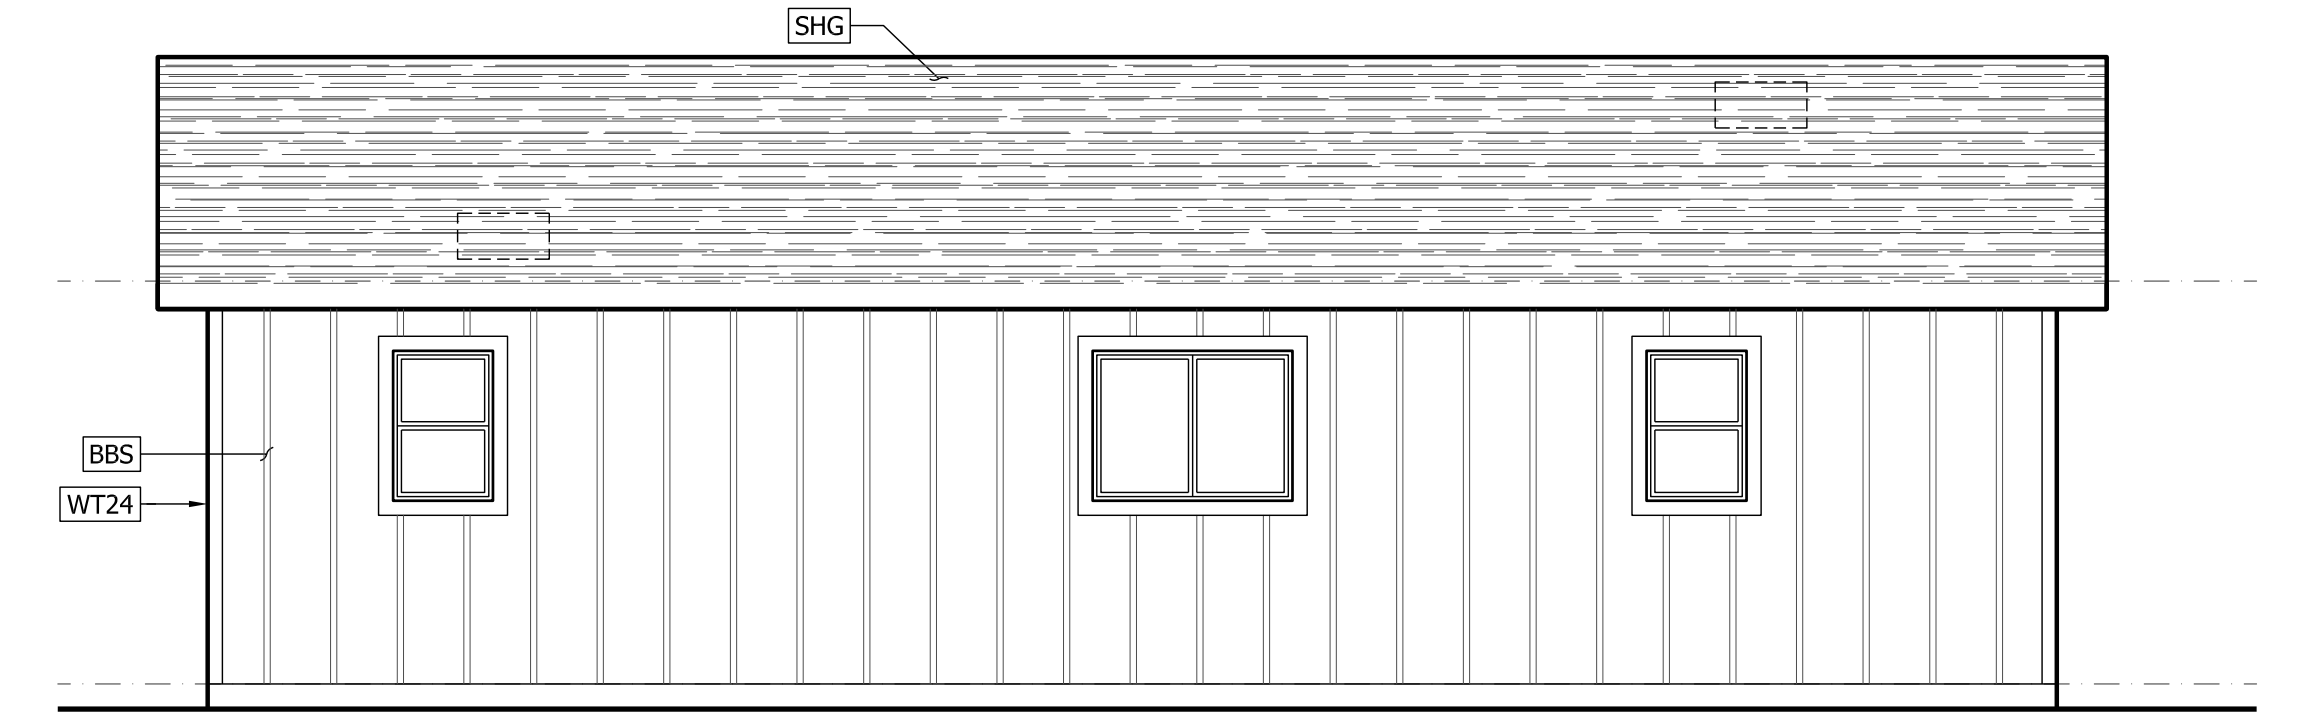

B REAR ELEVATION
1 1/4" = 1'-0"

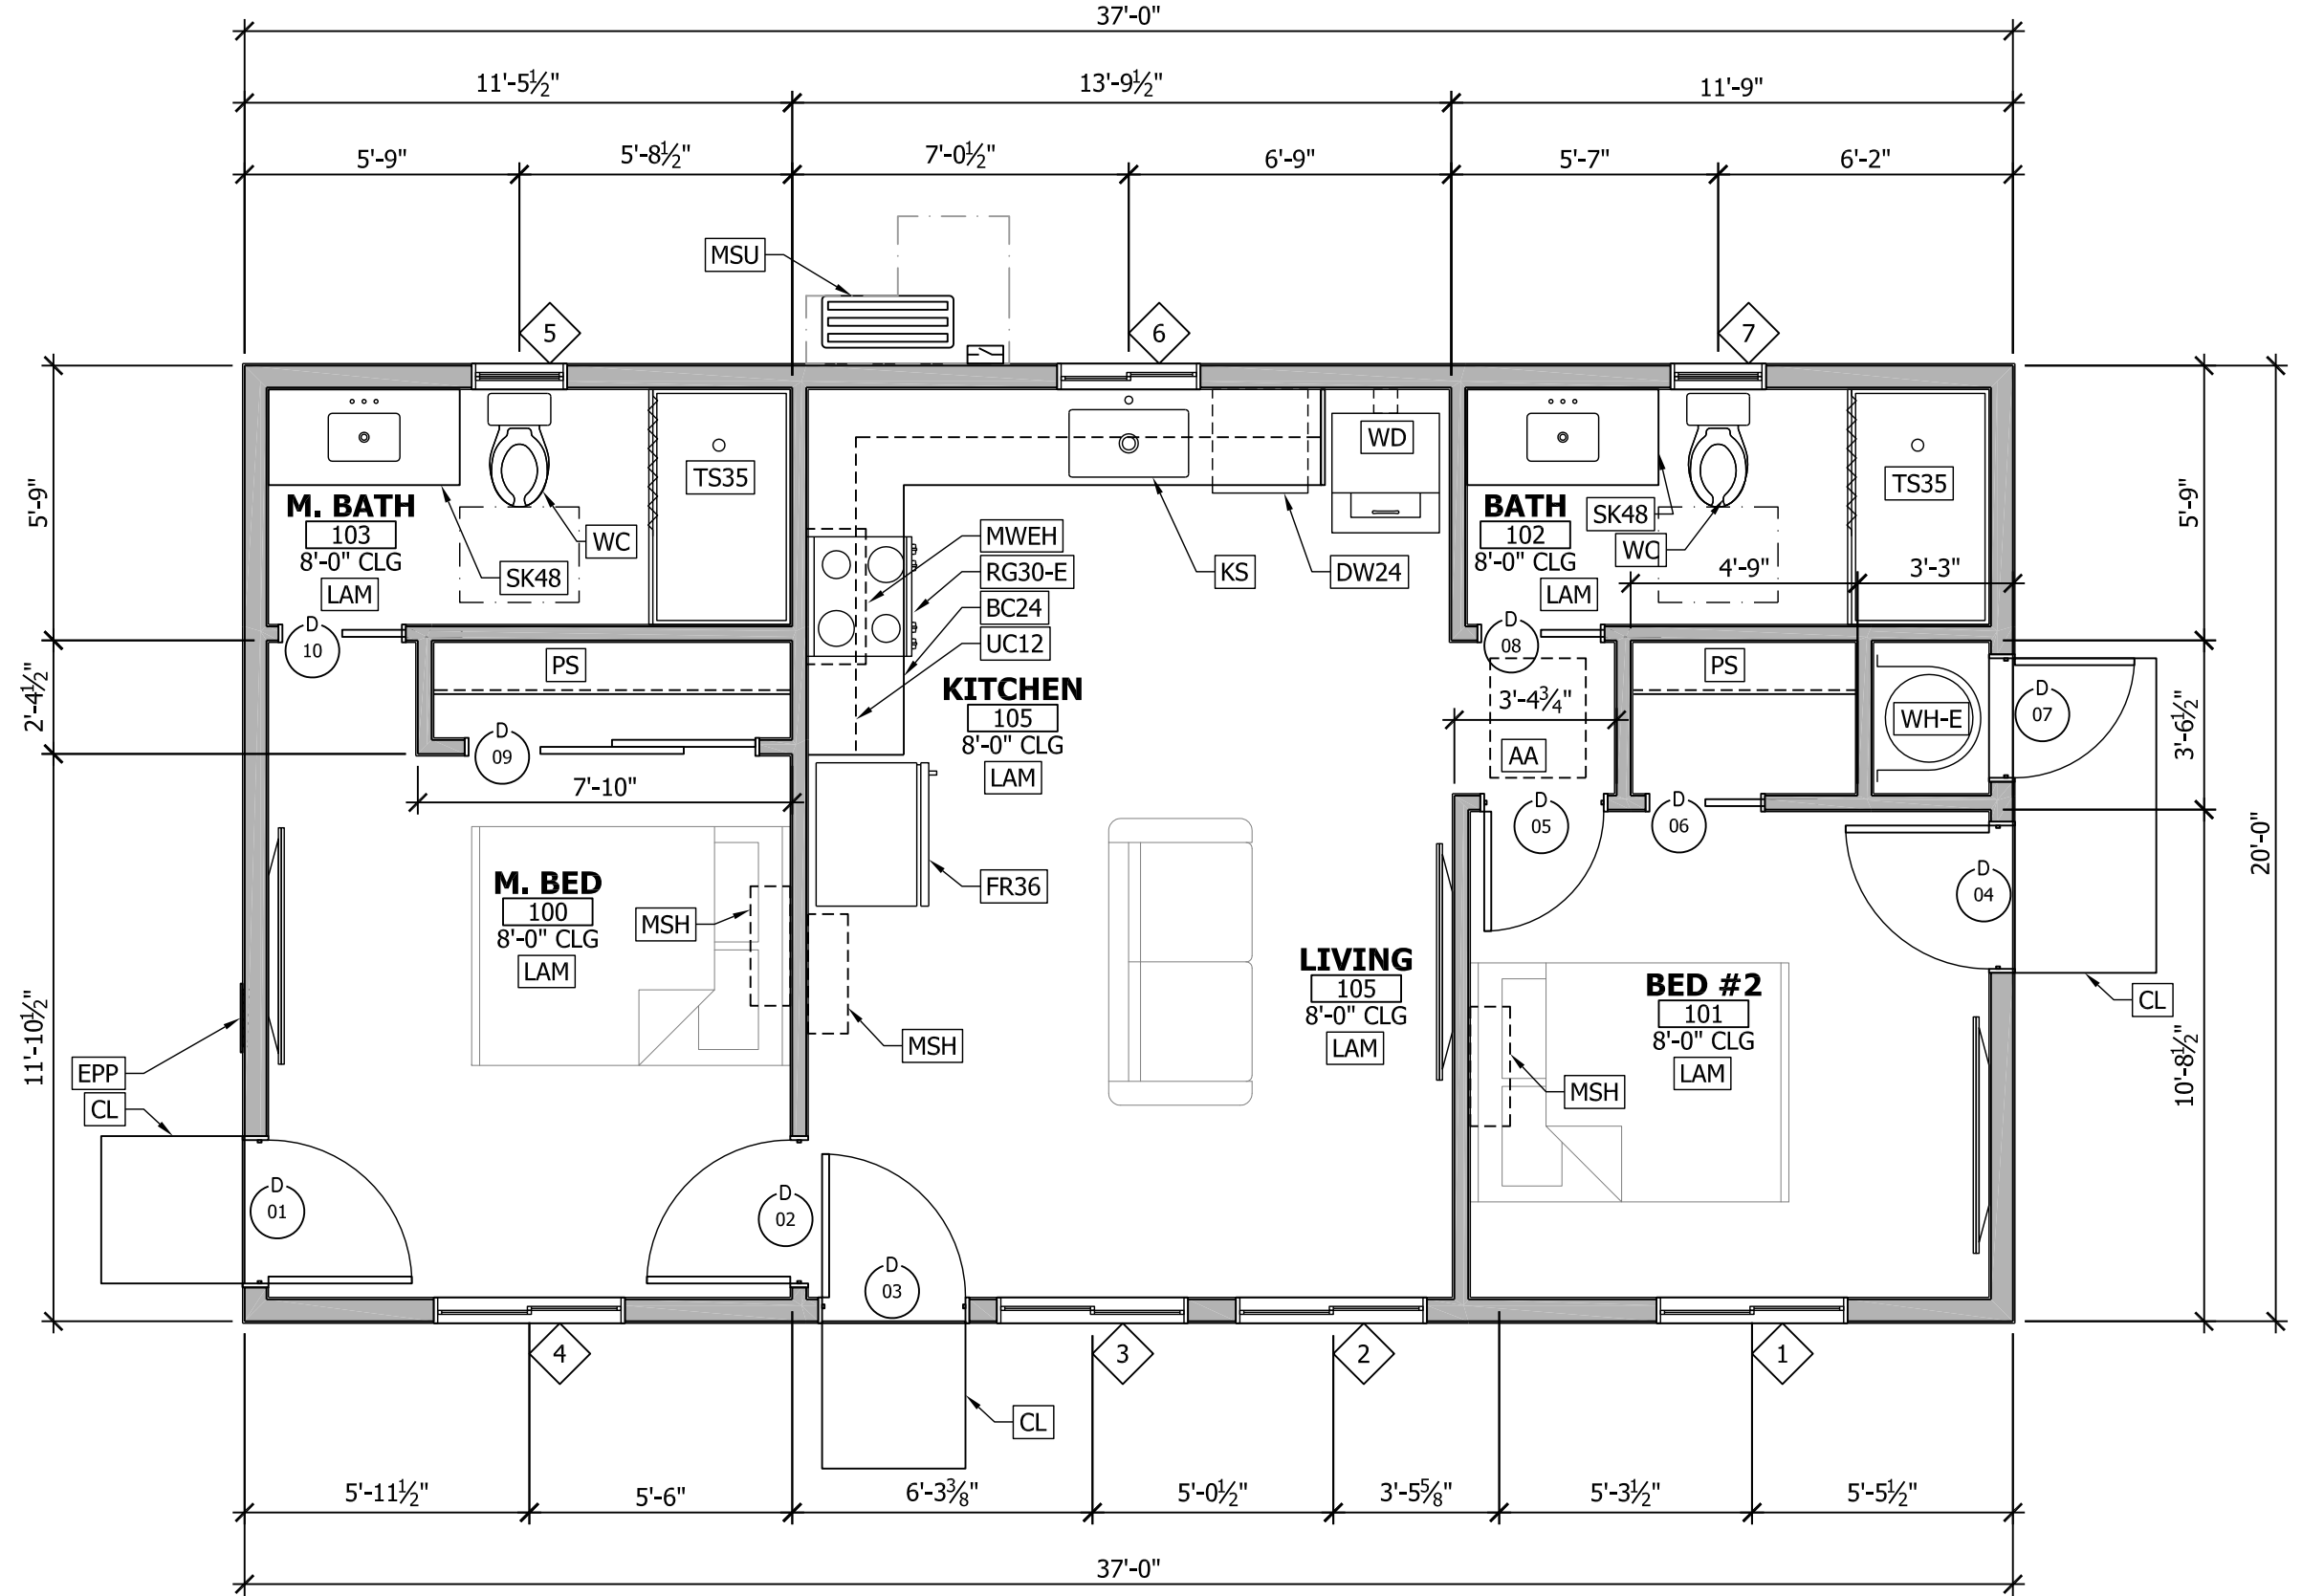

1 FLOOR PLAN
1 1/4" = 1'-0"

