



WINDOW SCHEDULE						
NUMBER	SIZE		STYLE	HEAD HEIGHT	SHCG	NOTES
	WIDTH	HEIGHT				
1	5'-0"	5'-0"	SLIDER	6'-8"	.23	TEMP
2	5'-0"	5'-0"	SLIDER	6'-8"	.23	
3	5'-0"	4'-0"	SLIDER	6'-8"	.23	
4	2'-0"	3'-0"	SINGLE HUNG	6'-8"	.23	
5	3'-0"	3'-0"	SLIDER	6'-8"	.23	
6	6'-0"	4'-0"	SLIDER	6'-8"	.23	
7	5'-0"	4'-0"	SLIDER	6'-8"	.23	
8	8'-0"	2'-0"	PICTURE	10'-0"	.23	

DOOR AND FRAME SCHEDULE			
NUMBER	SIZE	STYLE	NOTES
1	3'-0" x 6'-8" x 1-3/4"	SINGLE - EXTERIOR	--
2	3'-0" x 6'-8" x 1-3/4"	SINGLE - INTERIOR	--
3	2'-6" x 6'-8" x 1-3/4"	SINGLE - INTERIOR	--
5	2'-8" x 6'-8" x 1-3/4"	SINGLE - INTERIOR	--
6	3'-0" x 6'-8" x 1-3/4"	SINGLE - INTERIOR	--
7	PR 2'-0" x 6'-8" x 1-3/4"	HORIZONTAL BYPASS	--
8	PR 2'-0" x 6'-8" x 1-3/4"	HORIZONTAL BYPASS	--





REFERENCE KEYNOTES	
DIVISION 03 - CONCRETE	
CL	- 4" THICK CONCRETE LANDING, MINIMUM 3'-0" DEEP x DOOR WIDTH. LANDING SHALL NOT EXCEED 1/4 UNIT VERTICAL IN 12 UNITS HORIZONTAL (2%)
DIVISION 09 - FINISHES	
FLOORING -	
LVF	- LUXURY VINYL FLOORING
DIVISION 11 - EQUIPMENT	
DW18	- 18" DISHWASHER
FR30	- FRIDGE, 30" WIDE
REH	- RANGE EXHAUST HOOD/ MICROWAVE, VENTED
RG-E	- RANGE; ELECTRIC
WD	- STACKED WASHER AND DRYER, PROVIDE MIN 2" STANDPIPE
DIVISION 12 - FURNISHINGS	
BC24	- 24" DEEP BASE CABINET
UC12	- 12" DEEP UPPER CABINET
DIVISION 13 - SPECIAL CONSTRUCTION	
PS	- CLOSET POLE & SHELF
DIVISION 15 - MECHANICAL	
IHW-E	- INSTANT HOT WATER HEATER, ELECTRIC
MSU	- MINI SPLIT OUTDOOR UNIT, INSTALLED PER MANUFACTURER SPECIFICATIONS
DIVISION 16 - ELECTRICAL	
ESD	- EQUIPMENT SERVICE DISCONNECT, VERIFY MOTOR POWER REQUIREMENTS PRIOR TO INSTALL
DIVISION 17 - PLUMBING	
BC-S	- BATHTUB SHOWER COMBO
SK-P	- PEDESTAL SINK
SK-U	- UNDERMOUNT SINK
SK-V	- SINK w/ VANITY
WC	- WATER CLOSET, MINIMUM 30" CLEAR WIDTH CENTERED ON WATER CLOSET & 24" CLEAR SPACE OFF NOSE OF WATER CLOSET.

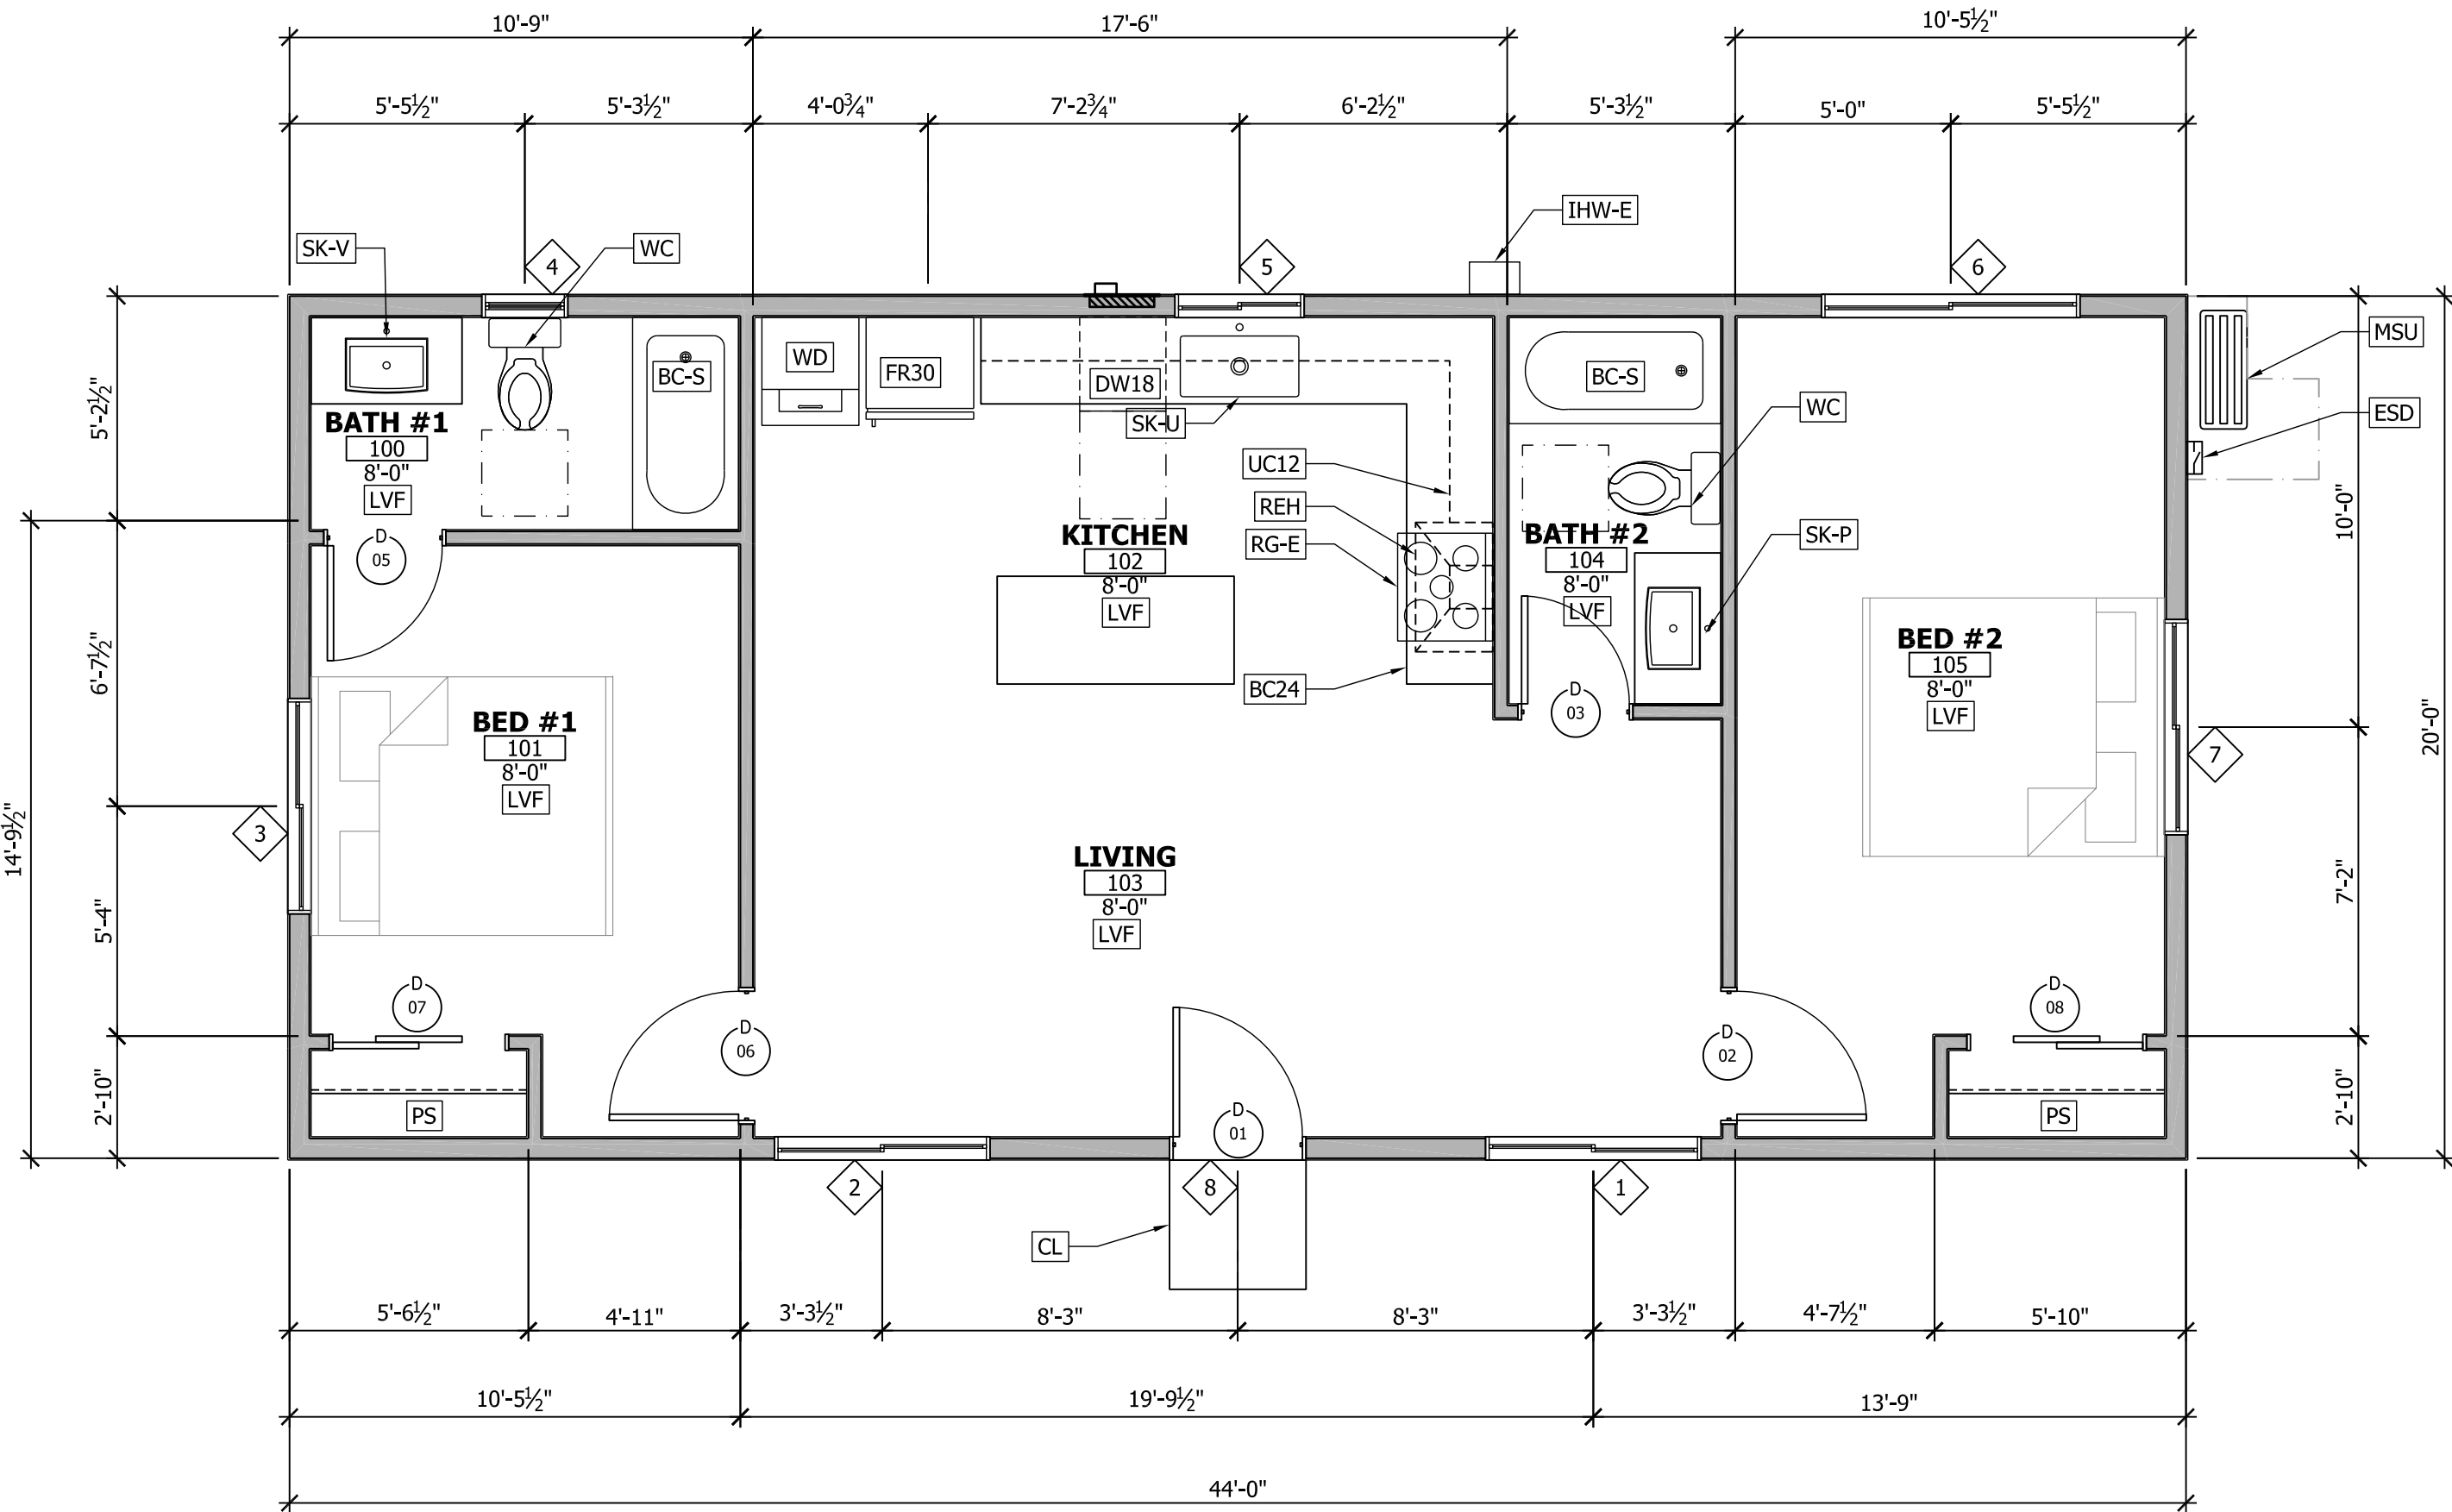

1 FLOOR PLAN
1 1/4" = 1'-0"

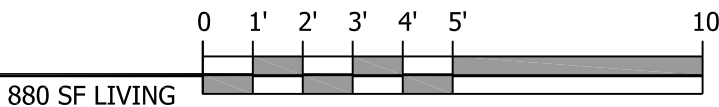

REFERENCE KEYNOTES	
DIVISION 06 - WOOD AND PLASTICS	
MISCELLANEOUS -	
WT24	- 2x4 WOOD TRIM
DIVISION 07 - THERMAL AND MOISTURE PROTECTION	
ROOFING AND SIDING -	
SHG	- CLASS 'A' LIFETIME COMPOSITION ROOF SHINGLES o/ 15LB FELT COMPLIANT WITH TABLE R905.1(1). FASTEN ROOFING WITH CORROSION RESISTANT FASTENERS CRC R905.2.5
DIVISION 09 - FINISHES	
BBS	- 5/8" T1-11 BOARD AND BATTEN SIDING o/ TWO LAYER GRADE 'D' PAPER OR 1 LAYER TYVEK. NAILING PER STRUCTURAL

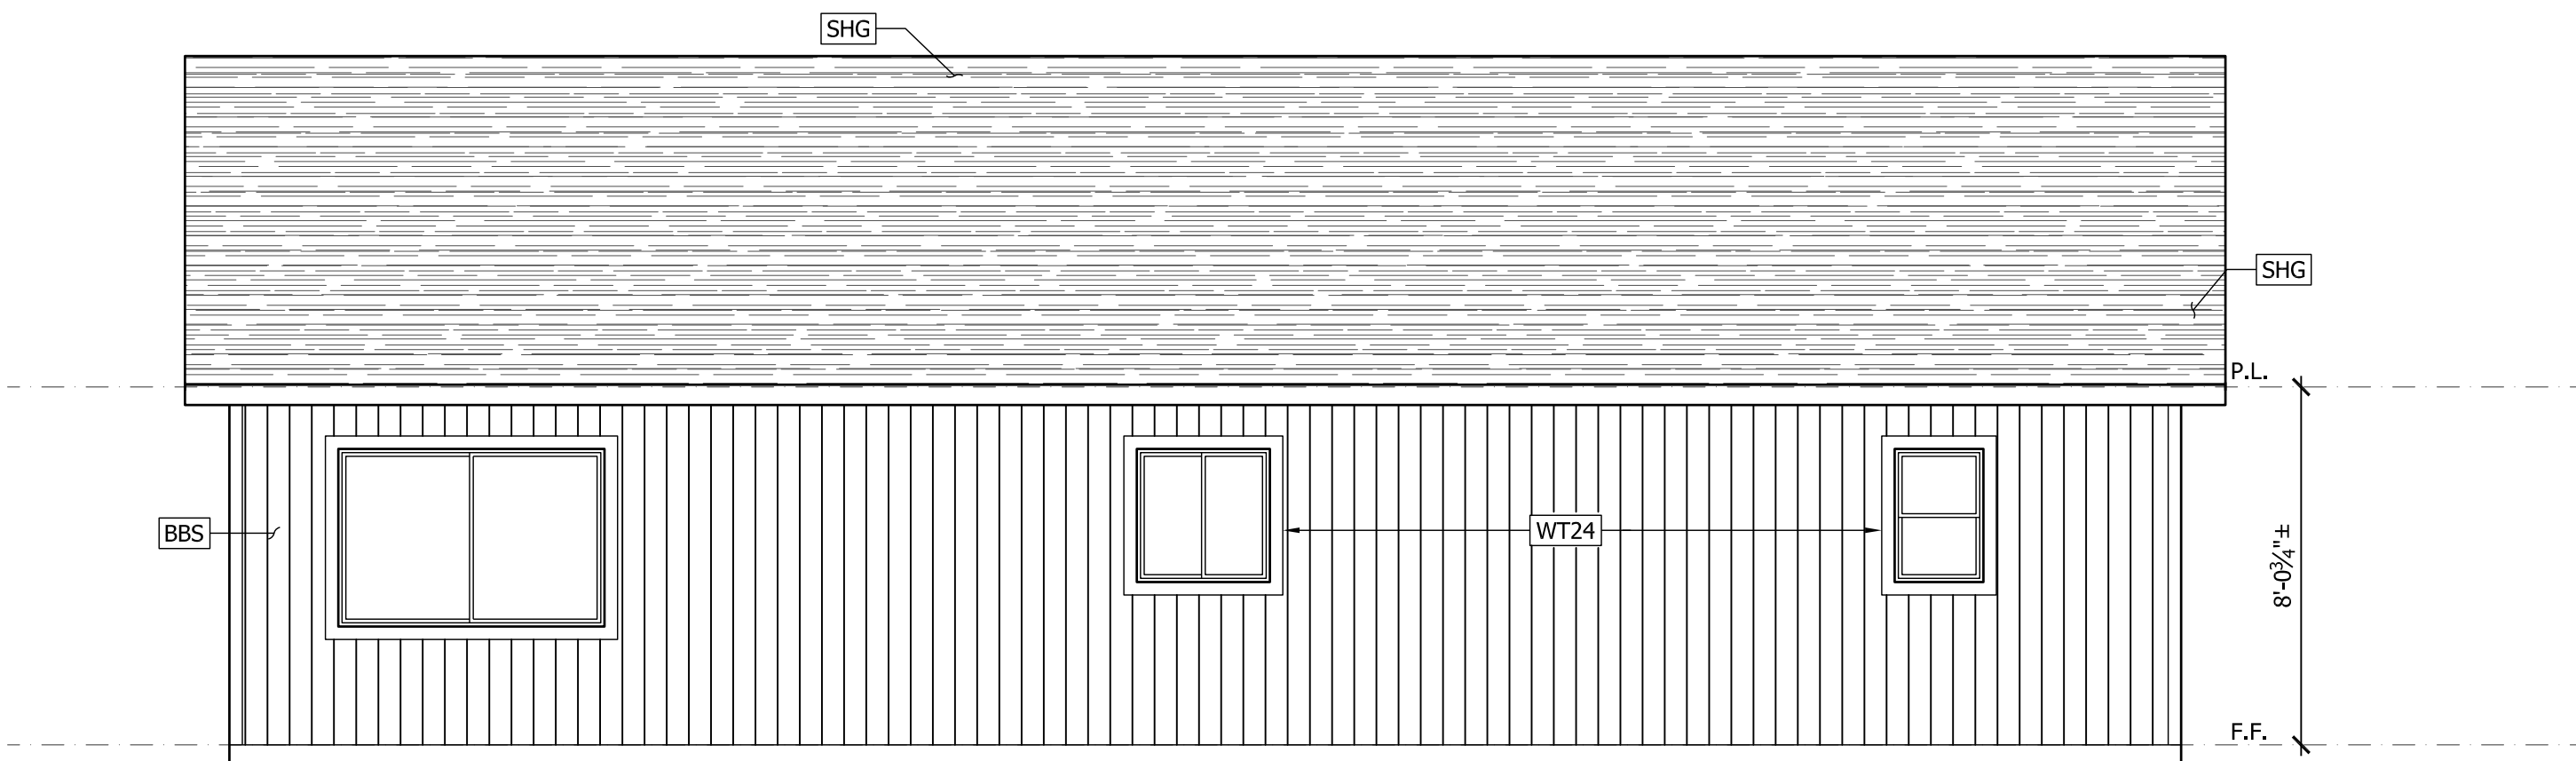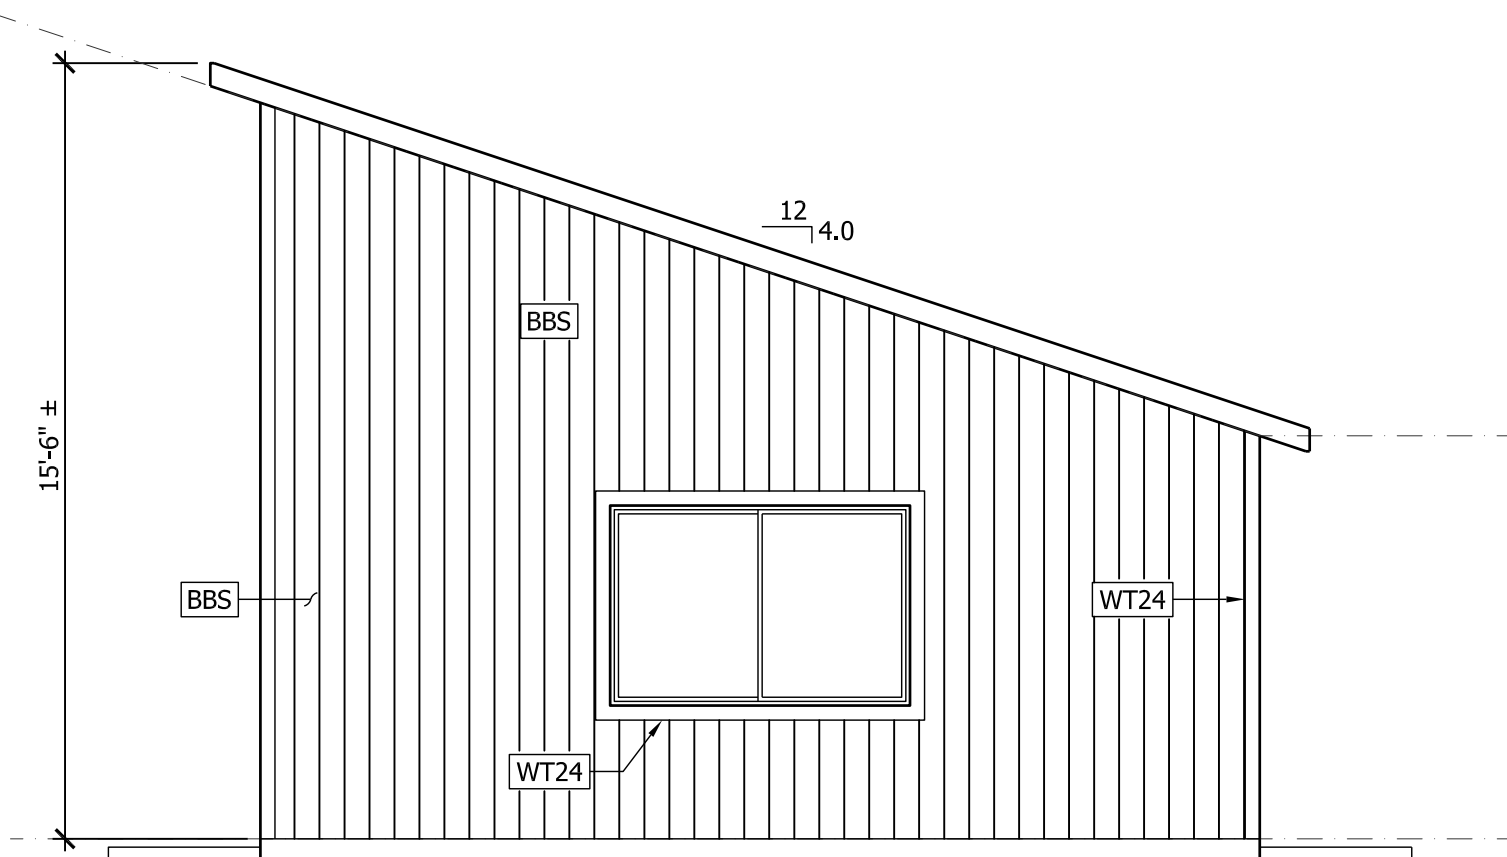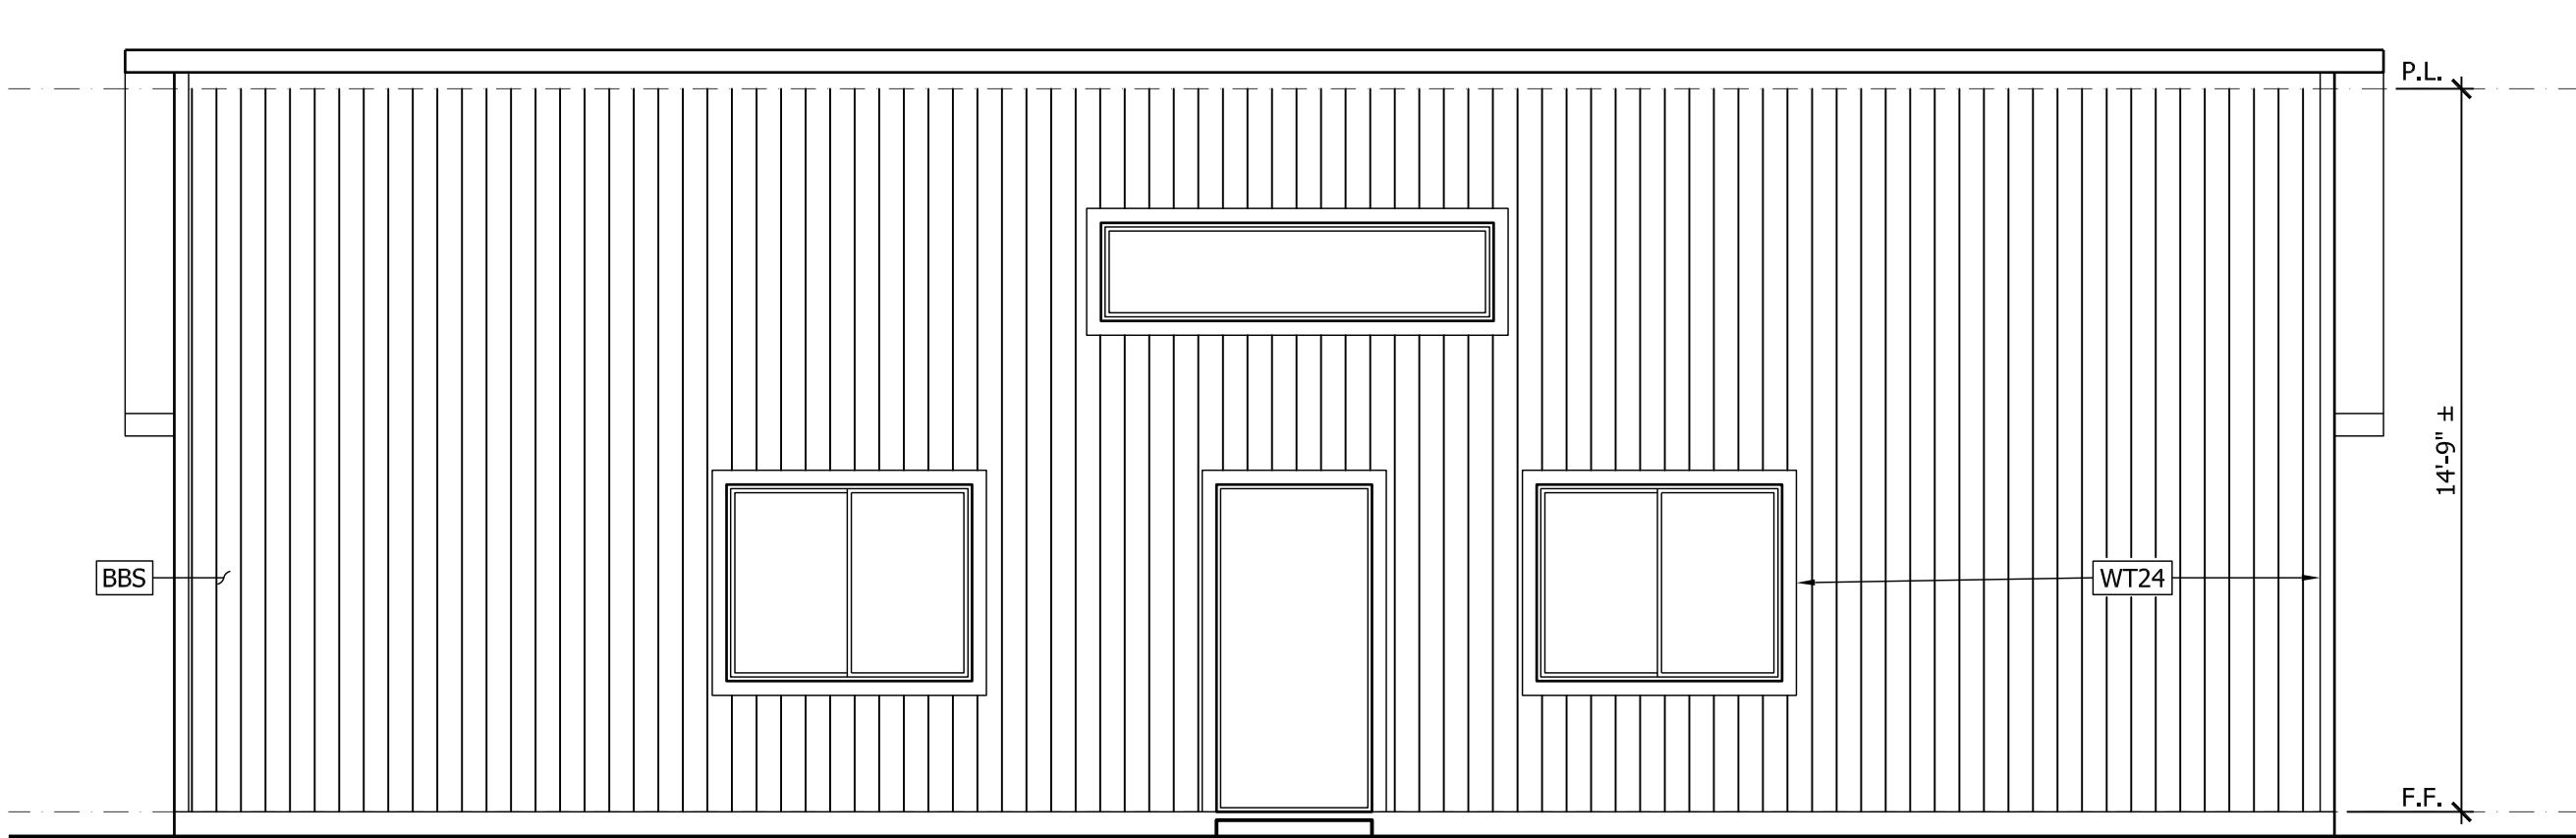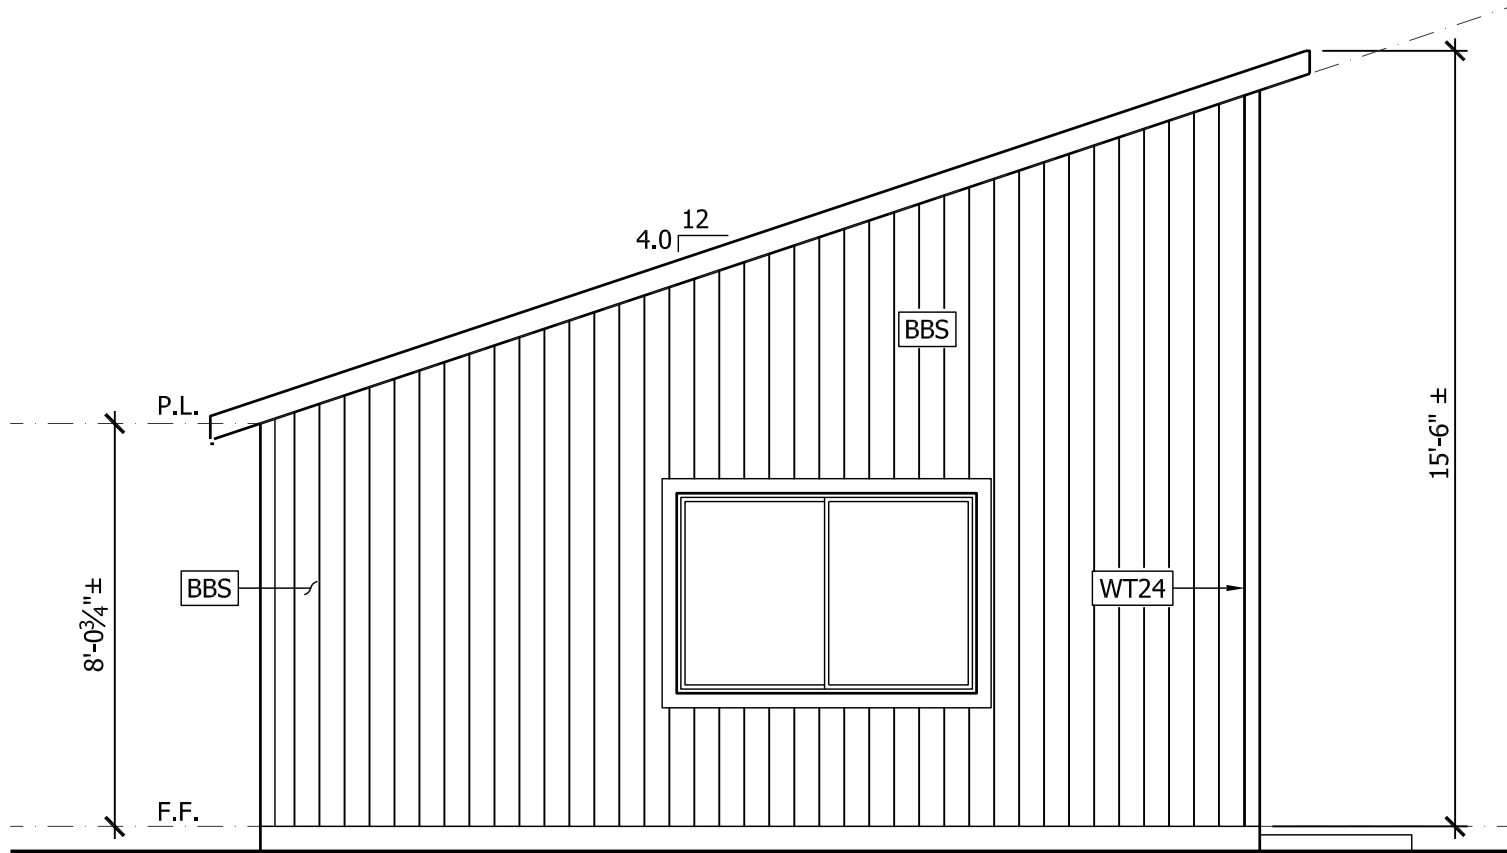

REFERENCE KEYNOTES	
DIVISION 06 - WOOD AND PLASTICS	
MISCELLANEOUS -	
WT24	- 2x4 WOOD TRIM
DIVISION 07 - THERMAL AND MOISTURE PROTECTION	
ROOFING AND SIDING -	
TRS	- TILE ROOF SYSTEM
DIVISION 09 - FINISHES	
CEMENT PLASTER -	
STCO	- STUCCO

