




REFERENCE KEYNOTES	
DIVISION 03 - CONCRETE	
CL	- 4" THICK CONCRETE LANDING, MINIMUM 3'-0" DEEP x DOOR WIDTH. LANDING SHALL NOT EXCEED 1/4 UNIT VERTICAL IN 12 UNITS HORIZONTAL (2%)
CO-F	- CONCRETE FLOOR
DIVISION 06 - WOOD AND PLASTICS	
R-F	- RAISED FOUNDATION
CASEWORK -	
LIN	- FULL HEIGHT BUILT IN CABINET
DIVISION 07 - THERMAL AND MOISTURE PROTECTION	
ROOFING AND SIDING -	
SHG	- CLASS 'A' LIFETIME COMPOSITION ROOF SHINGLES <i>o/</i> 15LB FELT COMPLIANT WITH TABLE R905.1(1). FASTEN ROOFING WITH CORROSION RESISTANT FASTENERS CRC R905.2.5
DIVISION 09 - FINISHES	
ZX4	- ZX4 TRIM
BBS	- 5/8" T1-11 BOARD AND BATTEN SIDING <i>o/</i> TWO LAYER GRADE 'D' PAPER OR 1 LAYER TYVEK. NAILING PER STRUCTURAL
FLOORING -	
LVF	- LUXURY VINYL FLOORING
DIVISION 11 - EQUIPMENT	
DW18	- 18" DISHWASHER
FR30	- FRIDGE, 30" WIDE
MWEH	- MICROWAVE EXHAUST HOOD COMBINATION, MIN VENTILATION RATE OF 100 CFM (CMC TABLE 403.7), HV1 RATED & LIMITED TO 3 SONES, HERS VERIFICATION REQUIRED
R/G-E	- RANGE / OVEN COMBO - ELECTRIC
WD	- STACKED WASHER AND DRYER, PROVIDE MIN 2" STANDPIPE
DIVISION 12 - FURNISHINGS	
BC24	- 24" DEEP BASE CABINET
UC12	- 12" DEEP UPPER CABINET
UC24	- 24" DEEP UPPER CABINET
DIVISION 13 - SPECIAL CONSTRUCTION	
PS	- CLOSET POLE & SHELF
DIVISION 15 - MECHANICAL	
50HPE	- 50 GALLON HYBRID HEAT PUMP ELECTRIC HOT WATER HEATER
MSU	- MINI SPLIT OUTDOOR UNIT, INSTALLED PER MANUFACTURER SPECIFICATIONS
DIVISION 16 - ELECTRICAL	
EPP	- ELECTRICAL SUB PANEL, 120/240V 125A, W/ UFER GROUND
DIVISION 17 - PLUMBING	
BC-S	- BATHTUB SHOWER COMBO
KS-P	- KITCHEN PREP SINK
KS-U	- UNDERMOUNT KITCHEN SINK
SK30	- SINK w/VANITY 30"
SK36	- SINK w/VANITY 36"
TS33	- TILE SHOWER 3x3
WC	- WATER CLOSET, MINIMUM 30" CLEAR WIDTH CENTERED ON WATER CLOSET & 24" CLEAR SPACE OFF NOSE OF WATER CLOSET.

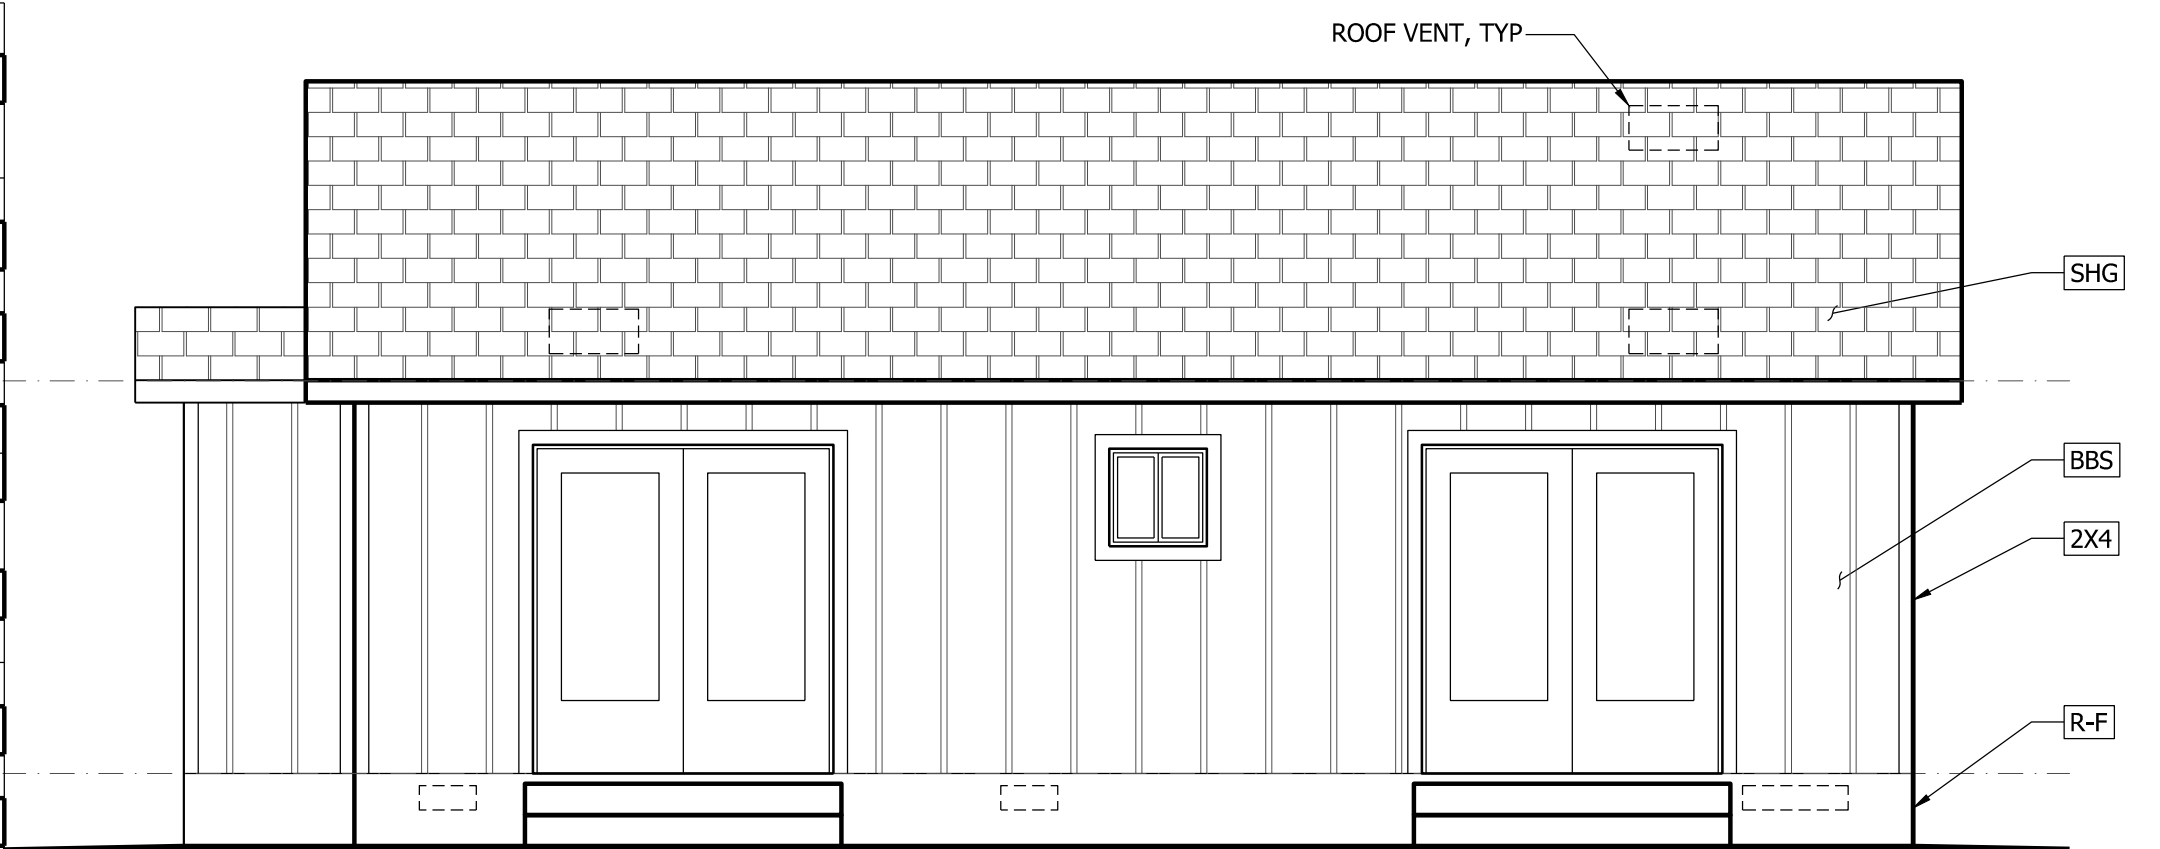


A FRONT ELEVATION
A2.1 1/4" = 1'-0"

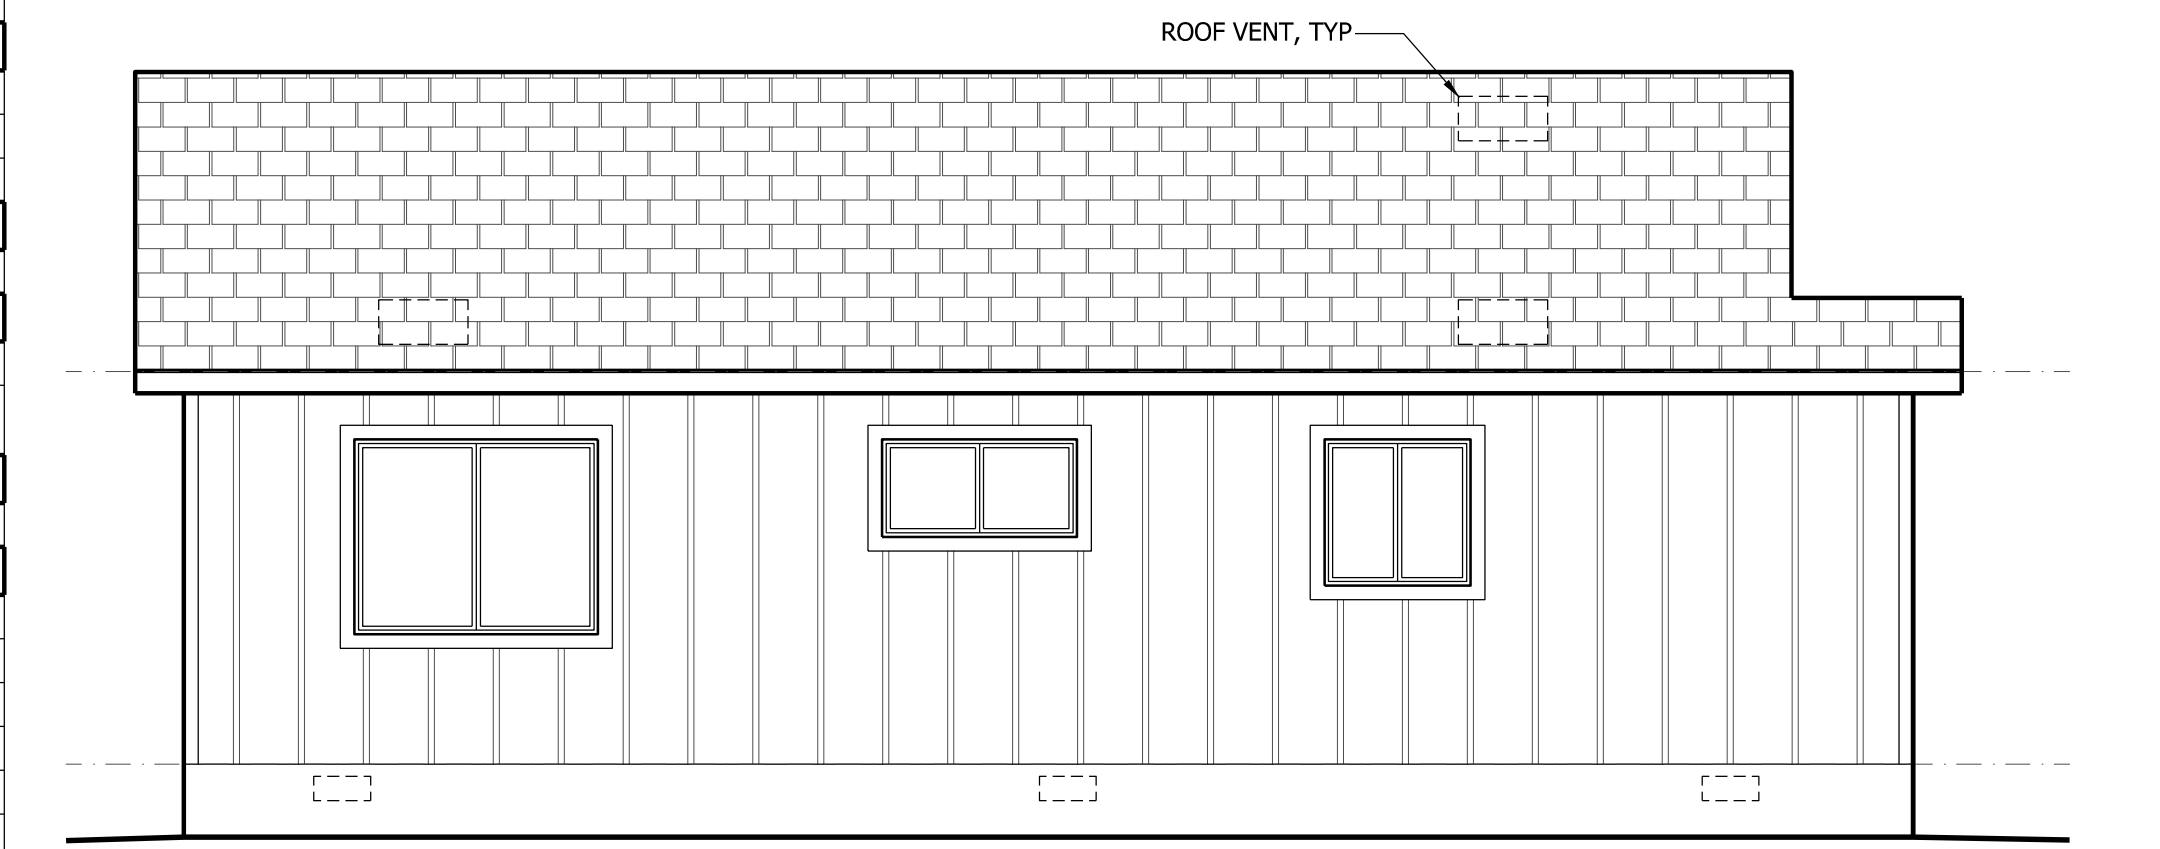

C REAR ELEVATION
A2.1 1/4" = 1'-0"

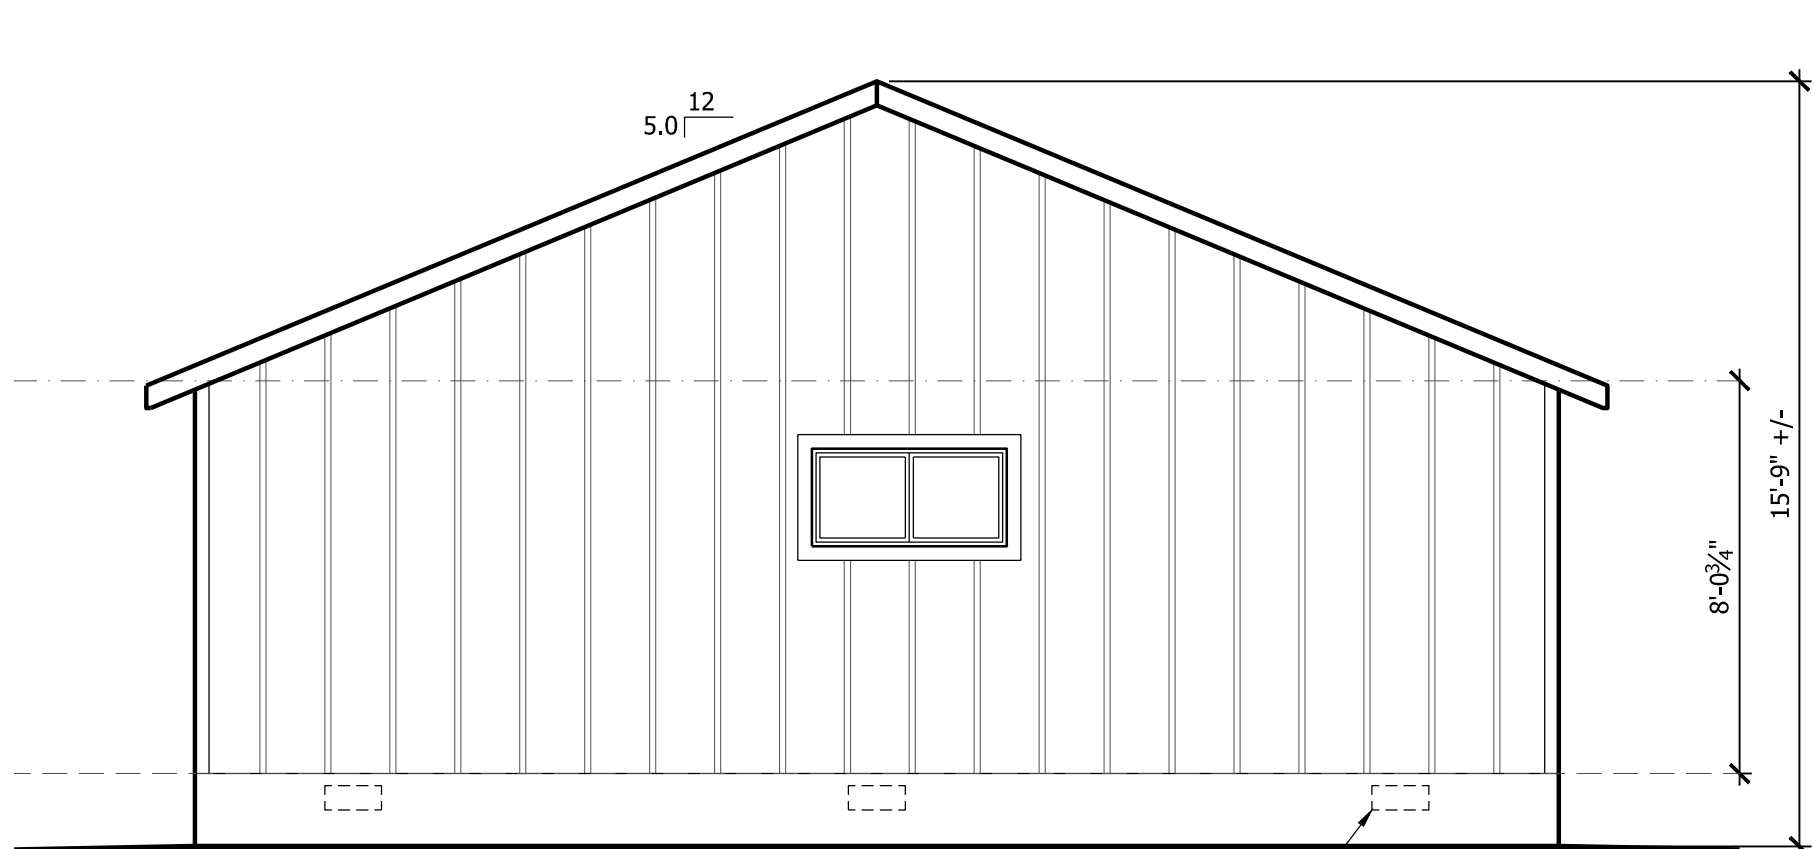


B RIGHT ELEVATION
A2.1 1/4" = 1'-0"

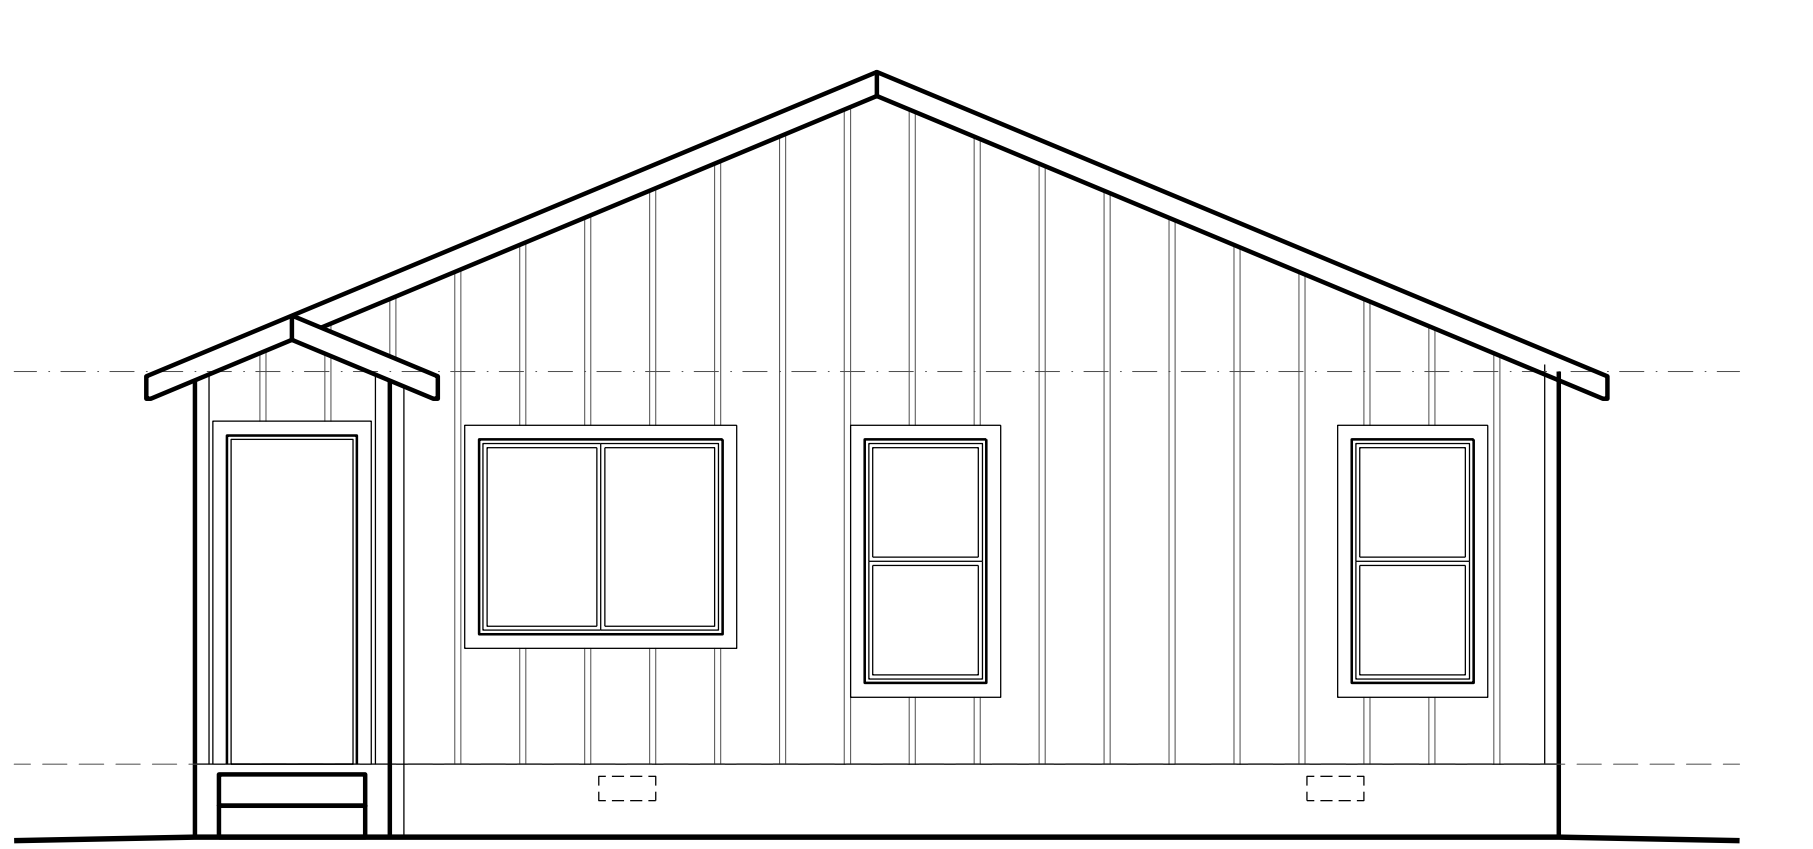

D LEFT ELEVATION
A2.1 1/4" = 1'-0"

DOOR AND FRAME SCHEDULE					
NUMBER	SIZE	STYLE	FIRE RATING	NOTES	
1	PR 3'-0" x 6'-8" x 1-3/4"	DOUBLE - EXTERIOR	--	--	--
2	PR 3'-0" x 6'-8" x 1-3/4"	DOUBLE - EXTERIOR	--	--	--
3	2'-6" x 6'-8" x 1-3/4"	SINGLE - INTERIOR	--	--	--
4	2'-8" x 6'-8" x 1-3/4"	SINGLE - INTERIOR	--	--	--
5	2'-8" x 6'-8" x 1-3/4"	DOUBLE BIFOLD	--	--	--
6	PR 3'-0" x 6'-8" x 1-3/4"	HORIZONTAL BYPASS	--	--	--
7	2'-8" x 6'-8" x 1-3/4"	SINGLE - INTERIOR	--	--	--
8	2'-6" x 6'-8" x 1-3/4"	SINGLE - INTERIOR	--	--	--
9	3'-6" x 6'-8" x 0"	GYPSUM OPENING	--	--	--
10	PR 2'-6" x 6'-8" x 1-3/4"	HORIZONTAL BYPASS	--	--	--
11	2'-6" x 6'-8" x 1-3/4"	SINGLE - EXTERIOR	--	--	--

WINDOW SCHEDULE							
NUMBER	SIZE		STYLE	HEAD HEIGHT	SHCG	U-FACTOR	NOTES
	WIDTH	HEIGHT					
1	5'-0"	4'-0"	SLIDER	6'-8"	.23	.30	
2	3'-0"	3'-0"	SLIDER	6'-8"	.23	.30	
3	2'-6"	5'-0"	SINGLE HUNG	6'-8"	.23	.30	
4	2'-6"	5'-0"	SINGLE HUNG	6'-8"	.23	.30	TEMP
5	4'-0"	1'-6"	SLIDER	6'-8"	.23	.30	
6	4'-0"	1'-6"	SLIDER	6'-8"	.23	.30	TEMP
7	5'-0"	4'-0"	SLIDER	6'-8"	.23	.30	
8	2'-0"	2'-0"	SLIDER	6'-8"	.23	.30	TEMP

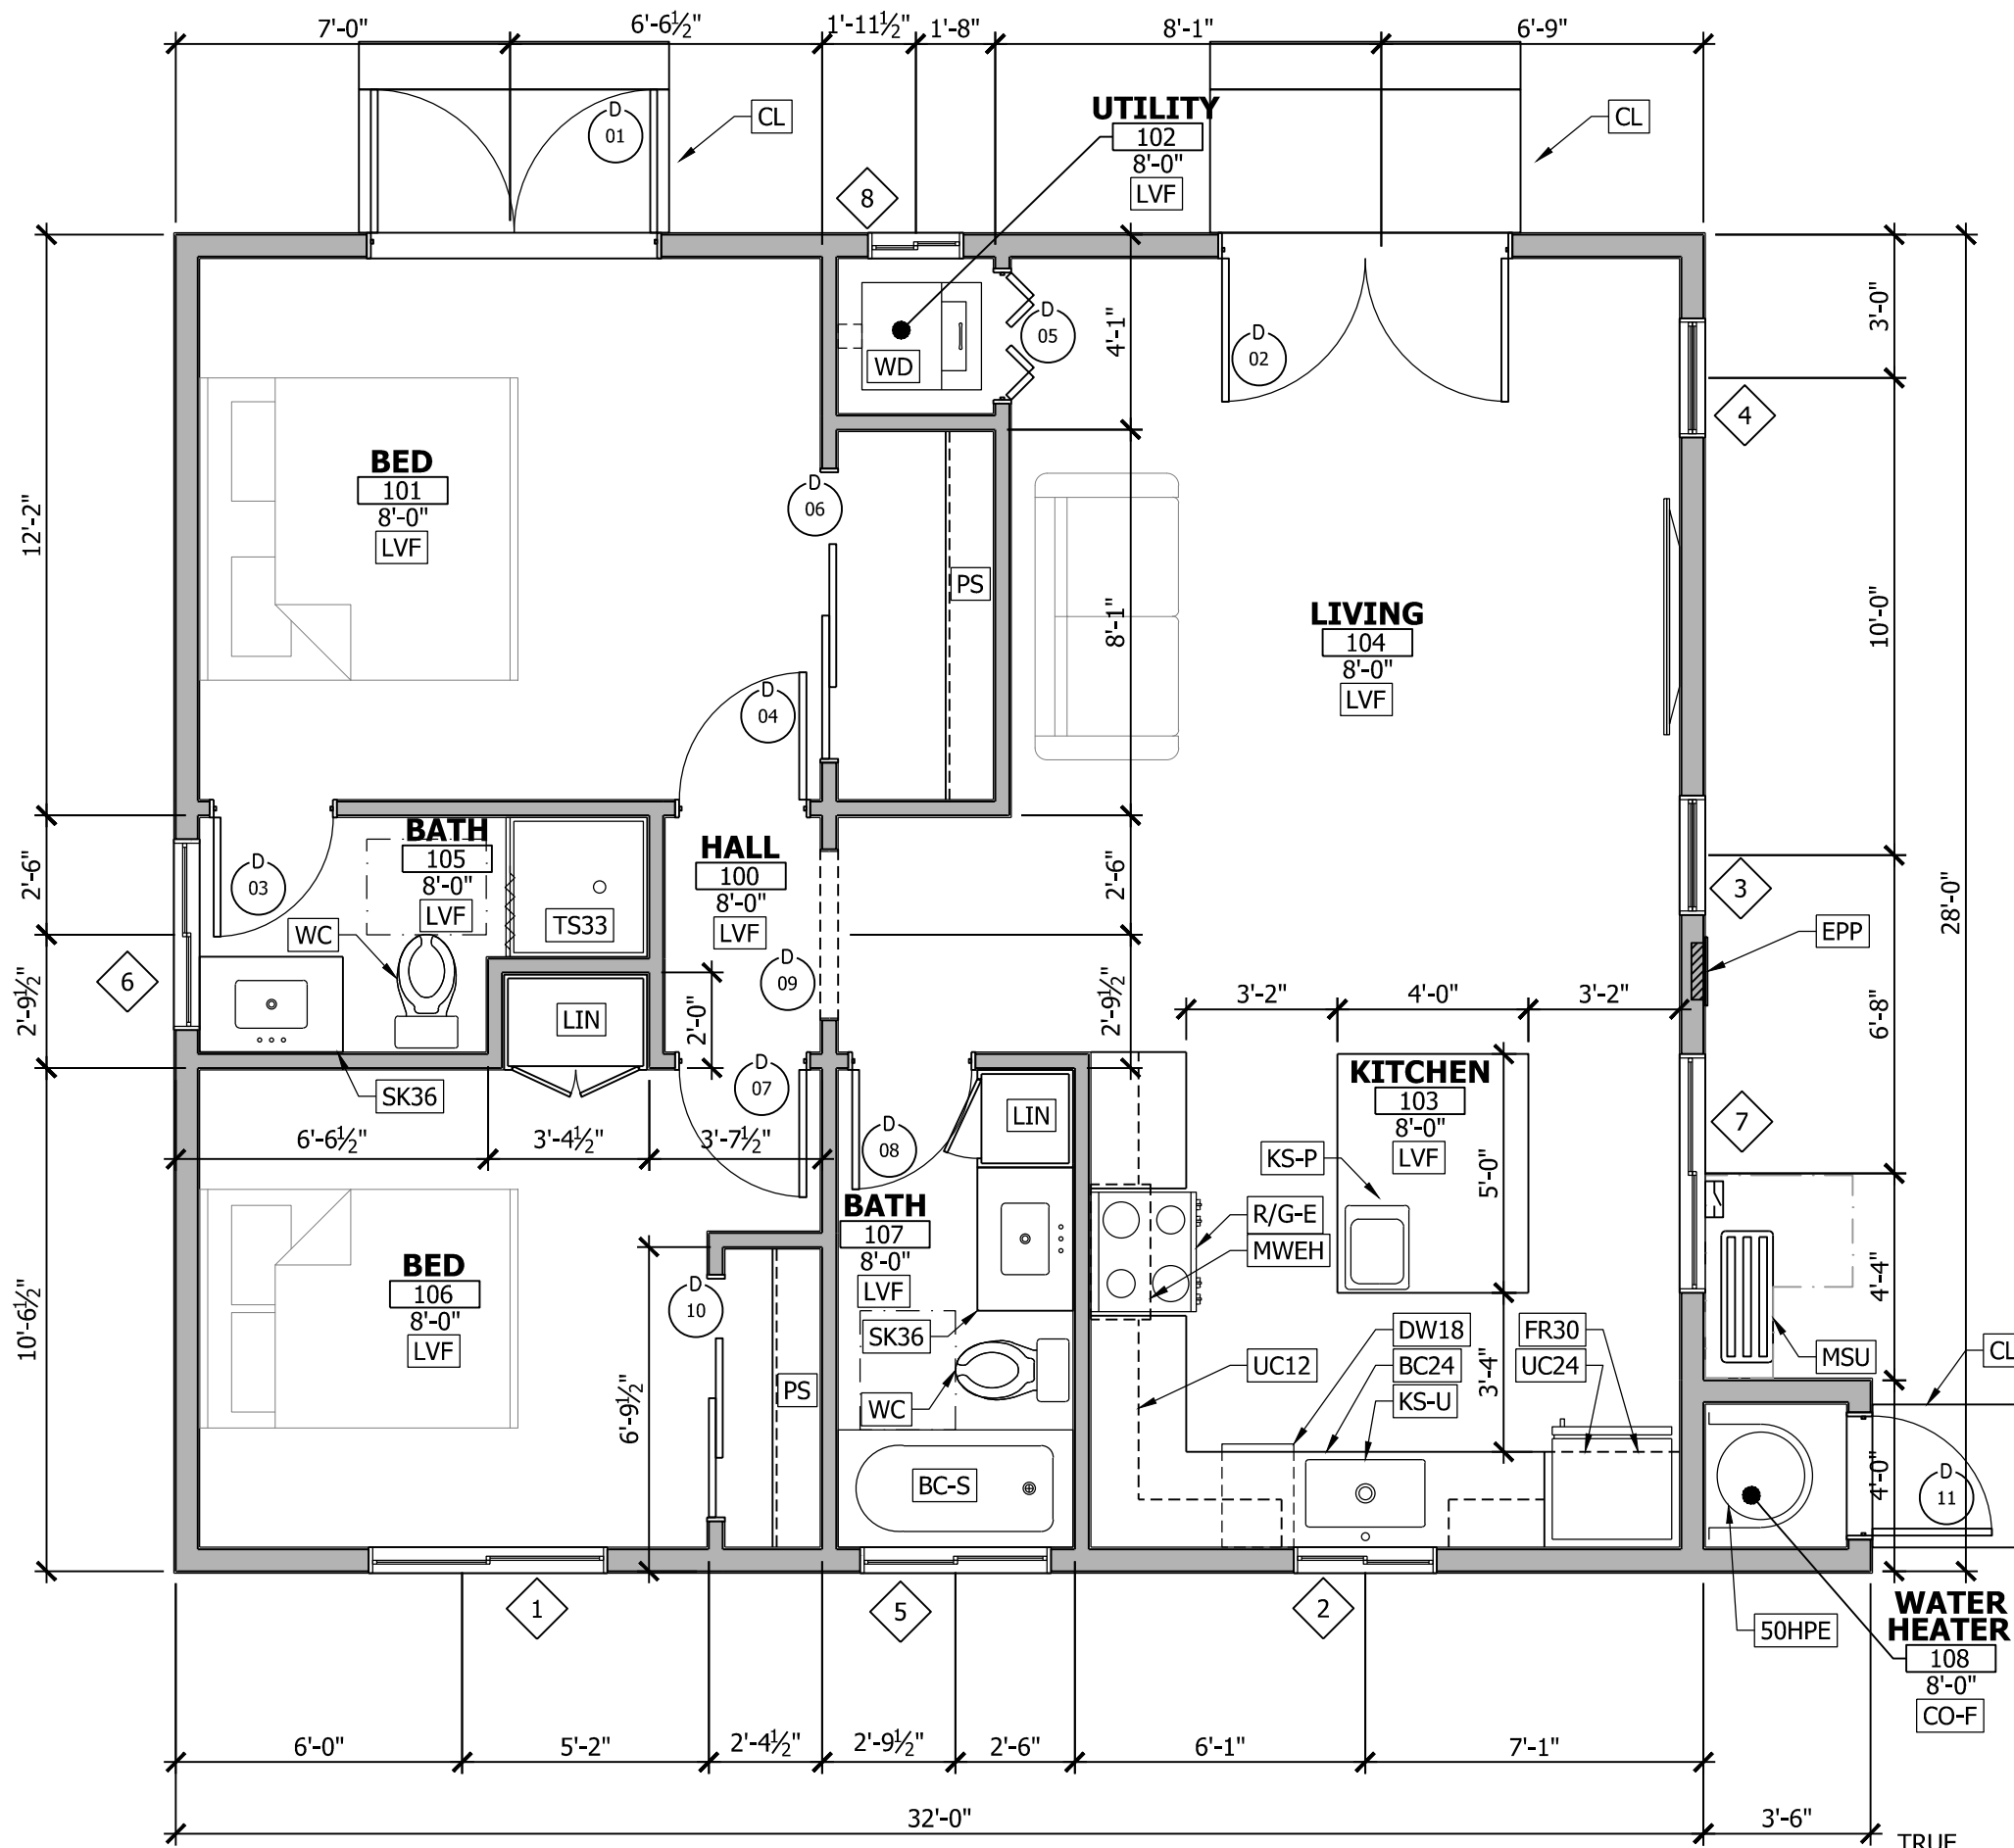

1 FLOOR PLAN
A2.1 1/4" = 1'-0"

896 SF LIVING
14 SF STORAGE

